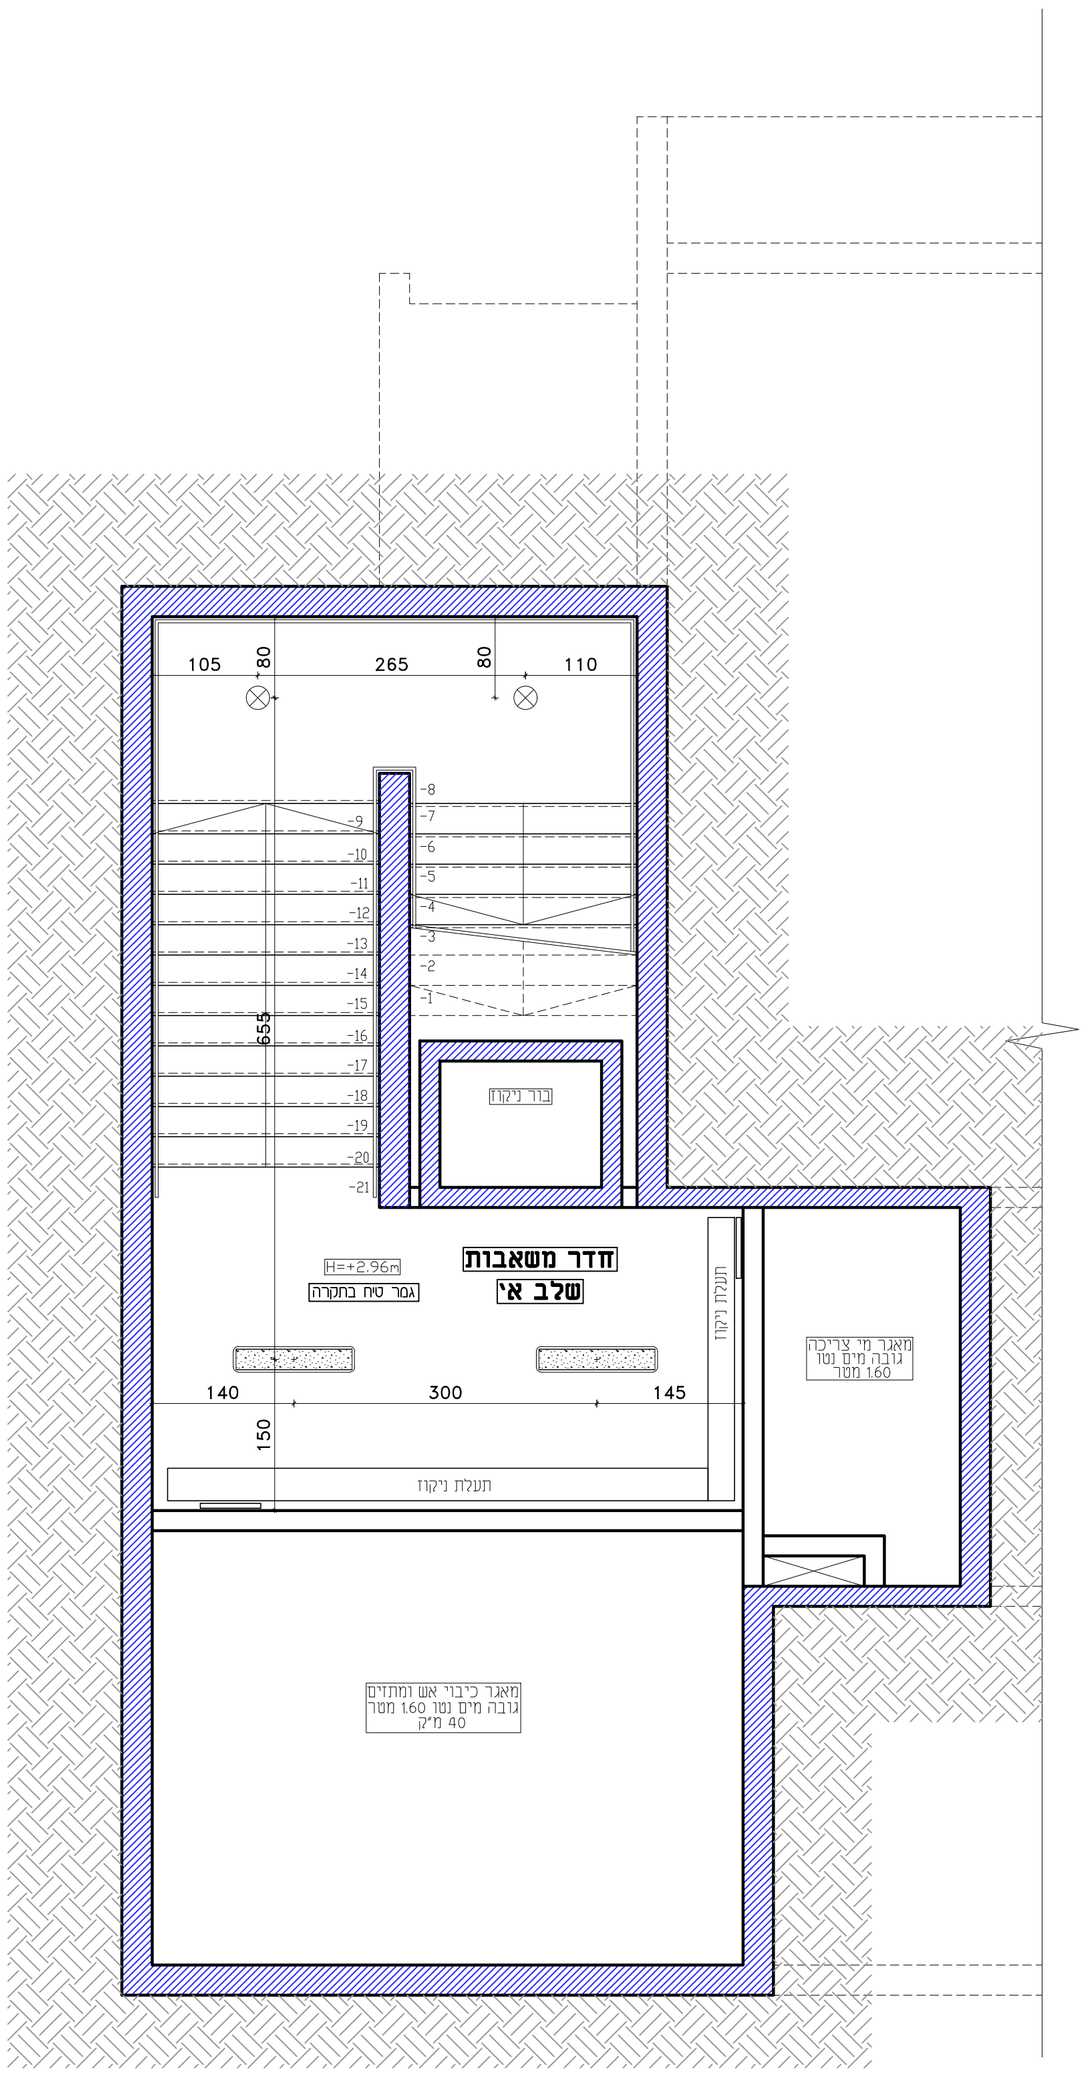

תכנית תקרה אקוסטית-קומת מרתף

קנ"מ 1:50

מקרא:

ג"ת דגם לארא לד תוצרת THORN עם נורת לד 18W גימור בצבע לפי בחירת האדריכל

ג"ת לד דגם IBV771\3 P66204 מוגן מים פוליקרבונט כולל נורת לד 4800LM-4000K LED 40W שיווק לירד שטיינץ

הערות:
- סימון המפלס מתייחס ל-0.00 של הקומה
- ציון וסימון סוגי התקרות בהתאם לרשימת חומרי הגמר
- באם לא מצוין אחרת, סינר הגבס במפלס אחיד עם התקרה הסמוכה

תאריך:	תפוצה:	כמות:

תאריך:	שינוים:	מהדורה:

הערות כלליות:
- המבצע אחראי לבדיקת המידות והתאמתן במקום.
- בכל מקרה של ספק, טעות או אי התאמה יש לפנות למתכנן.
- אין לבצע מידות ע"פ מדידה מהשרטוט.
- חומרי גמר ואבידרי פרזול יורכבו לאחר אישור המתכנן.
- אין לעשות כל שימוש בתכנית זו או ברעיונות הגלומים בה ללא אישור בכתב מהמתכנן
- מהנדס ו/או יועץ אשר שמו רשום מעל שם האדריכל בתכנית זו נושא לבדו באחראיות המקצועית והחוקית לתכנית.

פרויקט:

בית ספר יסודי -24 כיתות + אולם ספורט - מגרש 73 - בת ים

נושא:

תכנית תקרה אקוסטית - קומת מרתף שלב א'

לעיון	לאישור	למכרז 30.09.2024	לביצוע

מזמין:	מס' גליון:	מהדורה:
עיריית בת ים	PC-10	01

אדריכל אחראי:	מבקר:
סלסביל עומרי	דנה מרמור

קנה מידה:	מס' עבודה:	קובץ:
1:50	95/011	DA-95011-01

DATUM Eng Ltd
Engineering Services And Consulting
Tel: 04-6419957 | Fax: 04-6411646 | Kfar Kana 16930 | P.O.Box: 132
E.Mail: Datum@datum-eng.com