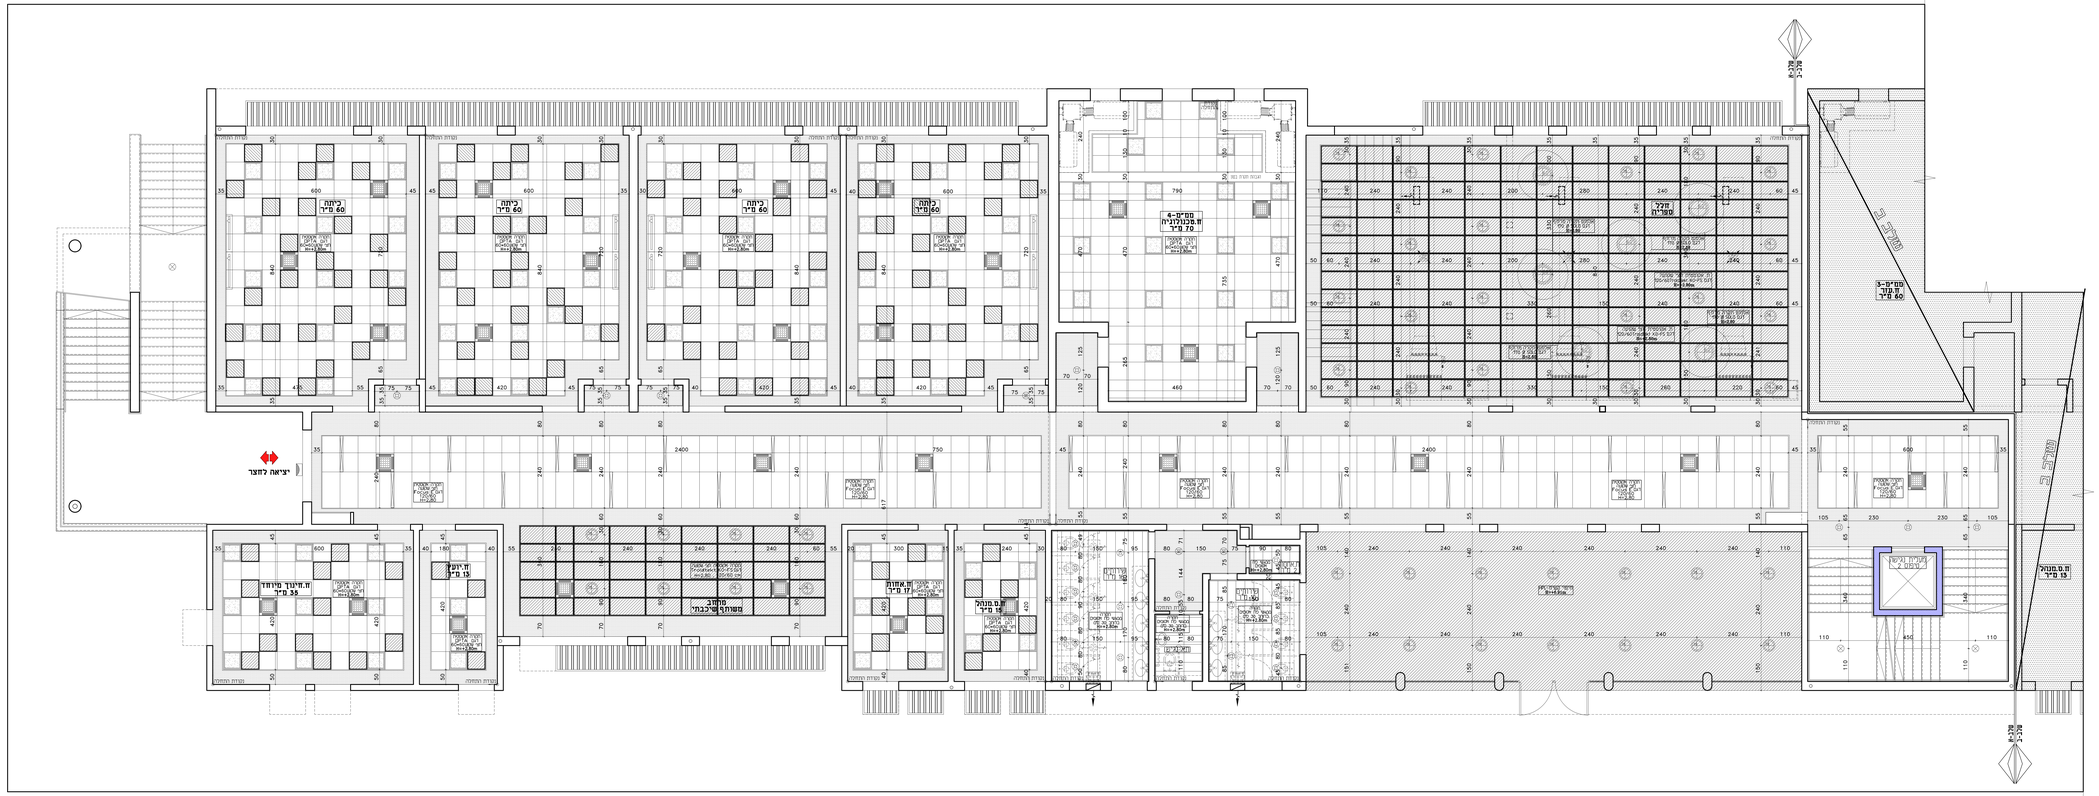

מקרא:

- גיף 60/60 משמן לד
- גיף עגול שטוח בתקרה דגם מימוס לד 1000LM-4000K LED מוזרק עם THORN תוצרת
- גיף דגם לארא לד תוצרת THORN עם מדרגת לד 9W כחול נצנוץ עבר בחירת האדריכל
- גיף עגול שטוח בתקרה דגם G-SAVRIC צהוב כיוון עם בחירת בגוון עמה עבר בחירת האדריכל 20w-2300LM-4000K/3000K 47w-4800LM-4000K/3000K קומר 60
- מרפיר תאורה שטוח
- גיף לד 24w לשארת מחוץ כיתה תוצרת 5150046 עם מיכס
- גיף דגם הרקאיס לד שוטוק לירד שטריק כולל מדה לד 26W
- אטמים תקרה מרחוק דגם SOLO
- תקרת שבבי עץ דגם 60*120\60*60-TROLDTEKT מרופלים עם מרוחל מסוג T24
- תקרה אקוסטית תאי שטוח 50/50 דגם Focus E
- תקרה אקוסטית תאי שטוח דגם Troldtekt 50/50
- ארון מיכלי 60/60 תאי שטוח (דגם מיקרוגדה תקרות אקוסטיות)
- מעבר מים ברוחב 50 מיס ללא מירוד
- מחזיק גבס מחוכלל

הערות:
- הרחון ומפלס מתייחס ל-0.00 של הבתיה
- גיין ומיזון סוב. הבקרות בהתאם בשאיפה מחוזי הנמד
- כאל לא תקיין אחדיל. מיזוד הגבוה בתיבים אחדיל עם הבקרה המתיכה

תאריך	הערה	מספר

תאריך	שינוי	מהדורה

הערות כלליות:
- המבנים אחראי לבדיקת הפרדות התאמתן בתיבות.
- בכל מקרה של סתיר, מעדיף את ה הוראה ש נקבה למתכנן.
- אין לבצע מדידה ע"פ מדידה מהשרטוט.
- תחתי עמד ואריחי פ"מ יירבנו לאחר אישור המתכנן.
- אין לשנות כל שימוש בתבנית זו אי בגישרות ובגלמים בה בלא אישור בכתב מהמתכנן.
מבנים ראש יקבל אאר עמד רשום מעל מעל האדריכל בתבנית זו מעמ לגבי אחראיות ומקצועית המחיבת עליהם.

מרקם:

בית ספר יסודי -24 כיתות + אולם ספורט - 73 מ"ר בת ים

משרד:

הכנסת הקרקע אקוסטית -שלב ג' קומה א'

לעיון	לאישור	למכרז 30.09.2024	לביצוע

משרד: עיריית בת ים	מס' עדכון: PC-12	מהדורה: 01	
אדריכל אחראי: סלסביל עומרי		מנהל: דנה מרמור	
שנה מידה: DA-95011-01	מס' עבודה: 95/011	שרטוט: 150	

DATUM Eng Ltd
Engineering Services And Consulting
Tel. 04-6499957 | Fax. 04-6471646 | Kfar Kana 16/930 | P.O.Box: 192
E.Mail: Datum@datum-eng.com