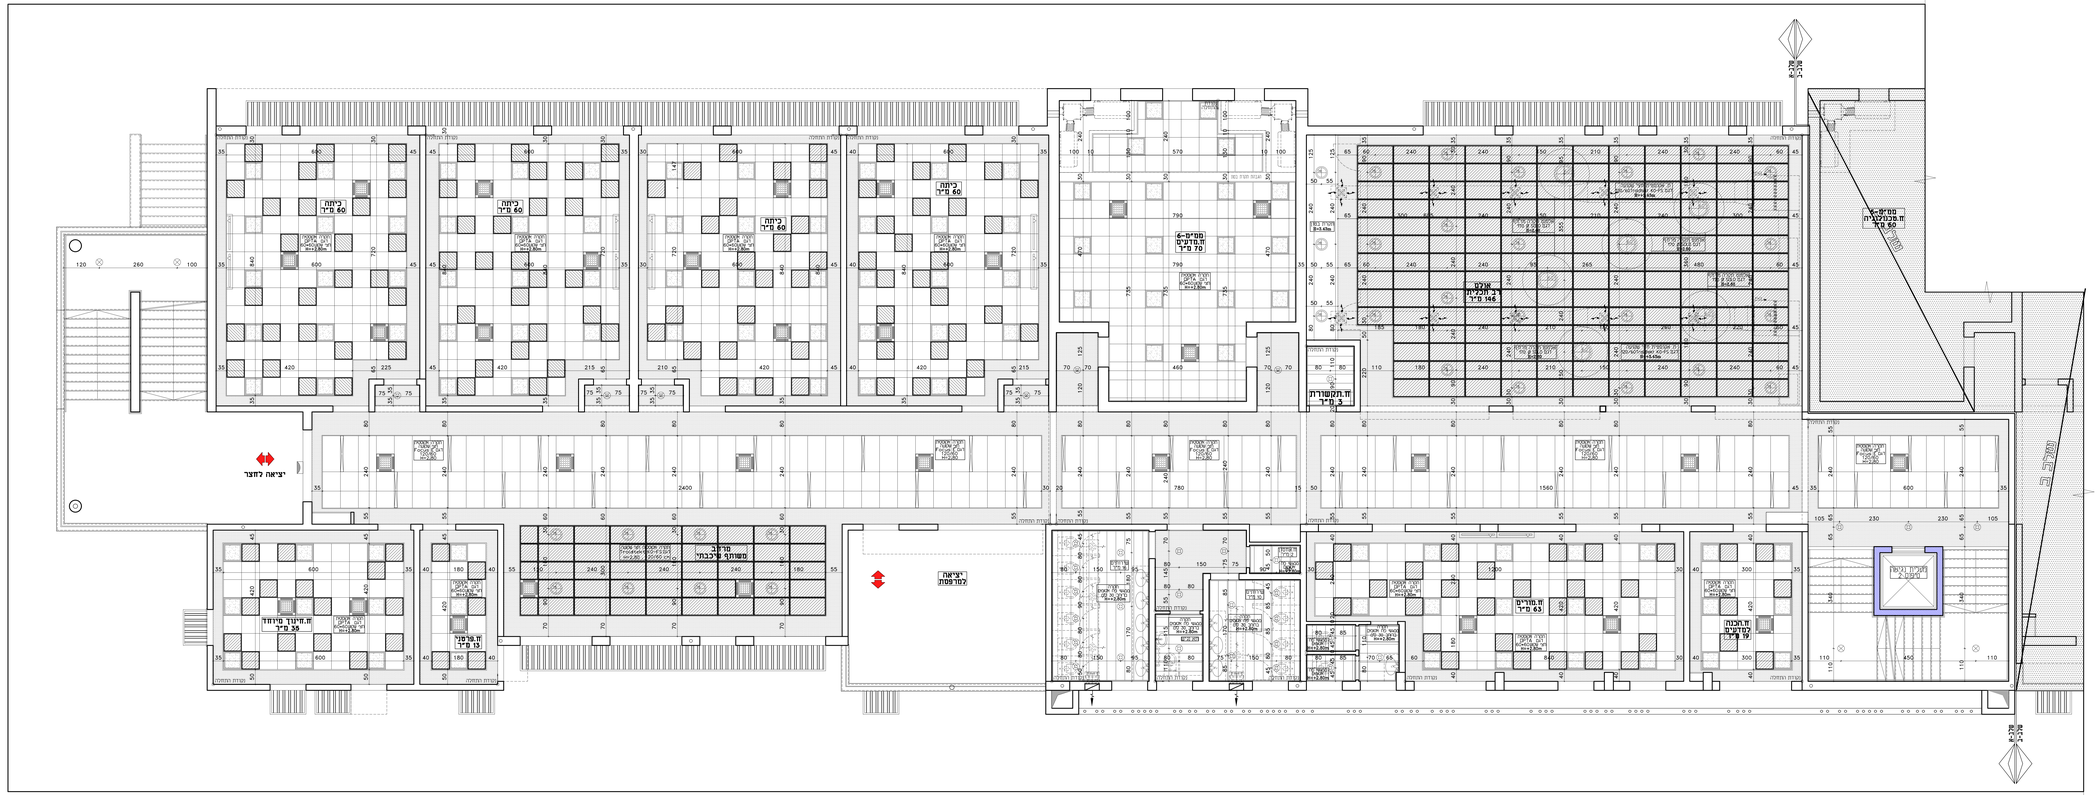

מקרא:

- ניק 60/60 חשמל לד
- ניק עגול שטוח בתקרה דגם מיתוס לד 1000LM-4000K LED תוצרת THORN עם גוף חלבי
- ניק דגם לארא לד תוצרת THORN עם גוף לד שחור כיסוי נגטיב לבן בתיקרת האולי"כ
- ניק עגול שטוח בתקרה דגם G-SAVALC שחוק לירד שחיקן בגוון עמוד לבן בתיקרת האולי"כ 20W-2300LM-4000K/3000K 47W-4800LM-4000K/3000K
- פרופיל תאורה שקוע
- ניק לד 24W לתוארת מתח כיתה תוצרת LUMIS 5150046
- ניק דגם הרמאיק לד שחוק לירד בגוון שחיקן כולל גוף לד 26W
- אמתח תוצרת מרחף SOLO דגם
- תקרת שבבי עץ דגם TROLDTEKT 60*120\60*60 פרופילים עץ פרופיל מסוג T24
- תקרת אקוסטית תאי שטיחה דגם Focus E 120/60
- תקרת אקוסטית תאי שטיחה דגם דאשבורד 120/60
- ארייזי מתכת 60/60 תאי שטיחן דגם AcoFix (תקרת אקוסטיקה)
- מגשר פח ברוחב 30 מיס ללא חירור
- מחיצת גבס מחמלק

הערות:
- מיחוי הנמכת מחייחס ל-0.00 של הנמוכה
- אין לוחמן סוג התקרה בתאום ובשאלה מחמיר הנמר
- באם לא מצוין אחרת מיחוי הגבס בחיבור אחיד עם הנמוכה הנמוכה

תאריך	חוצה	כמות

תאריך	שינוי	מהדורה

הערות כלליות:
- המבנים אמורים לבריכת הנדיות והתאמתן בחומר.
- בכל מקרה על מפלס מגוון אי אי הלאומי"ם לקמת למחסנן.
- אין לבנים אידיות ביס מדרגה מהשמים.
- חמר - גמר ואביזרי מיחוי יהיבנו לאחר אישור המחסנן.
- אין לשנות כל שחוס בתכנית זו אי ברשיוות ובלמים בה ללא אישור מראש ובכתב מהמתכנן.
- מרגע זה ואילך יקבל אשר שנה רשם חוב שם האדריכב בתכנית זו ושאו לבנין באמוראות ומאמצעת המחוזית לתכנית.

פרויקט:
בית ספר יסודי -24 כיתות + אולם ספורט
- מגרש 73 - בת ים

נושא:
תכנית הקרקע אקסטיקה -מבנה א' קומה 2

לעיון	לאישור	למכרז 30.09.2024	לביצוע

משרד	מס' גיליון	מהדורה
עיריית בת ים	PC-13	01

אדריכל אחראי	מנהל
מסטביץ' עמרי	דנה מרמור

עמ' מידה	מס' עבודה	שבע
DA-95011-01	95/011	150

DATUM Eng Ltd
Engineering Services And Consulting
Tel: 04-6499957 | Fax: 04-6498646 | Kfar Kana 16930 | P.O.Box: 192
E.Mail: Datum@datum-eng.com