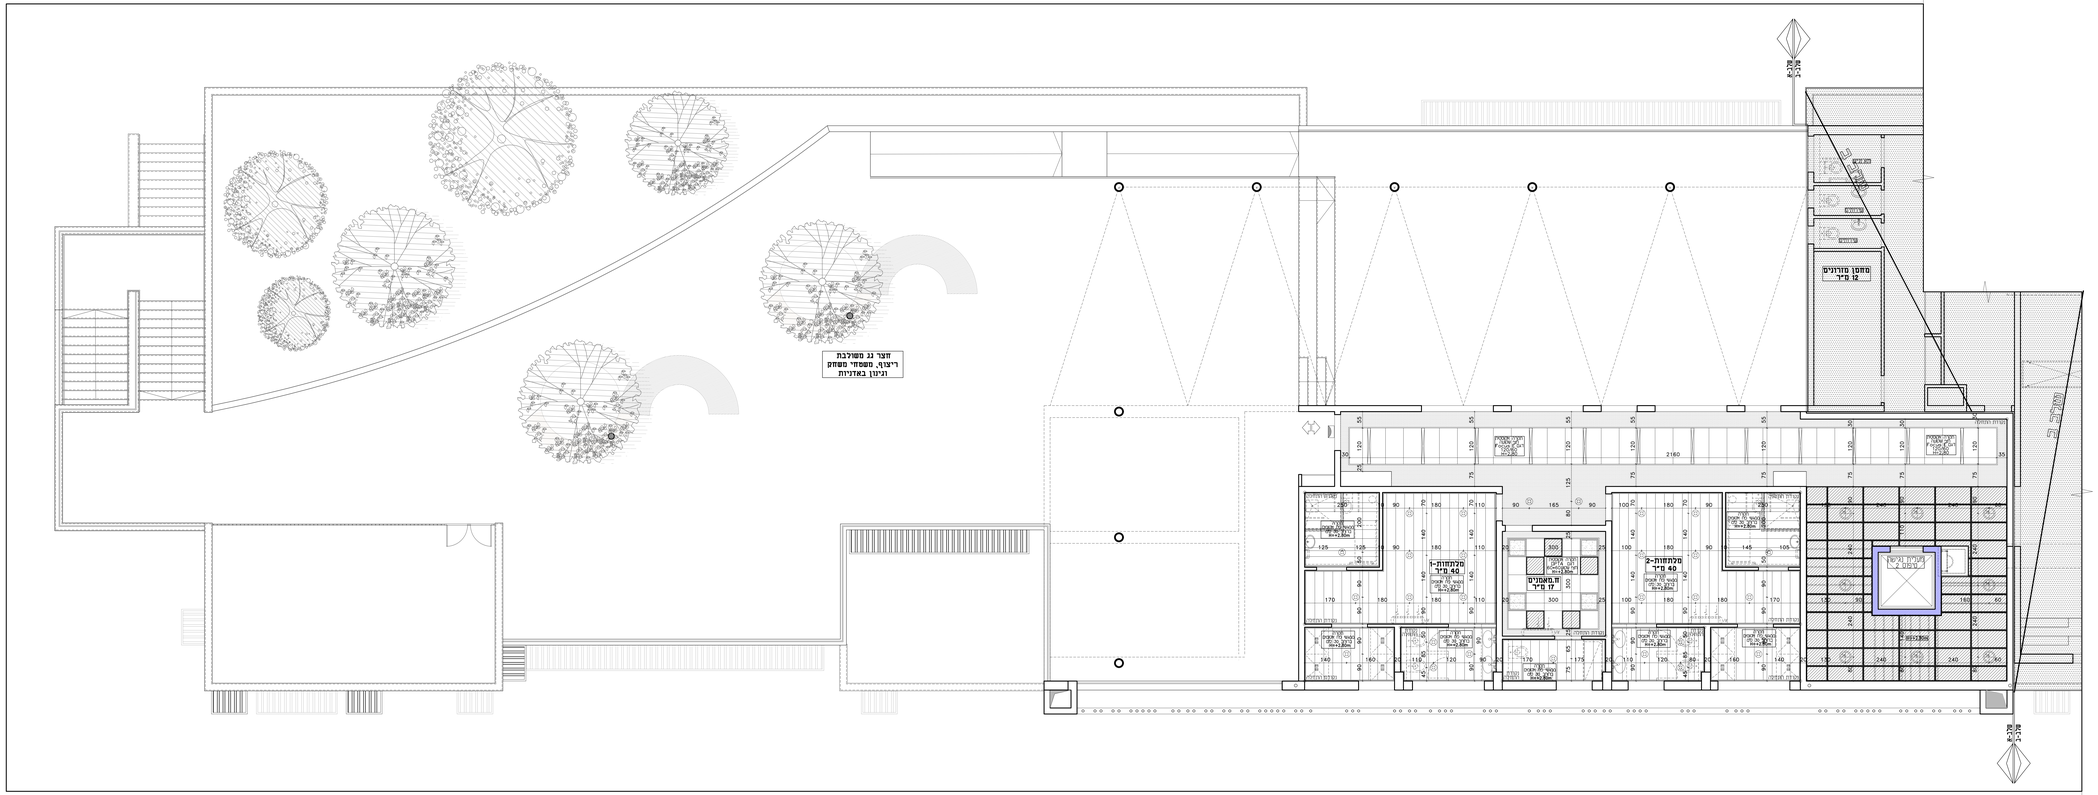

מקרא:

- גוף 60/60 משטח לד
- גוף עגול שקוע בתקרה דגם פיטנס לד 1000LM-4000K LED מדגם THORN תקרה
- גוף דגם לארא לד תקרה THORN עם מדף לד 9W נמוך בגובה לפי בחירת האדריכל
- G-SUNVILE גוף עגול שקוע בתקרה דגם עדוכן לירד שטרק בגובה עמוד לפי בחירת האדריכל
- 20W-2300Lm-4000K/3000K 47W-4800Lm-4000K/3000K קוטר 60
- פרופיל תאורה שקוע
- גוף לד 24W לתאורת מדף ביתה תוצרת עגם מקס 5150046
- גוף דגם הרשאן לד שוקע לירד שטרק בגוף מדף לד 26W
- אמצעם תקרה מרוחף דגם SOLO
- תקרת שבבי עץ דגם TROLDTEKT 60*120\60*60- פרופילים עץ פרופיל מסוג 124
- תקרה אוטמטית חצי שקועה דגם Focus E 120/60
- תקרה אוטמטית חצי שקועה דגם Troldtekt 120/60
- ארונות מיוחדי 60/60 חצי שקוע (דגם בלאקליגהט תקרות אוטמטיות)
- מגשר פח ברוחב 30 סמ כלא חירור
- קחתת גבס מחוזק

הבהרות
- פיתוח המגרש מתייחס ל-0.00 של הבתה
- עיין ומתאם מול האדריכלים בתאום כלשהם חומר וגמר
- כאם לא מצוין אחרת, כיור הגבס בתפרים אחיד עם התקרה המסיכה

תאריך	תמצה	כמות

תאריך	שרטט	מהדורה

הערות כלליות
- המבנים אחוריר לבדיקת המידות והתאמתן במקום.
- בכל חברה עם מלא, מבנה אל אל המאמר יש דפות לתחכון.
- אין לבצע מידות בעיי מדידה מחשבים.
- תמרי נמוך ובגיהר ציר יוכבו לאחר אשר המתכנן.
- אין קשרת כל שרחוב בתכנית זו אי בריחות וגלמים בה בלא אשר בכתב מחתכנ.
- מהנדס ישא יזכר אשר אחר ושם מעל מעל מעל האדריכל בתכנית זו ומשא בגבר באחריות המקצועית והחוקית בלבדה.

מיקום
בית ספר יסודי -24 כיתות
+ מרכז ספורט
- מגרש 73 - בת ים

נושא
תוכנית חקרת אקוסטית -שלב א'
קומת ג'

לעיון	לאישור	למכרז 30.09.2024	לביצוע

משרד	עירייית בת ים
מס' גיליון	PC-14
מהדורה	01
אדריכל אחראי	סטפניק עומרי
מנהל	דנה מרמור
שנה מידה	1:50
מס' עבודה	95/011
שרטוט	DA-95011-01

DATUM Eng Ltd
Engineering Services And Consulting
Tel: 04-6499957 | Fax: 04-6499646 | Kfar Kana 16930 | P.O.Box: 192
E.Mail: Datum@datum-eng.com