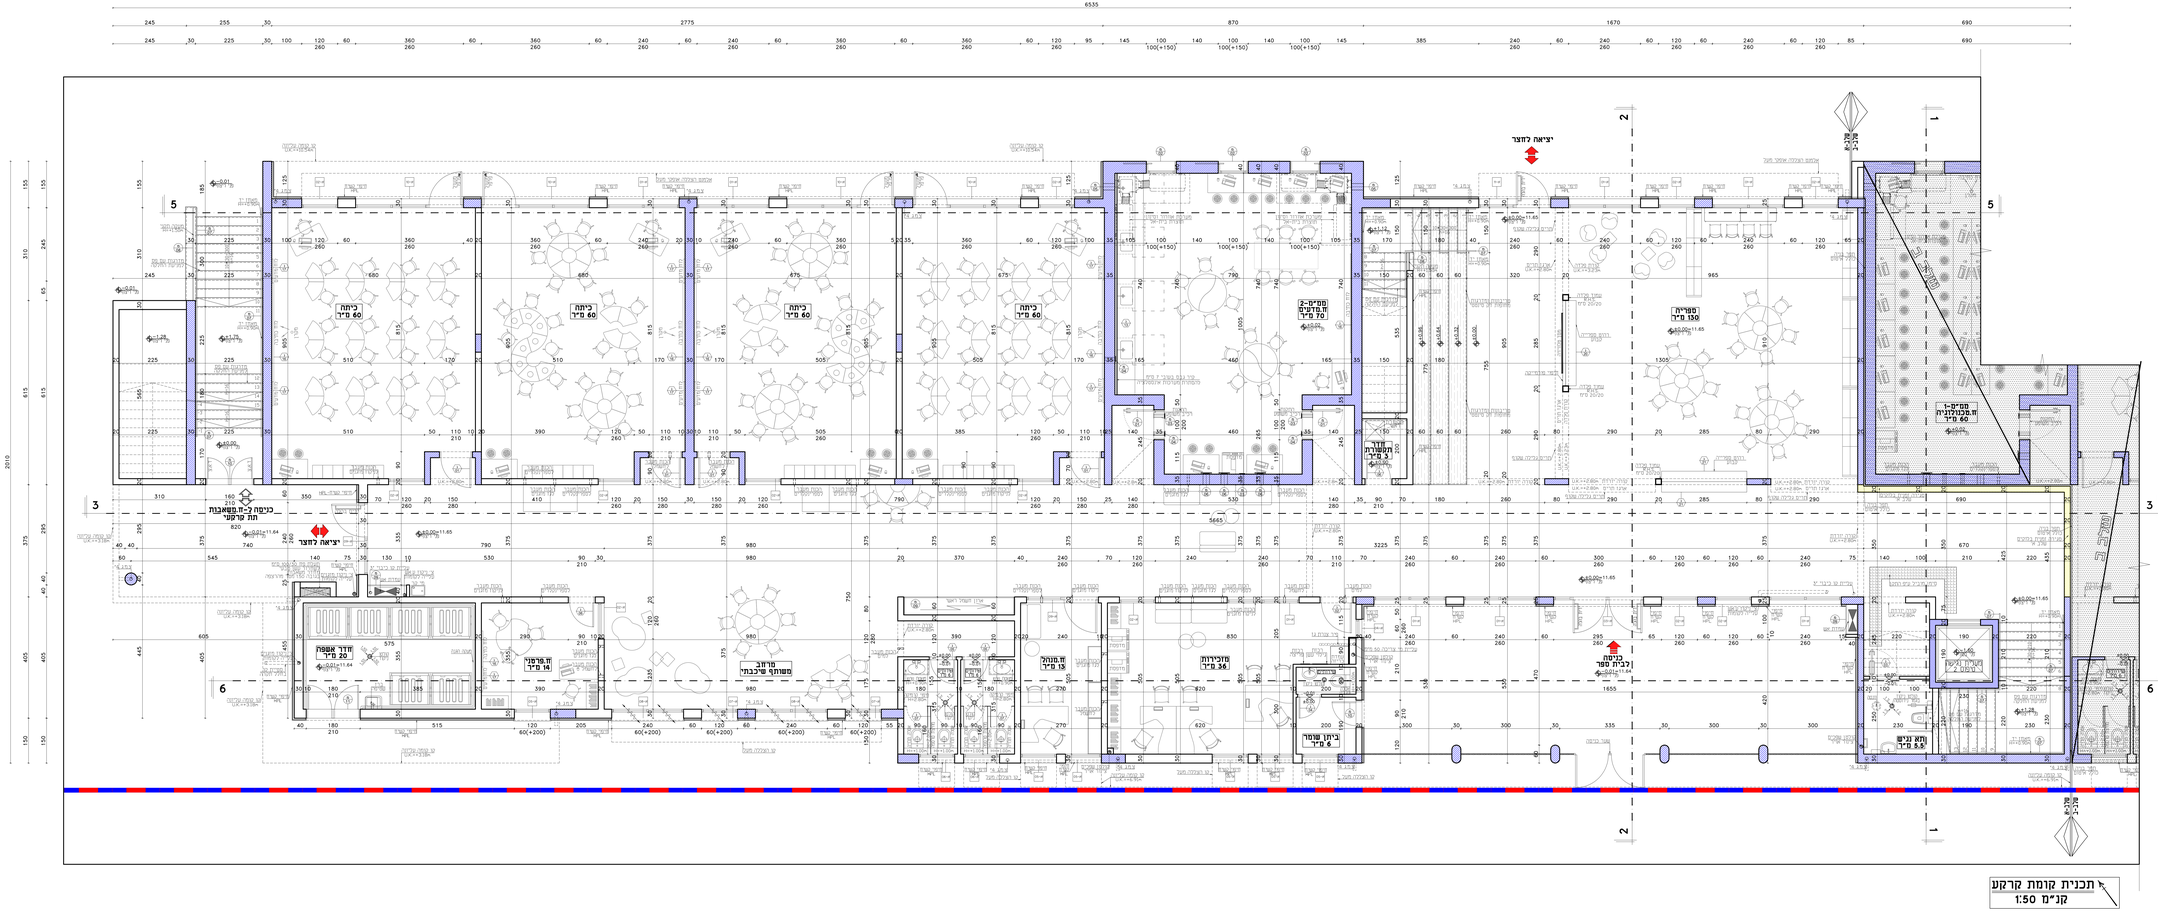

תאריך	תיאור	כמות

תאריך	שרטט	מהדורה

הערות כלליות
המבנים אחוזר לבריכת הנדיבות המאוחדת בחסום
בכל מקרה אל מול מקום, מקום אל מול הנאמנים ש קמות למחבנו.
אין לבצע מידות על פי מדידה מחשבים
תמרי נמל האביר פרסם יהיבנו לאחר אישור המחבנו.
אין לשנות כל שמשם בתכנית זו אי ברשומת וגלמים בה ללא אישור
בלתי מוסמכנו.
מבנים ראש יקון אשר שתו ישם מעל אל האדריכל בתכנית זו ושמ
לבדו באוראות מלאכתית המחיבת מוכנת.

מיקום
בית ספר יסודי -24 כיתות
+ מגרש ספורט
- מגרש 73 - בת ים

נושא
תכנית קומת קרקע
-מגרש א'

לעיון	לאישור	למכרז 30.09.2024	לביצוע

משרד	מס' גיליון	מהדורה	
עריית בת ים	PL-02	01	
אדריכל אחראי	מבנה		
סטסבייל עומרי	דנה מרמור		
עמוד מידה	מס' עבודה	שבע	
DA-95011-01	95/011	150	

DATUM Eng Ltd
Engineering Services And Consulting
Tel. 04-6419997 | Fax. 04-6419646 | Kfar Karia 16/990 | P.O.Box. 192
E.Mail: Datum@datum-eng.com