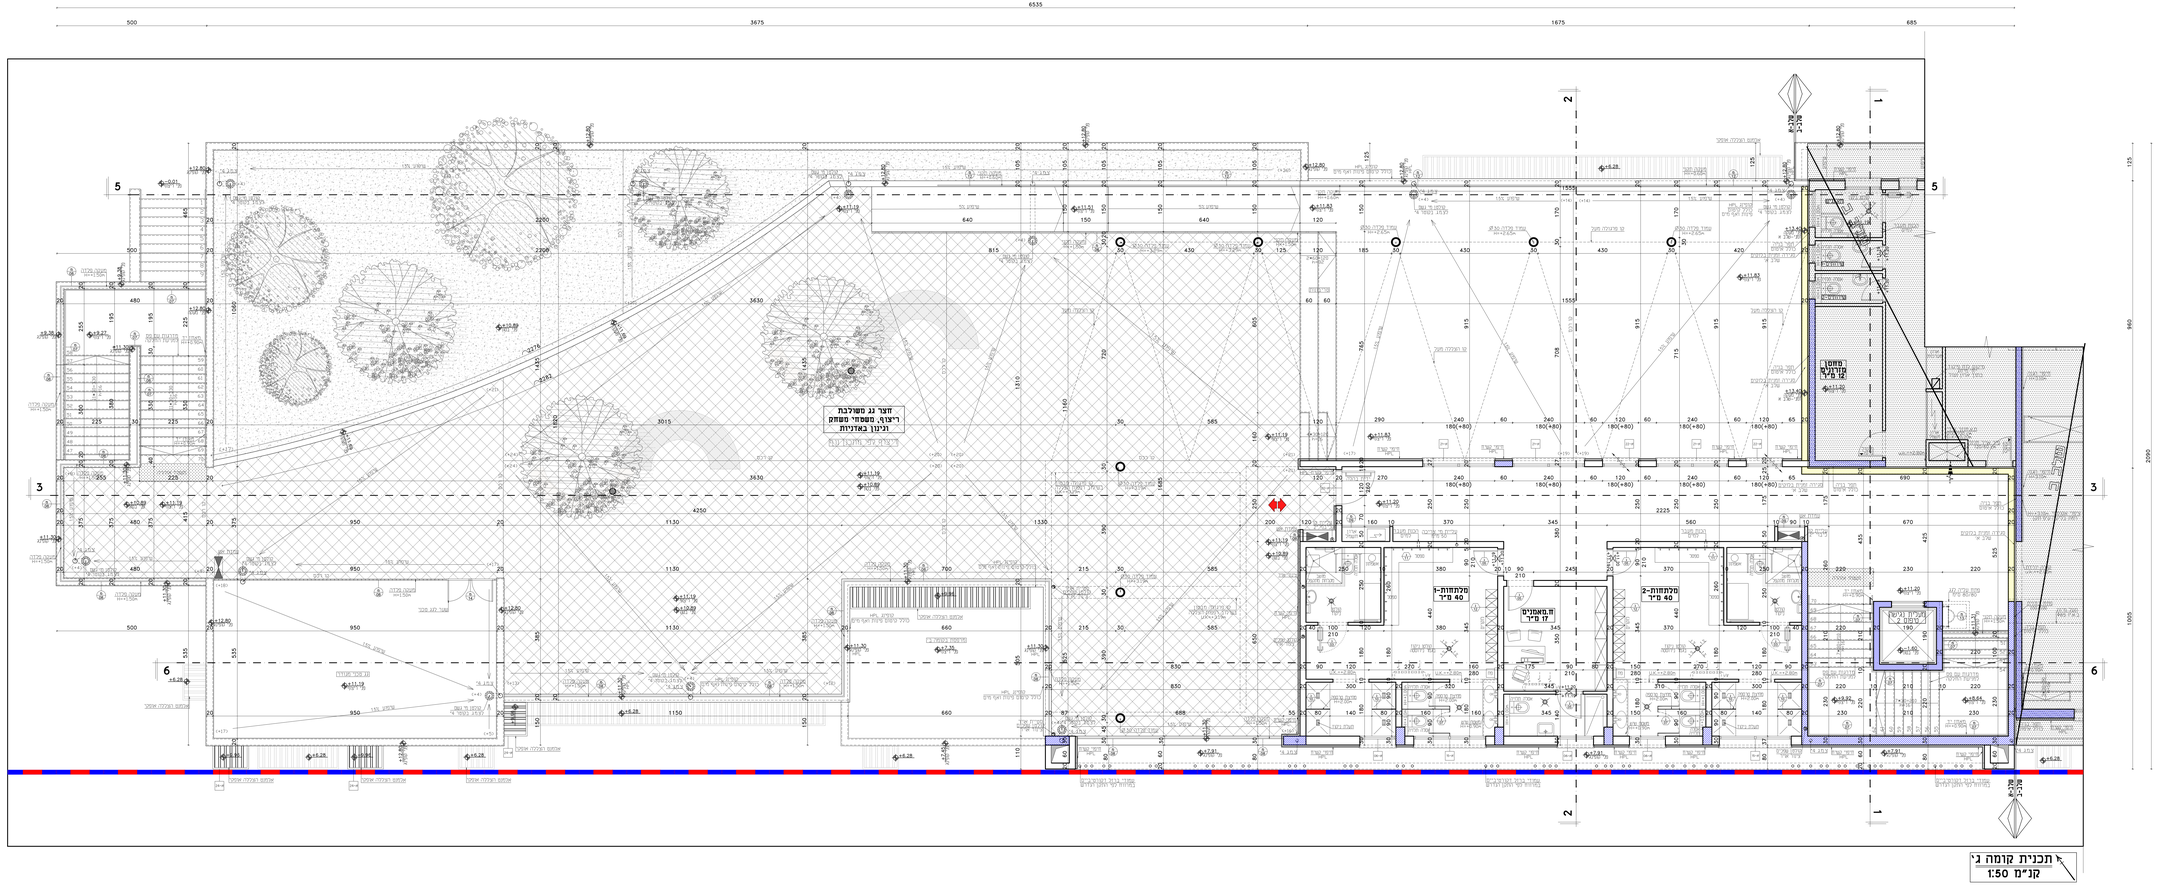

תאריך	הערה	כמות

תאריך	שרטט	מהדורה

הערות כלליות

- המבנים אחוריר לבדיקת הגדילות המאמתון בחסום.
- בכל מקרה של סתירה, עדיף מקום אל מול מקום אל מול הגאומה שם כמות למחבנן.
- אין לבצע מידות ע"פ מדידה מחשבים.
- תמרי נמל האביר פרטי יהיבו לאחר אישור המחבנן.
- אין לעשות כל שימוש בתכנית זו אם ברעדות וגמלים בה ללא אישור בכתב מהמחבנן.
- מבדק ראש יקוץ אשר שמו מעל מגל האדריכל בתכנית זו משא לבדו באחריות מלאכתית המחוקת מתכנית.

פרויקט

בית ספר יסודי -24 כיתות
+ אולם ספורט
- מגרש 73 - בת ים

שם

תוכנית קומה ג'
קנ"מ 1:50

לעיון	לאישור	למכרז	לביצוע
		30.09.2024	

משרד	מס' גיליון	מהדורה	
עריית בת ים	PL-05	01	
אדריכל אחראי		מבנה	
מסטביץ' עומרי		דנה מרמור	
עמוד מידה	מס' עבודה	שרטט	
DA-95011-01	95/011	150	

DATUM Eng Ltd
Engineering Services And Consulting
Tel. 04-6419997 | Fax. 04-6419646 | Kfar Saba 16/990 | P.O.Box. 192
E.Mail: Datum@datum-eng.com