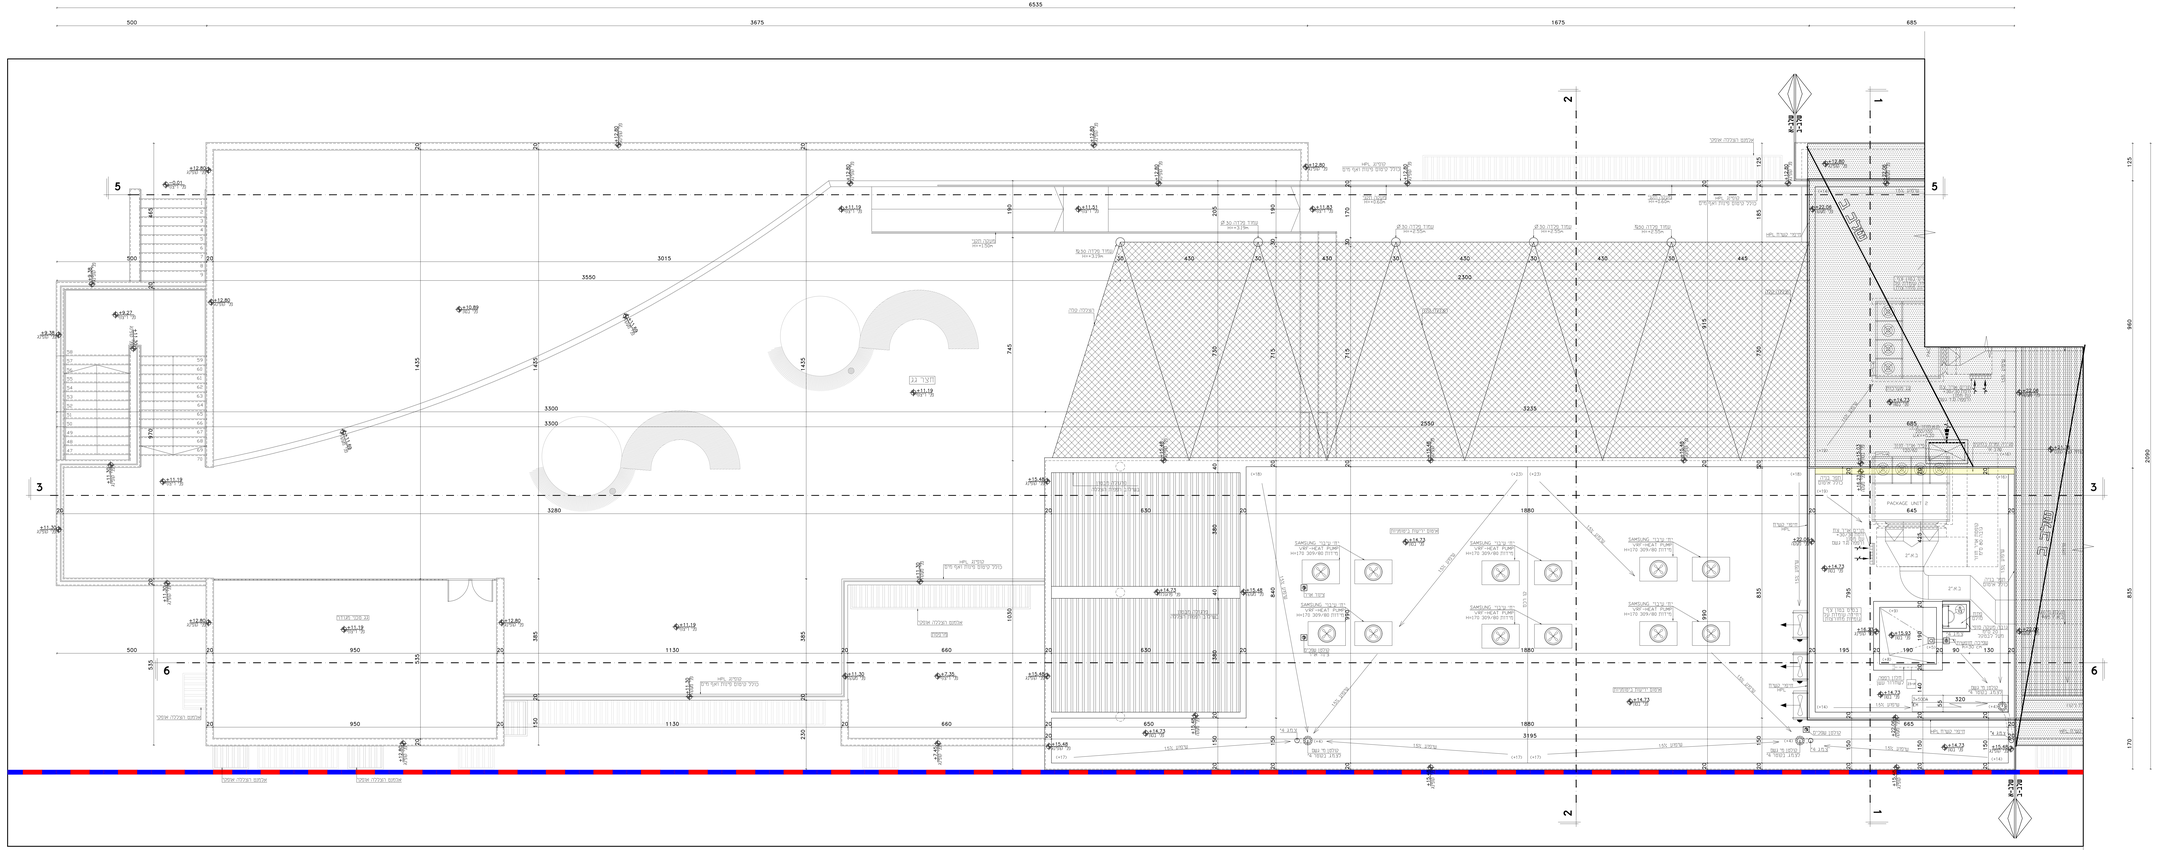

תכנית קומת גג
קנ"מ 1:50

תאריך	תיאור	כמות

תאריך	שרטט	מהדורה

הערות כלליות
- המבנה מתואר לצרכיה הבדיקה המתאמתן בתיקון.
- בכל מקרה של סתירה, עדיפות ביניהם תהיה לפי הנחיה מהנדס.
- אין לבצע מידות ע"פ מדידה מהשרטוט.
- תמרי עמ' האבריאר פרטי יריבוי לאחר אישור המתכנן.
- אין לעשות כל שימוש בתכניות זו אם ברעיונות וגאומים בה ללא אישור בכתב מהמתכנן.
- מבנים ראש יקון אצר מתו ישום מבר עם האדריכל בתכנית זו ושמה לבדו באחריות מלאכותית המתוכת מתכנית.

פרויקט
בית ספר יסודי -24 כיתות
+ אולם ספורט
- מגרש 73 - בת ים

שם
תכנית קומת גג
-מגרש 73

לעיון	לאישור	למכרז 30.09.2024	לביצוע

משרד: עריית בת ים	מס' גליון: PL-06	מהדורה: 01
אדריכל אחראי: סלסבריל עומרי	מנהל: דנה מרמור	
עמוד פרויקט: DA-95011-01	מס' עבודה: 95/011	שרטוט: 150

DATUM Eng Ltd
Engineering Services And Consulting
Tel: 04-6499957 | Fax: 04-6497646 | Kfar Saba 16/990 | P.O.Box: 192
E.Mail: Datum@datum-eng.com