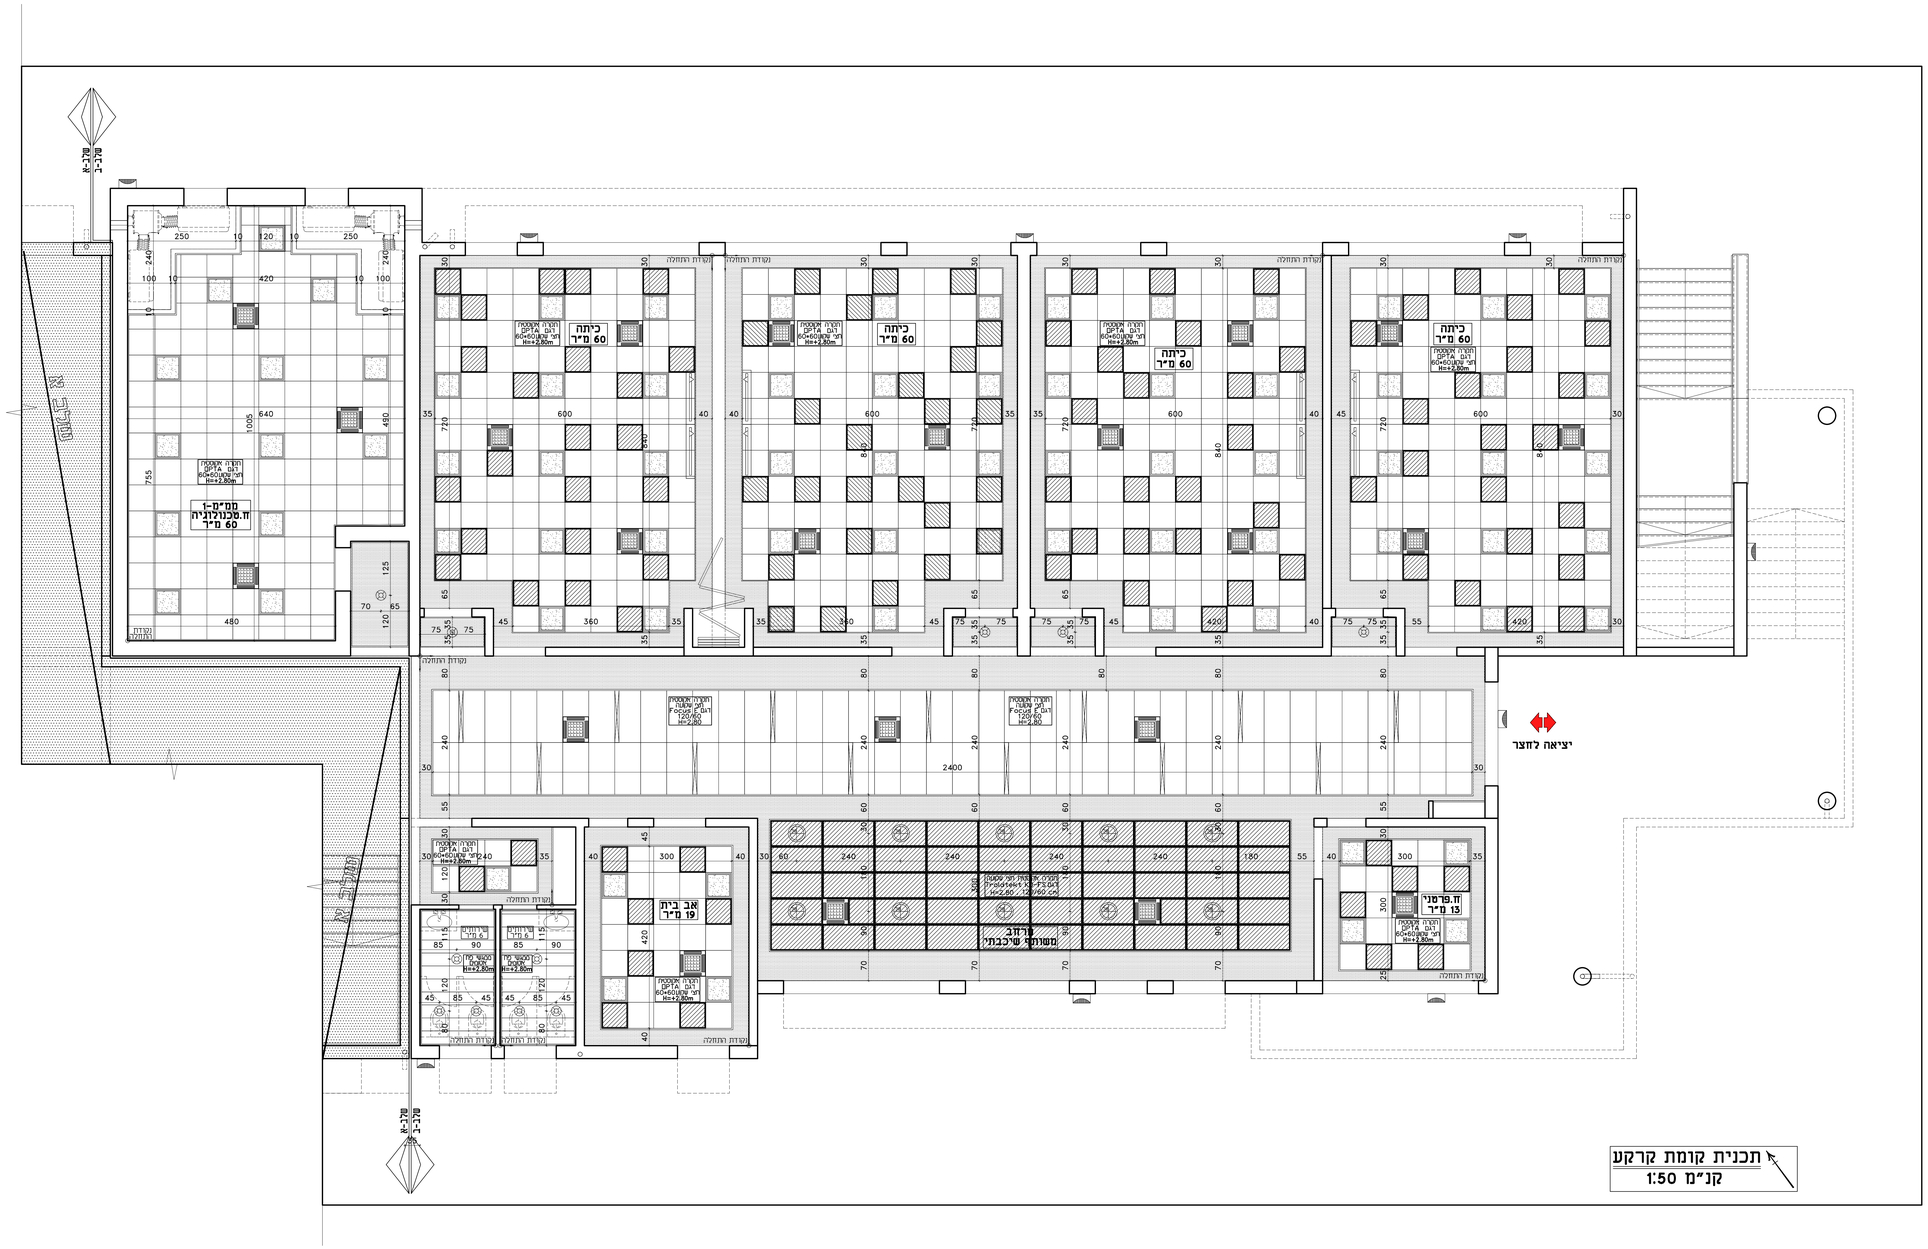

מקרא:

- ג"ת 60/60 משטח לד
- ג"ת עגול שקוע בתקרה דגם סיתום לד תוצרת THORN עם נורת LED 1000LM-4000K
- ג"ת דגם לארא לד תוצרת THORN עם נורת לד 18W גימור בצבע לפי בחירת האדריכל
- ג"ת עגול שקוע בתקרה דגם G-SUVRUC שווקי לירד שטיינץ בגודל שונה לפי בחירת האדריכל 20W-2300Lm-4000°K/3000°K 47W-4800Lm-4000°K/3000°K קוטר 60
- פרופיל תאוקה שקוע
- ג"ת לד 24w להארת לוח כיתה תוצרת 5150046 גגש מקיס
- ג"ת דגם ביקאאס לד שווקי לירד שטיינץ כולל נורת לד 26W
- אלמנט תקרה מרחף דגם SOLO
- תקרת שבבי עץ דגם TROLDTEKT -60*120\60*60 פרופילים ע"ג פרופיל מסוג T24
- תקרה אקוסטית וחצי שקועה דגם Focus E 120/60
- תקרה אקוסטית וחצי שקועה דגם Troldtekt 120/60
- אריחי מינרלי 60/60, חצי שקוע דגם OPTA(רוחבה תקרות אקוסטיות)
- מגשר פח ברוחב 30 מ"מ ללא חירור
- לוחות גבס מוחלק

הערות:
- סימון המפלס מתייחס ל-0.00 של הקומה
- ציון וסימון סוגי התקרות בהתאם לרשימת חומרי הגמר
- באם לא מצוין אחרת, סיגר הגבס במפלס אחיד עם התקרה הסמוכה

תאריך:	תפוצה:	כמות:

תאריך:	שינוים:	מהדורה:

הערות כלליות:
- המובצע אחראי לבדיקת המידות והתאמתן במקום.
- בכל סתירה על סמך מטות או אי התאמה יש לפנות למתכנן.
- אין לבצע מידות עפ מדידה מהשרטוט.
- חוזר נגד נאבריר פרוול יוכבבו לאחר אישור המתכנן
- אין לעשות כל שימוש בתכנית זו אי בהעיונות הגלומים בה ללא אישור בכתב מרמתכנן
- מובדם דאש יוכי אשר עמד רשום מעל שם האדריכל בתכנית זו ונושא בבדד באחריות המקצועית והחוקית לתכנית.

פרויקט:
בית ספר יסודי -24 כיתות
+ אולם ספורט
- מגרש 73 - בת ים

נושא:
תכנית תקרה אקוסטית -שלב ב'
קומת קרקע

לעיון	לאישור	למכרז 30.09.2024	לביצוע

מזמין:	מס' גליון:	מהדורה:
עיריית בת ים	PC-10	01

אדריכל אחראי:	מבקר:
סלסביץ עומרי	דנה מרמור

קנה מידה:	מס' עבודה:	שבע:
1:50	95/011	DA-95011-01

DATUM Eng Ltd
Engineering Services And Consulting
Tel: 04-6419957 | Fax: 04-6411646 | Kfar Kana 16930 | P.O.Box: 132
E.Mail: Datum@datum-eng.com