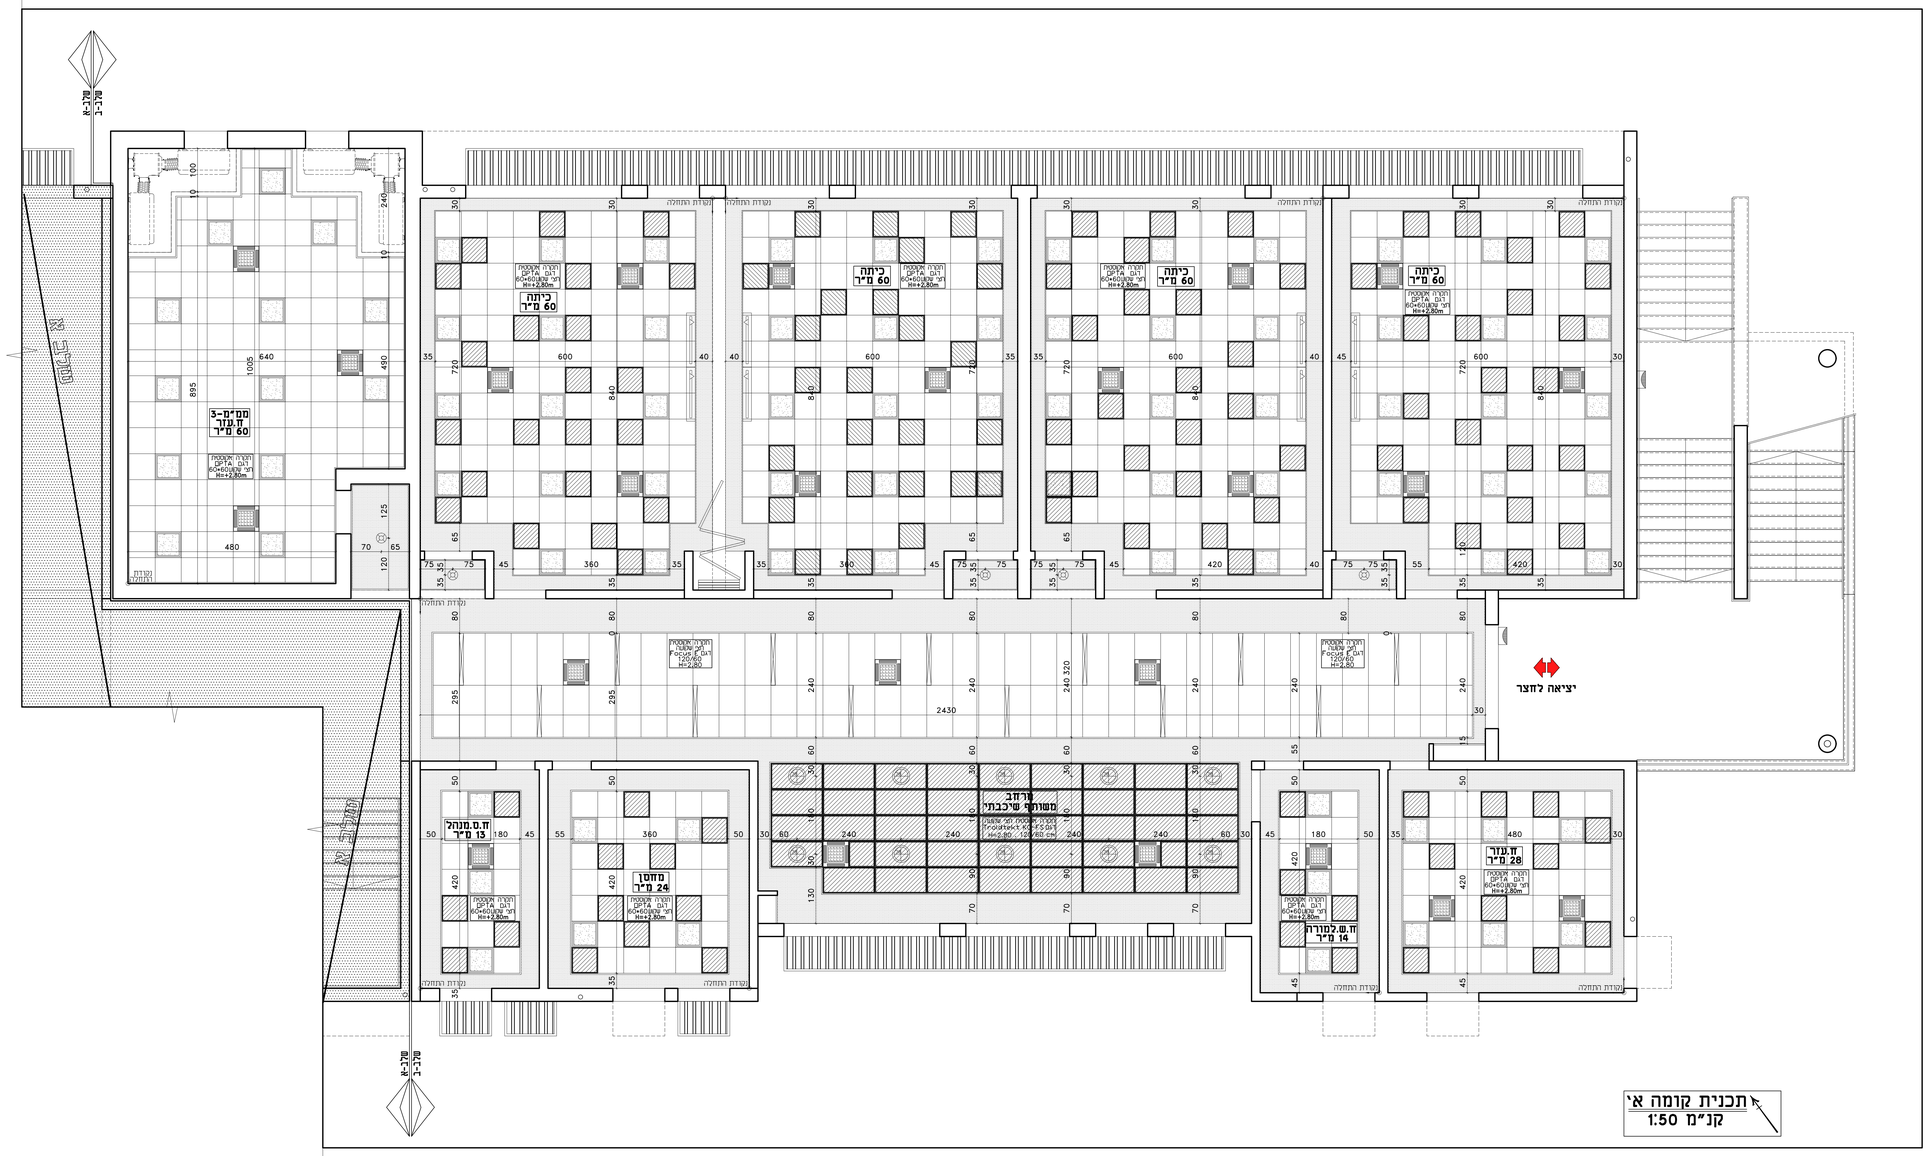

מקרא:

- ג"ת 60/60 משטח לד
- ג"ת נגרר שקוע בתקרה דגם סיתום לד 100LM-4000K LED מוצרת THORN עם נורת
- ג"ת דגם לאר"א לד מוצרת THORN עם נורת לד 18W גימור בצבע לפי בחירת האדריכל
- ג"ת נגרר שקוע בתקרה דגם G-SUVRUC שיווק לירד שסיינץ בגודל שונה לפי בחירת האדריכל
- 20W-2300Lm-4000°K/3000°K 47W-4800Lm-4000°K/3000°K קוסר 60
- פרוייל תאורה שקוע
- ג"ת לד 24W להארת לוח כיתה מוצרת 5150046 גגש מקיס
- ג"ת דגם הריפאק לד שיווק לירד שסיינץ כולל נורת לד 26W
- אלמנט תקרה מרחף דגם SOLO
- תקרת שבבי עץ דגם 60*120\60*60-TROLDTEKT פרופילים ע"ג פרוייל מסוג T24
- תקרה אקוסטית חצי שקועה דגם Focus E 120/60
- תקרה אקוסטית חצי שקועה דגם Troldtekt 120/60
- אריחי מינרלי 60/60, חצי שקוע דגם OPTA(רמה תקרות אקוסטיות)
- מגשר פח ברוחב 30 מ"מ לא חירור
- לוחות גבס מוחלק

הערות:
- קומון המפלס מתייחס ל-0.00 של הקומה
- ציון וסימון סוגי התקרות בתאם לרשימת חומרי הגמר
- באם לא מצוין אחרת, סיגר הגבס במפלס אחיד עם התקרה המסוכה

תאריך:	תפוצה:	כמות:

תאריך:	שינוים:	מהדורה:

הערות כלליות:
- המבנה אתראי לבדיקת המידות והתאמתן במקום.
- בכל מקרה של ספק, סטות או אי התאמה יש לפנות למתכנן.
- אין לבצע מידות עיפ מדידה מרשרטוט.
- חומר גמר ואביזרי פרוזל יוכבו לאחר אישור המתכנן.
- אין לעשות כל שימוש בתכנית זו אי ברעיונות וגבולים בה ללא אישור בכתב מהמתכנן.
- מדגדם ראו יועץ אשר שמו רשום מעל שם האדריכל בתכנית זו ונשא לבדו באחראיות המקצועית והחוקית לתכנית.

פרויקט:
בית ספר יסודי -24 כיתות
+ אולם ספורט
- מגרש 73 - בת ים

נושא:
תכנית תקרה אקוסטית -עליב ב'
קומה א'

לעיון	לאישור	למכרז 30.09.2024	לביצוע

מזמין: עיריית בת ים	מס' גליון: PC-11	מהדורה: 01
אדריכל אחראי: טלסביגי עומרי	מבצע: דנה מרמור	
קנה מידה: 150	מס' עבודה: 95/011	שובץ: DA-95011-01

DATUM Eng Ltd
Engineering Services And Consulting
Tel: 04-6419957 | Fax: 04-6411646 | Kfar Kana 16930 | P.O.Box: 132
E.Mail: Datum@datum-eng.com