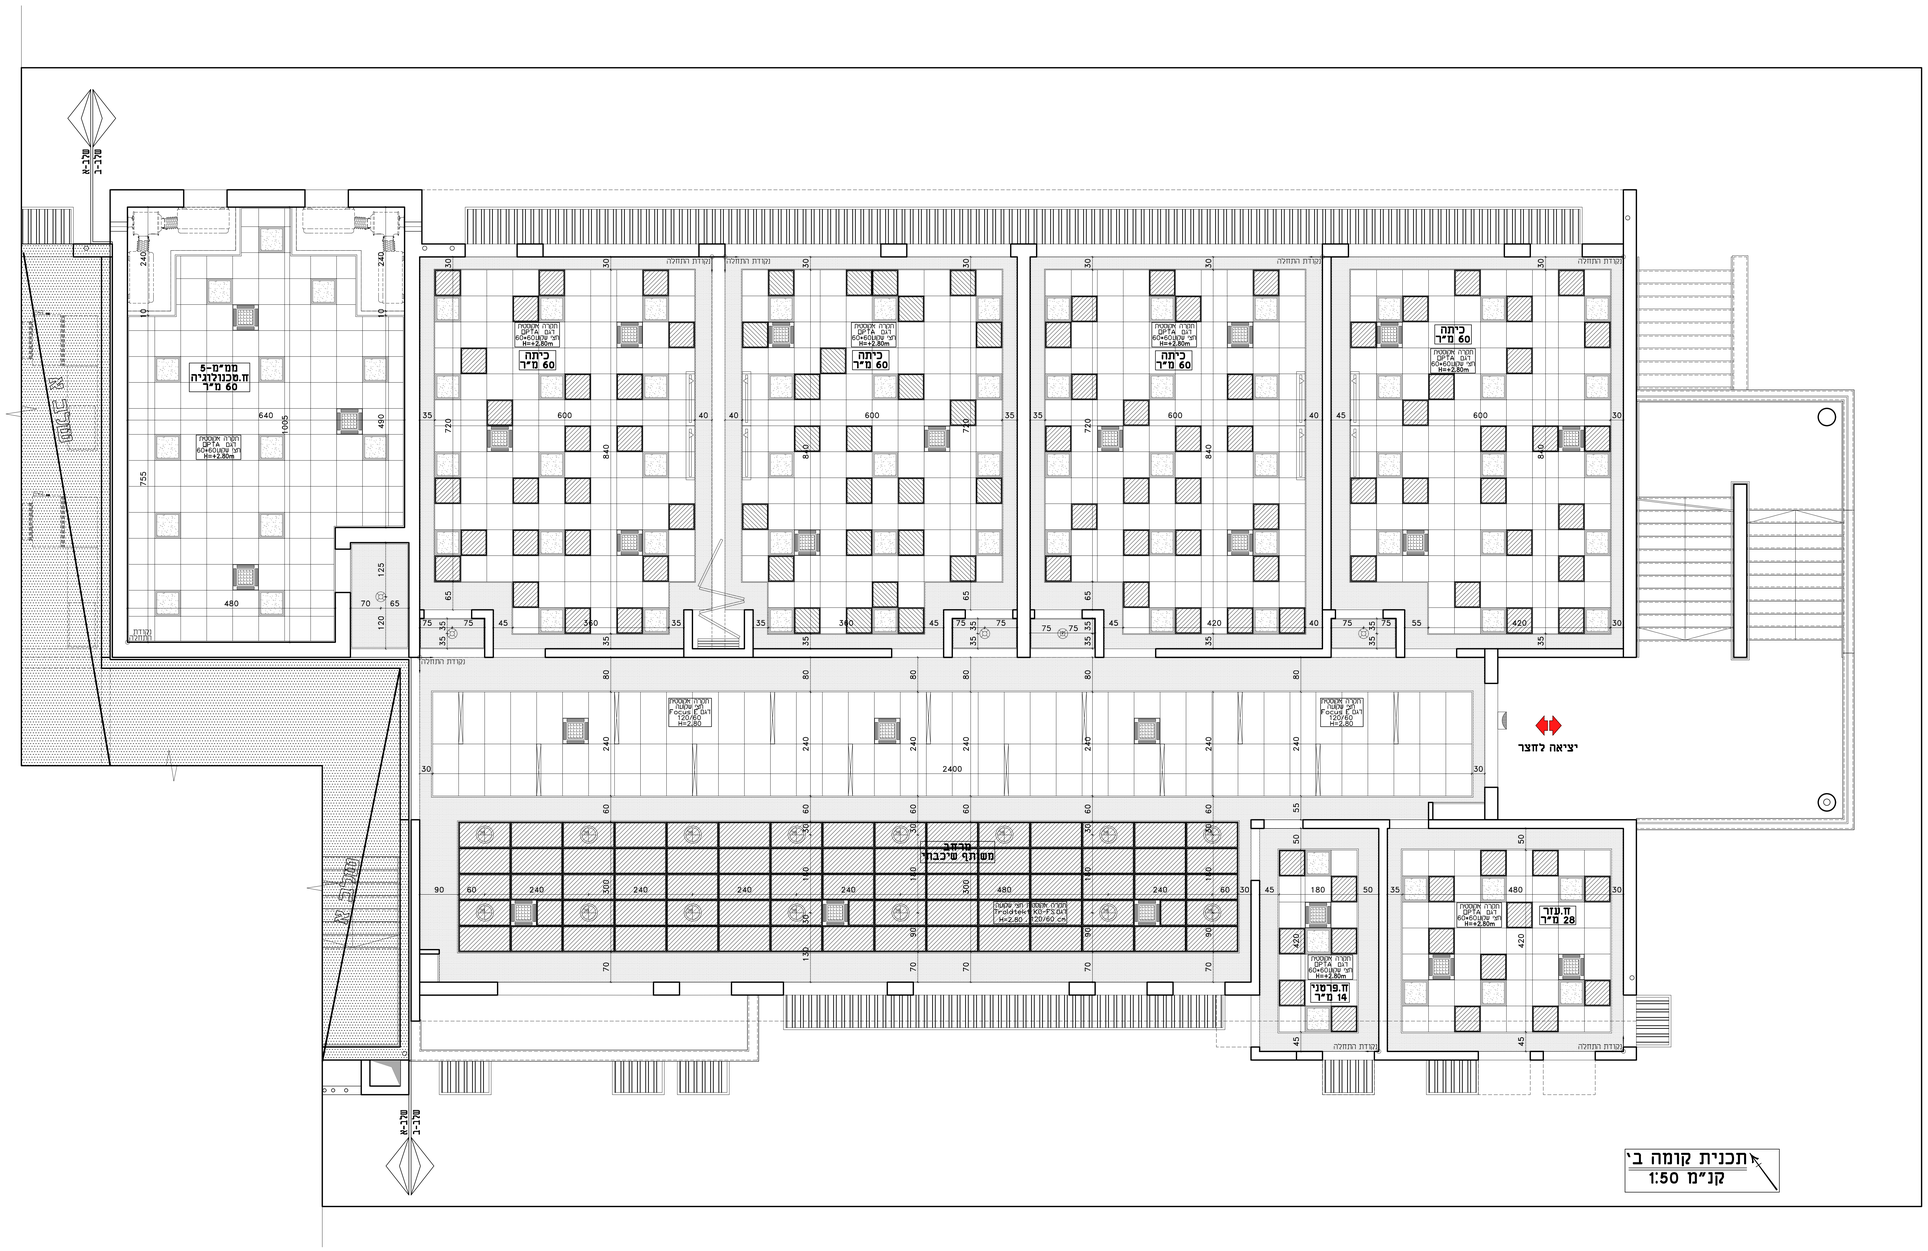

מקרא:

- גיית 60/60 משטח לד
- גיית ענוך שקוע בתקרה דגם סיתום לד תוצרת THORN עם נורת LED 1000LM–4000K
- גיית דגם לאורא לד תוצרת THORN עם נורת לד 18W גימור בצבע לפי בחירת האדריכל
- גיית ענוך שקוע בתקרה דגם G-SUVRUC שווק לירד שטיינץ בגודל שונה לפי בחירת האדריכל 20W-2300Lm-4000°K/3000°K 47W-4800Lm-4000°K/3000°K קוטר 60
- פרופיל תאוקה שקוע
- גיית לד 24W להארת לוח כיתה תוצרת גגוש מקיט 5150046
- גיית דגם הריקאאן לד שווק לירד שטיינץ כולל נורת לד 26W
- אלמנט תקרה מרחף דגם SOLO
- תקרת שבבי עץ דגם TROLDTEKT–60*120\60*60 פרופילים ע"ג פרופיל מסוג T24
- תקרה אקוסטית חצי שקועה דגם Focus E 120/60
- תקרה אקוסטית חצי שקועה דגם Troldtekt 120/60
- אריחי מינרלי 60/60, חצי שקוע דגם OPTA(רצועה תקרות אקוסטיות)
- מגשי פח ברוחב 30 מ"מ ללא חירור
- לוחות גבס מוחלק

הערות:
- מימון המפלס מתייחס ל-0.00 של הקומה.
- ציון וסימון סוגי התקרות בהתאם לרשימת חומרי הגמר
- באם לא מצוין אחרת, סיגר דג.ב.ס במפלס אחיד עם התקרה הסמוכה

תאריך:	תמציה:	כמות:

תאריך:	שרטט:	מהדורה:

הערות כלליות:
- המבצע אחראי לבדיקת המידות והתאמתן במקום.
- בכל מקרה על סמך מצוות אי אי התאמה יש לפנות למתכנן.
- אין לבצע מידות ע"פ מדידה מהשרטוט
- חומר גמר וארגוני פרוזל יוכבו לאחר אישור המתכנן
- אין לעשות כל שינוי בתוכנית זו אי ברעיונות וגבולים בה ללא אישור בכתב מהמתכנן
- מהנדס רואי יוצץ אשר שמו רשום מעל שם האדריכל בתכנית זו נושא לבדו באחריות המקצועית והחוזקית בתכנית

פרויקט:
בית ספר יסודי -24 כיתות
+ אולם ספורט
- מגרש 73 - בת ים

נושא:
תכנית תקרה אקוסטית -טליב ב'
קומה ב'

לעיון	לאישור	למכרז	לביצוע
		30.09.2024	

מזמין: עיריית בת ים	מס' גליון: PC-12	מהדורה: 01
אדריכל אחראי: סלסביל עומרי	מבצע: דנה מרמור	
קנה מידה: 1:50	מס' עבודה: 95/011	שבע: DA-95011-01

DATUM Eng Ltd
Engineering Services And Consulting
Tel. 04-6419957 | Fax: 04-6411646 | Kfar Kana 16930 | P.O.Box: 132
E.Mail: Datum@datum-eng.com