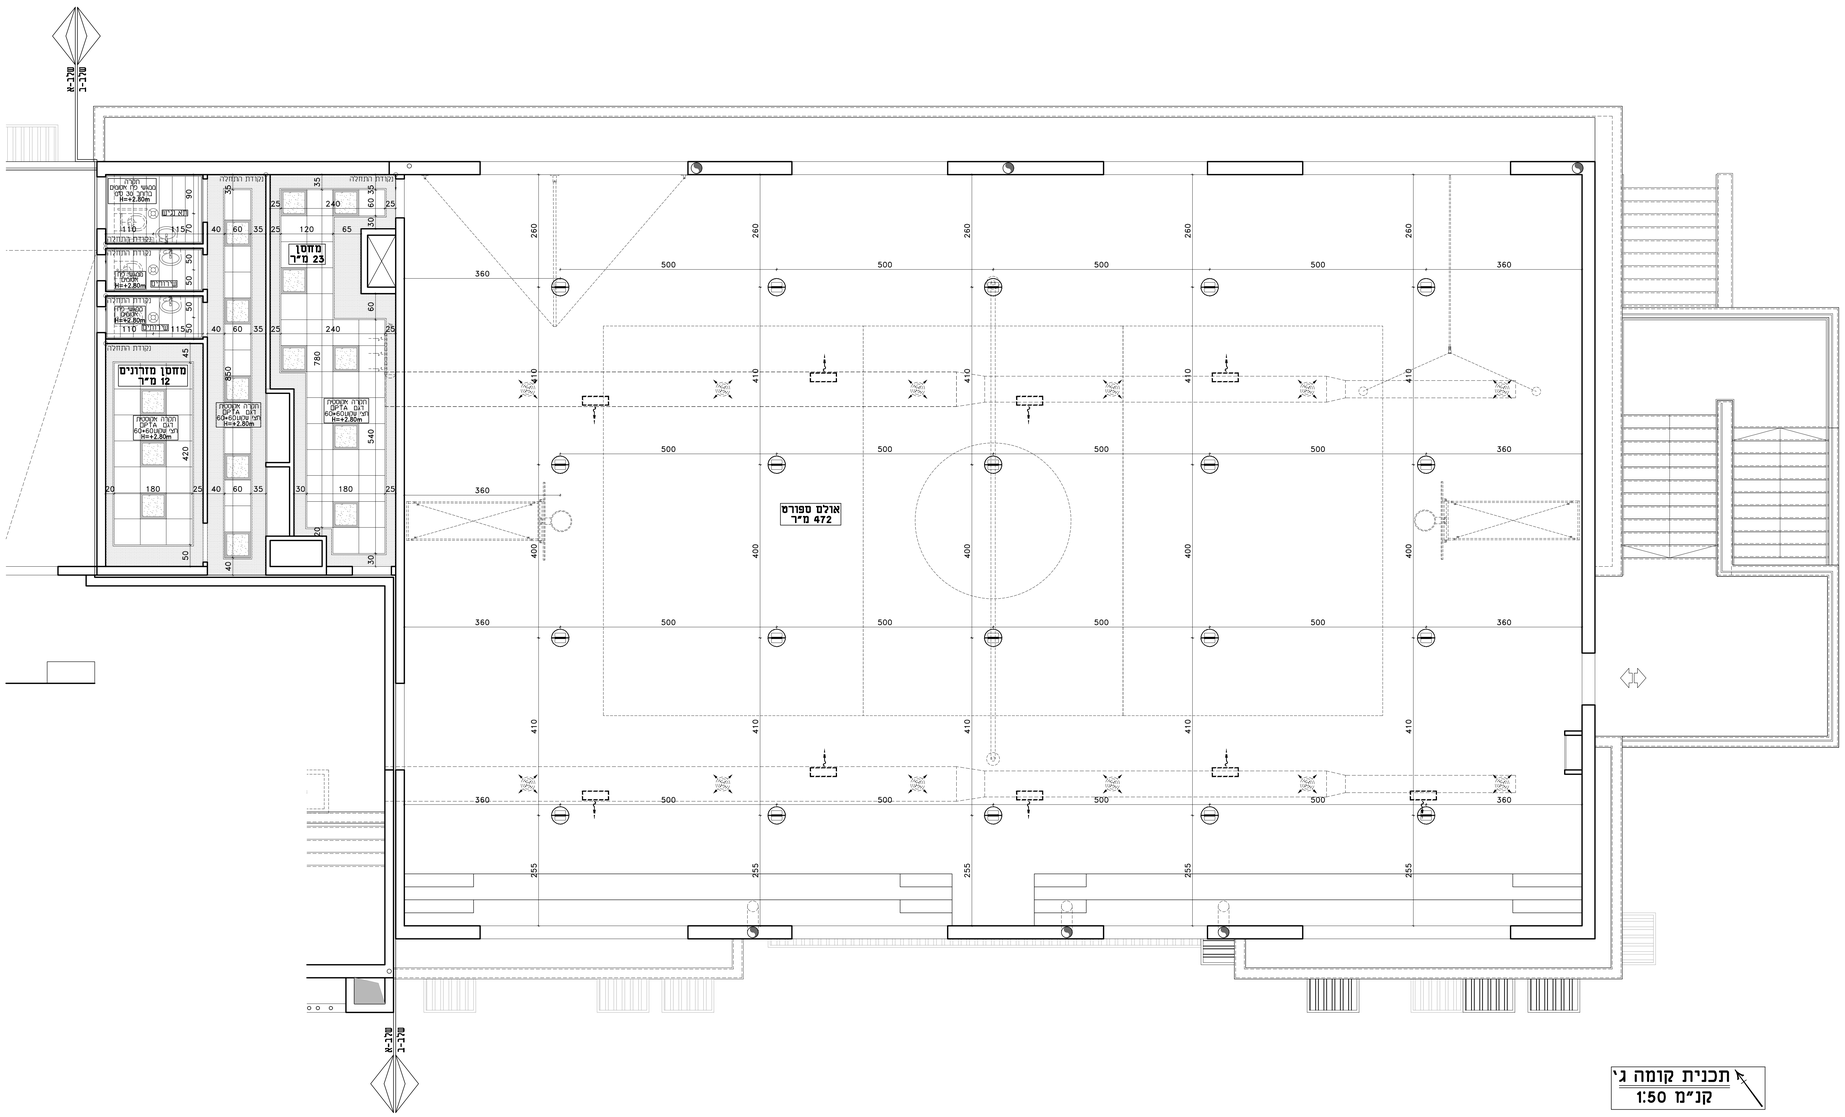

מקרא:

- גיץ 60/60 משטח לד
- גיץ עגול שקוע בתקרה דגם סיתום לד 1000LM-4000K תוצרת THORN עם נורת LED
- גיץ דגם הייפאק לד שיווק לירד שטיניץ כולל נורת לד 26W
- גיץ לד תלוי מתתקרה דגם HI CLOUD-L תוצרת לירד שטיניץ עם נורת לד 200W 4000K-24250LM מתאים לגבהים 6-8 מטר (40)
- תקרה אקוסטית חצי שקועה דגם Traditek 120/60
- אריחי מינרלי 60/60, חצי שקוע דגם OPTA(לרבות תקרות אקוסטיות)
- מגשר פח ברוחב 30 ס"מ ללא חירור
- לוחות גבס מוחלק

הערות:
- סימון המפלס מתייחס ל-0.00 של הקומה
- צירן וסימון סוגי התקרות בהתאם לרשרטת חומרי הגמר
- באם לא מצוין אחרת, סיגר הגבס במפלס אחיד עם התקרה הסמוכה

תאריך:	תמצה:	כמות:

תאריך:	שינוים:	מהדורה:

הערות כלליות:
- המבצע אחראי לבדיקת המידות והתאמתן במקום.
- בכל מקרה של סתירה, טעות או אי התאמה יש לפנות למתכנן.
- אין לבצע מידות עיפ מדידה מהשרטוט.
- חומרי גמר ואביזרי פרוזל ירכבו לאחר אישור המתכנן.
- אין לעשות כל שימוש בתכנית זו אי ברעיונות הגלומים בה ללא אישור בכתב מהמתכנן.
- מהנדס ו/או יועץ אשר שמו רשום מעל שם האדריכל בתכנית זו נושא לבדו באחריות המקצועית והחוקתית לתכנית.

פרויקט:
בית ספר יסודי -24 כיתות + אולם ספורט - מגרש 73 - בת ים

נושא
תכנית תקרה אקוסטית -עטלב ב' קומה ג'

לעיון	לאישור	למכרז 30.09.2024	לביצוע

מזמין: עיריית בת ים	מס' גליון: PC-13	מהדורה: 01
אדריכל אחראי: טלסביל עומרי	מתכנן: דנה מרמור	
קנה מידה: 1:50	מס' עבודה: 95/011	קובץ: DA-95011-01

DATUM Eng Ltd
Engineering Services And Consulting
Tel: 04-6419957 | Fax: 04-6411646 | Kfar Kana 16930 | P.O.Box: 132
E.Mail: Datum@datum-eng.com