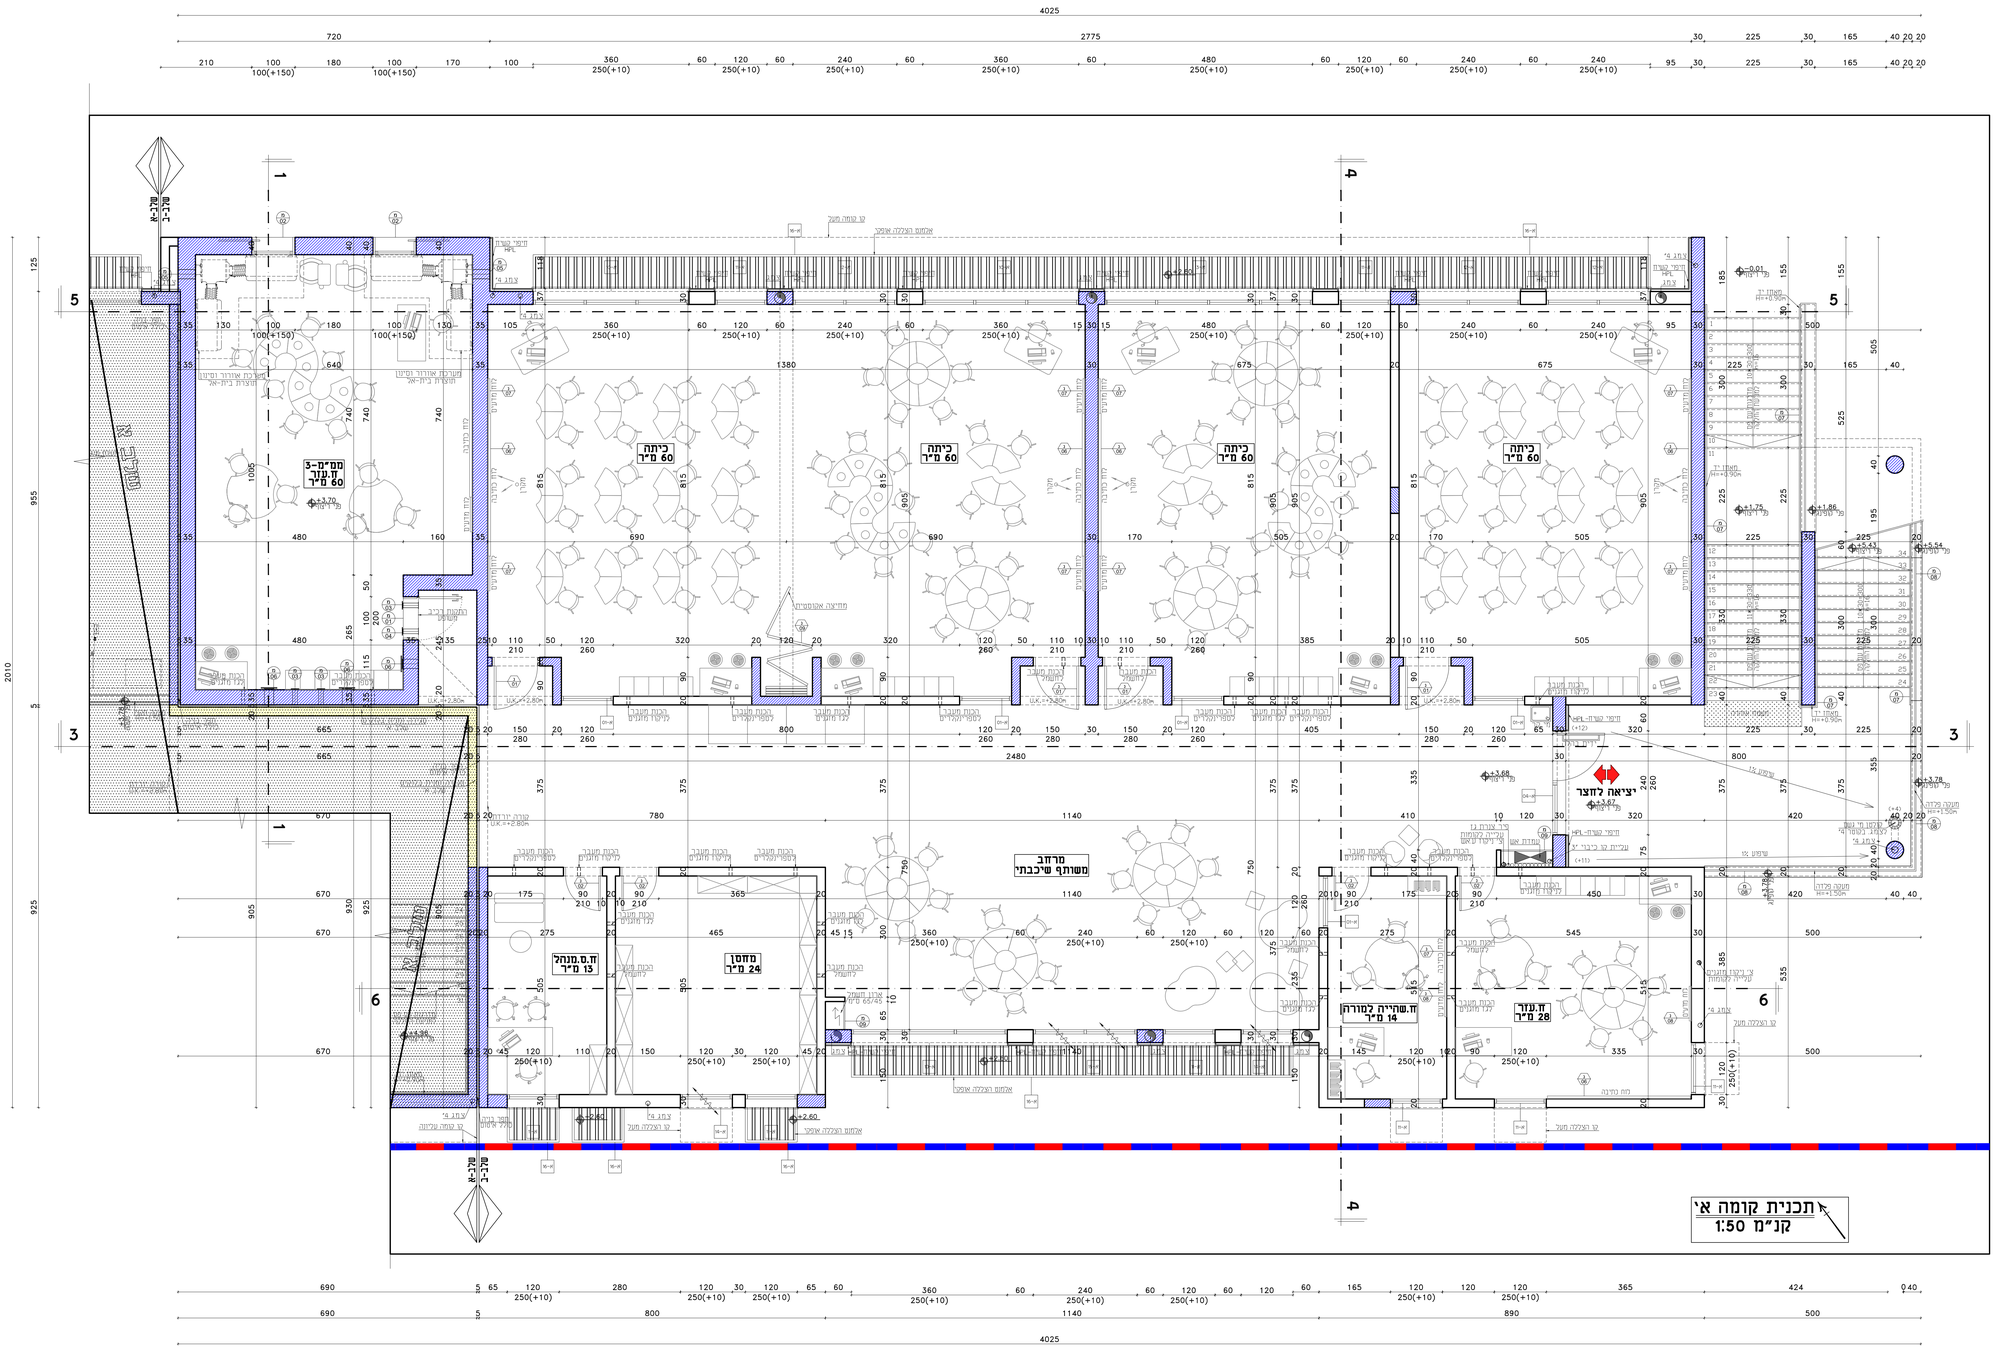

תאריך:	תפוצה:	כמות:

תאריך:	שינוים:	מהדורה:

הגדרת כללית:
- המבצע אחראי לבדיקת המידות והתאמתן במקום.
- בכל מקרה של ספק, טעות או אי התאמה יש לפנות למתכנן.
- אין לבצע מידות עפ"י מדידה מהשרטוט.
- חומרי גמר ואביזרי מרזוב יוזכבו לאחר אישור המתכנן.
- אין לעשות כל שימוש בתכנית זו אי ברעיונות הגלומים בה ללא אישור בכתב מהמתכנן.
- מדמדים ושאר יונקי אשר שמו רשום מעבר שם האדריכל בתכנית זו נושא לבדוק באחריאות המקצועית והחוקית לתכנית.

פרויקט:
בית ספר יסודי -24 כיתות
+ אולם ספורט
- מגרש 73 - בת ים

נושא:
תכנית קומה א'
-טלב ב'

לעיון	לאישור	למכרז 30.09.2024	לביצוע

חומר:	מס' גליון:	מהדורה:
עיריית בת ים	PL-02	01

אדריכל אחראי:	מבנה:
סלסביל עומרי	דנה מרמור

קנה מידה:	מס' עבודה:	שבע:
1:50	95/011	DA-95011-01

DATUM Eng Ltd
Engineering Services And Consulting
Tel: 04-6419957 | Fax: 04-6416646 | Kfar Kana 16930 | P.O.Box: 192
E.Mail: Datum@datum-eng.com