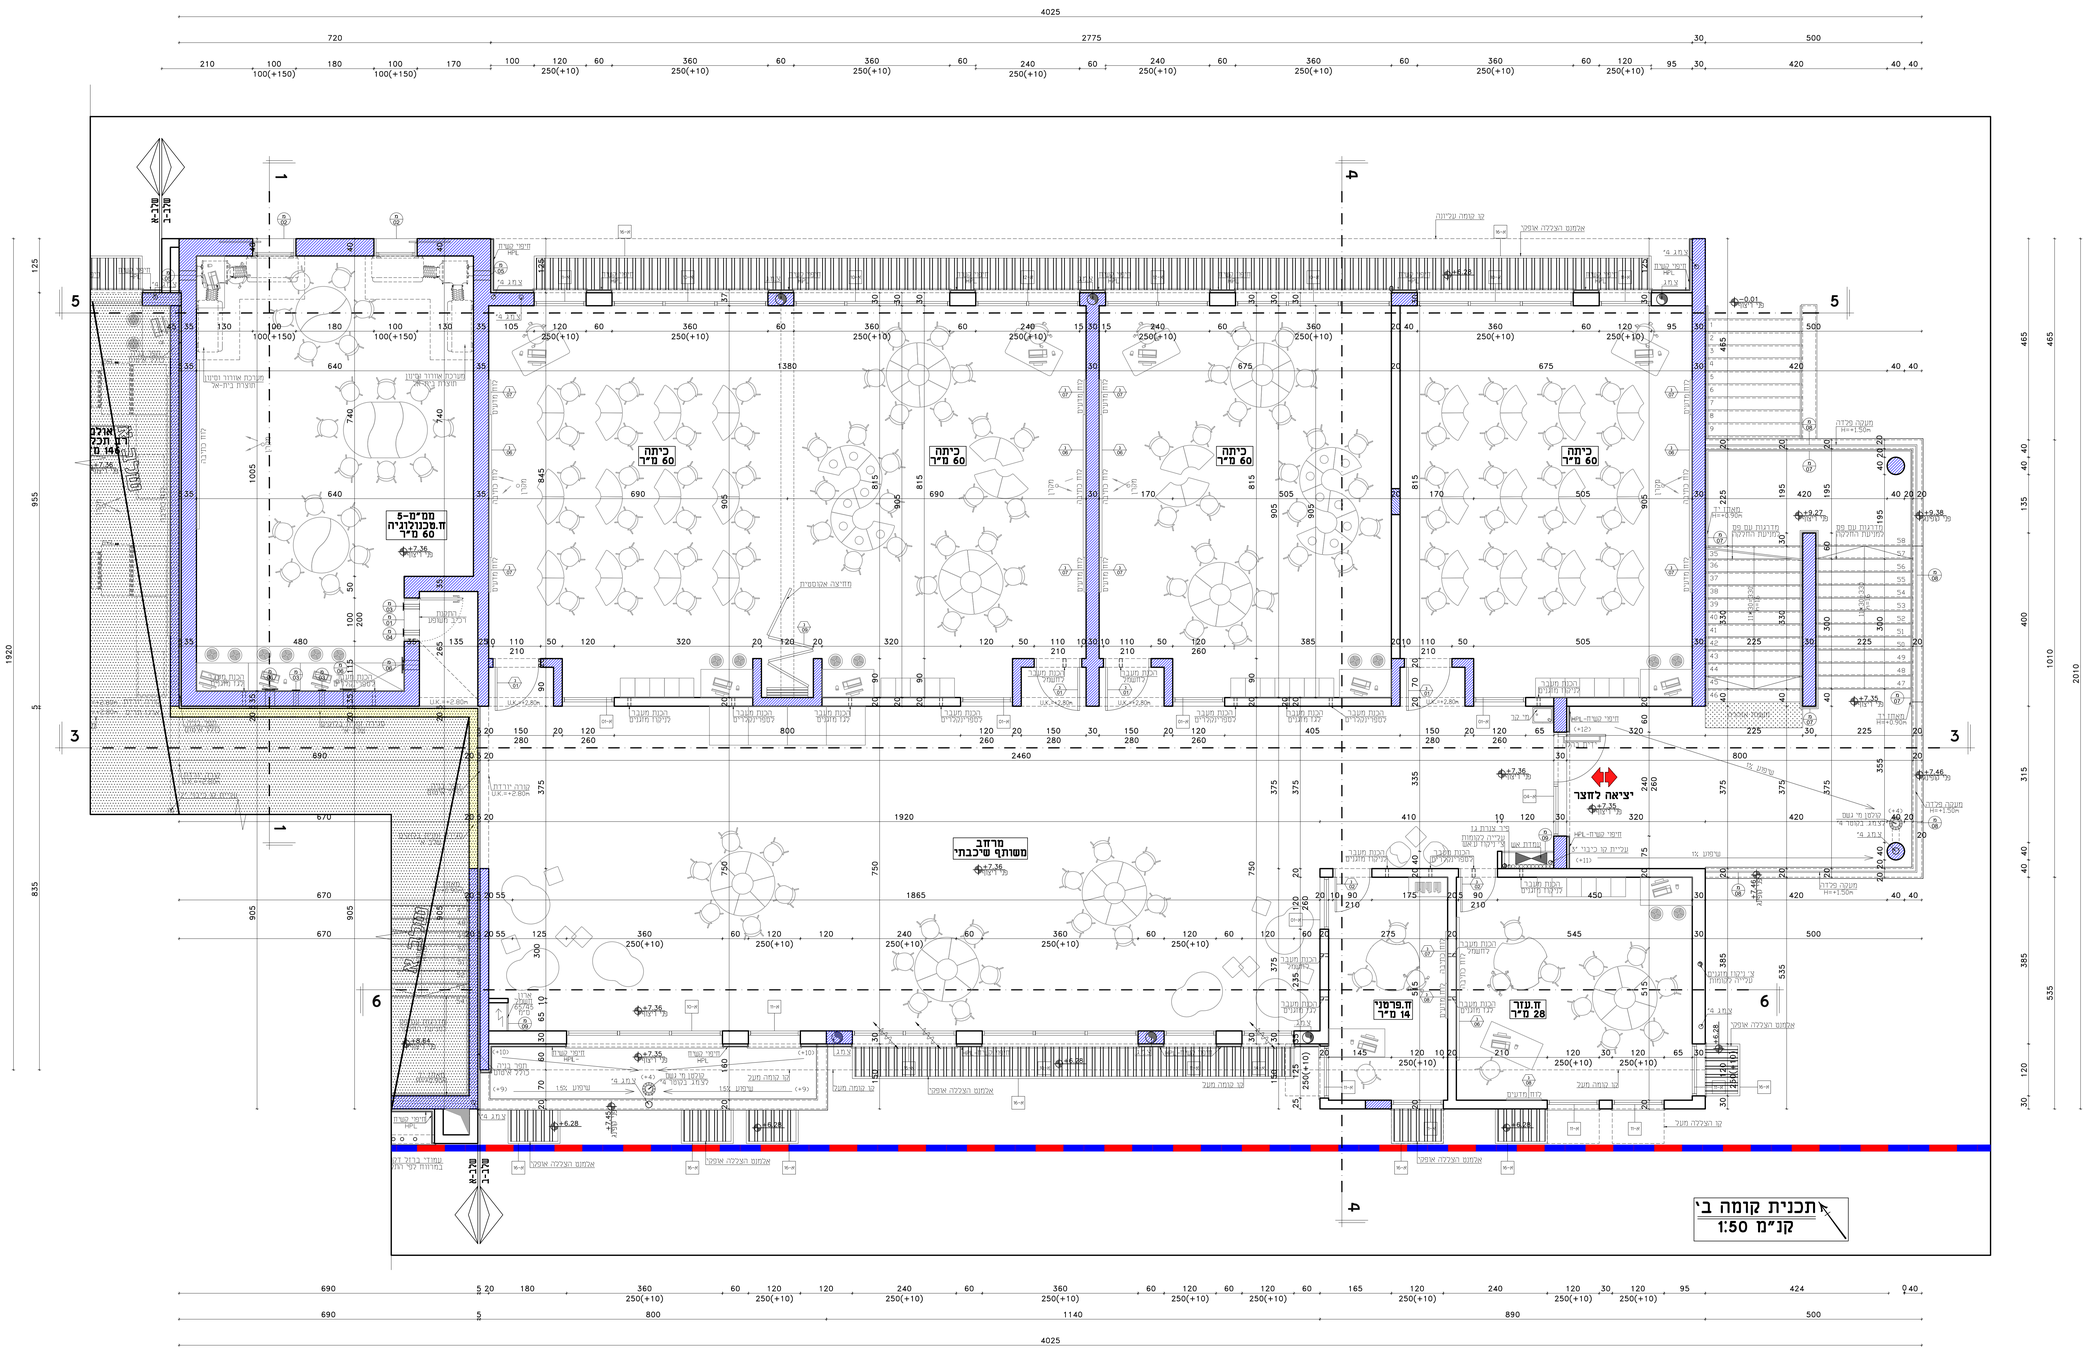

תאריך:	תוצאה:	כמות:

תאריך:	שינוי:	מהדורה:

הערות כלליות:
- המבצע אחראי לבדיקת המידות והתאמתן במקום.
- בכל מקרה של סתירה, מעוות או אי התאמה יש לפנות למתכנן.
- אין לבצע מידות עפ"י מדידה מהשרטוט.
- מומרי גמר ואביזרי פרזול יוזכרו לאחר אישור המתכנן.
- אין לעשות כל שינוי בתכנית זו אם ובינתוים הגבוהים בה ללא אישור בכתב מהמתכנן.
- מהנדס ראש יזעץ אשר שמו רשום מעל שם האדריכל בתכנית זו נושא לבדו באחריותו המקצועית והחוקית לתכנית.

פרויקט:
בית ספר יסודי -24 כיתות
+ אולם ספורט
- מגרש 73 - בת ים

נושא:
תכנית קומה ב'
-טלב ב'

לעיון	לאישור	למכרז 30.09.2024	לביצוע

מתמיך: עיריית בת ים	מס' גליון: PL-03	מהדורה: 01
אדריכל אחראי: סלסביל עומרי	מבצר: דנה מרמור	
קנה מידה: 1:50	מס' עבודה: 95/011	שבע: DA-95011-01

DATUM Eng Ltd
Engineering Services And Consulting
Tel: 04-6419957 | Fax: 04-6411646 | Kfar Kana 16930 | P.O.Box: 132
E.Mail: Datum@datum-eng.com