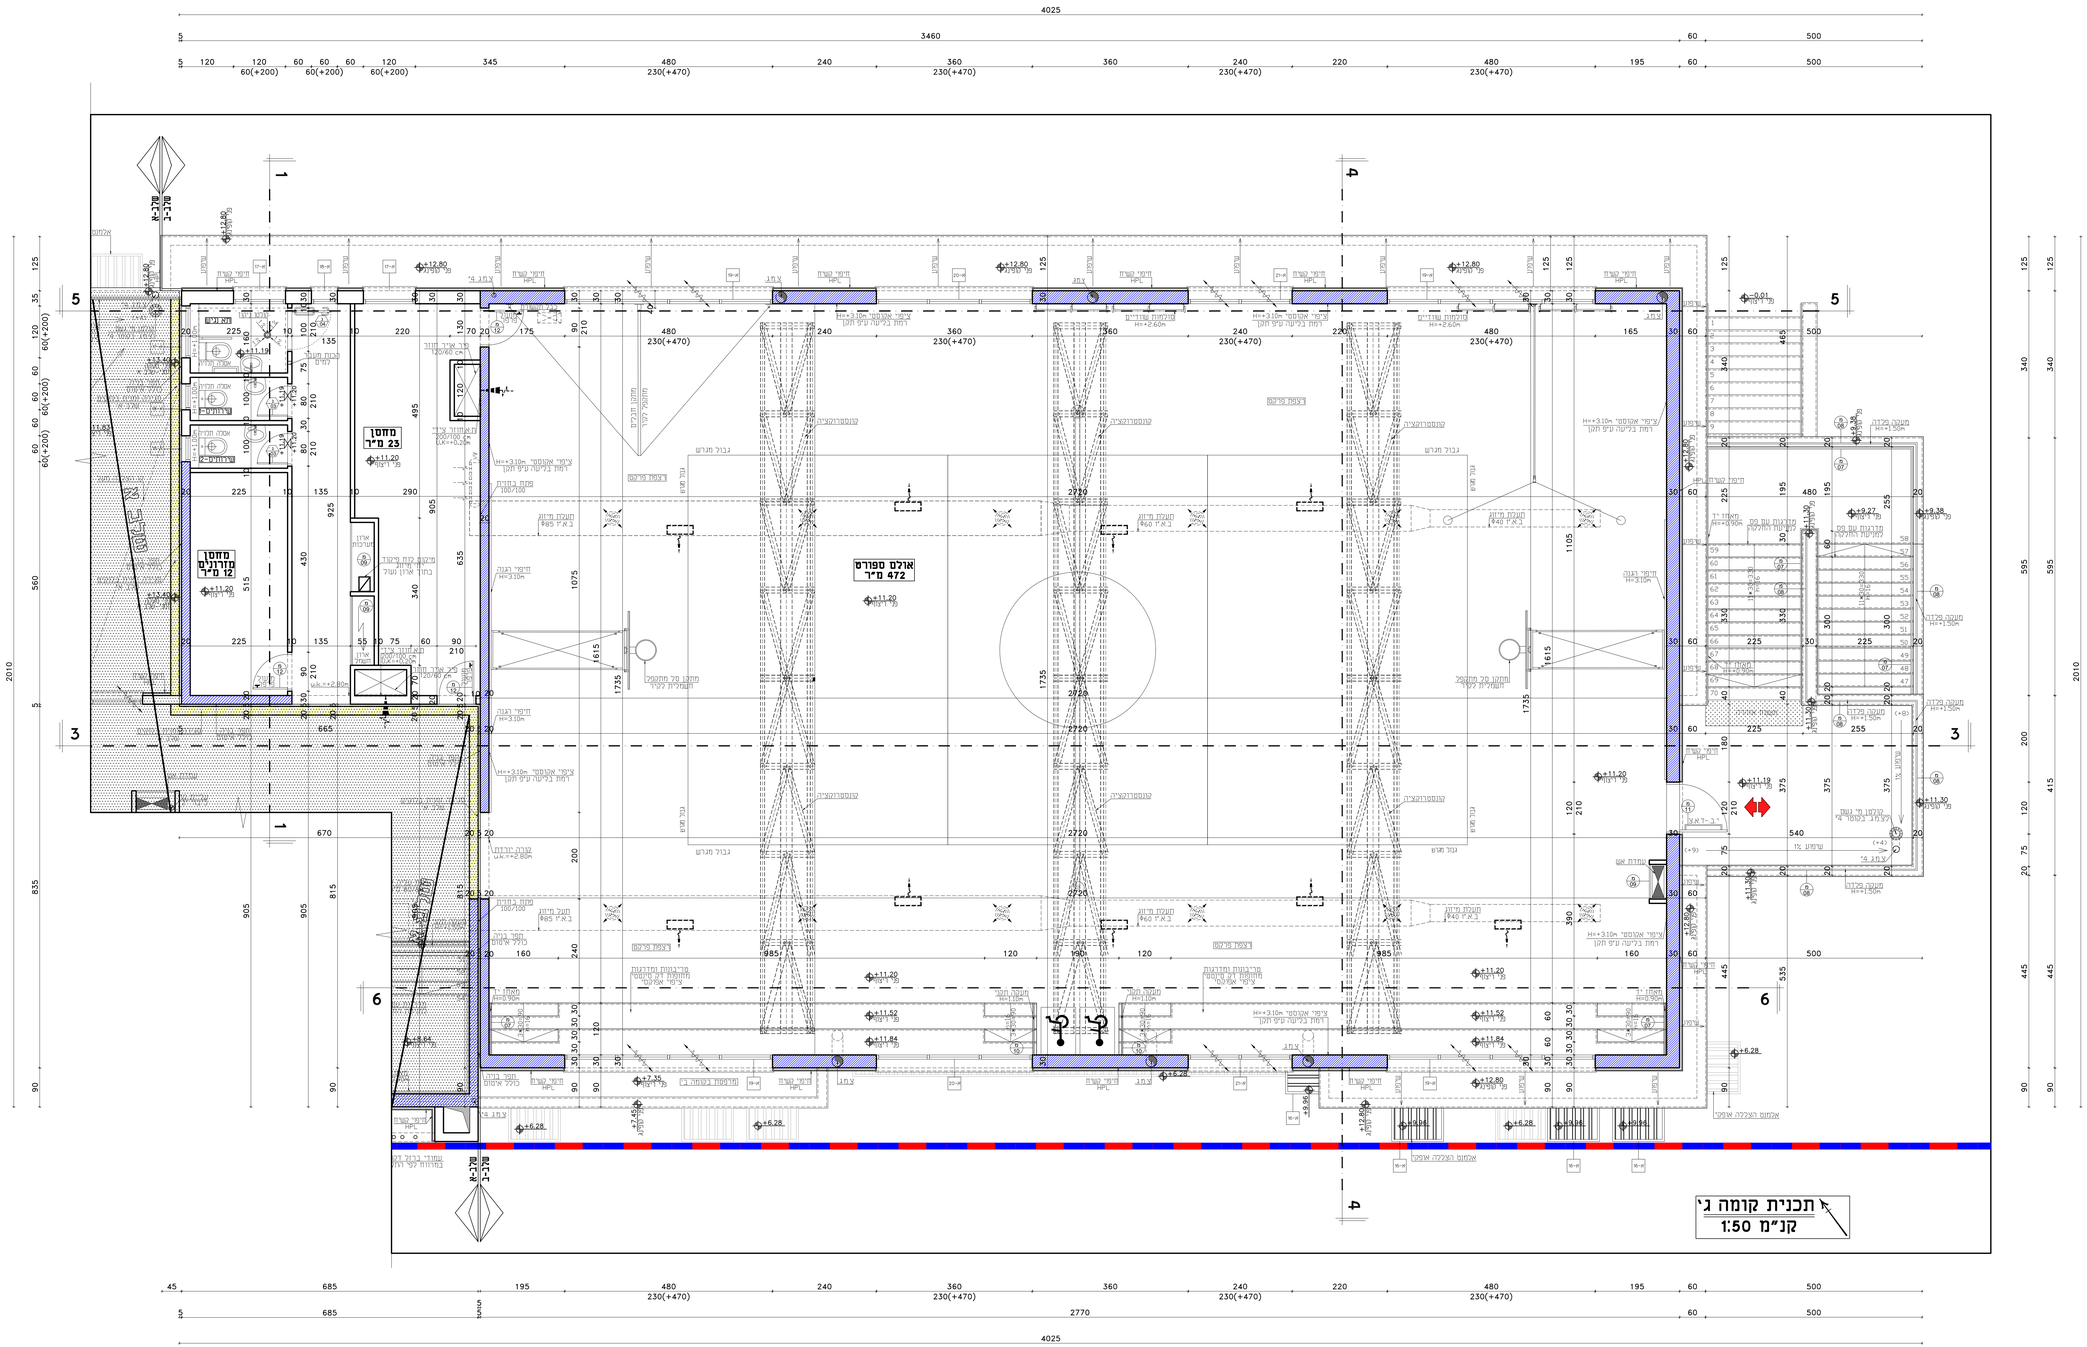

תאריך: | תמצה: | כמות:

תאריך: | שינוים: | מהדורה:

הערות כלליות:
- המבנא אחראי לבדיקת המידות והתאמתן במקום.
- בכל מקרה של ספק, סטות או אי התאמה- יש לפנות למתכנן.
- אין לבצע מידות ע"פ חדידה מהשרטוט.
- מומלץ גמד ואביזרי פרוזל יורכבו לאחר אישור המתכנן
- אין רעשות כל שינוים בתכנית זו אי ברטיוות הבלוחים בה ללא אישור בכתב מהמתכנן
- מהבנים ראש יזנין אשר שמו רשום מעל שם האדריכל בתכנית זו ונעא לבדו באחריאיות המקצועית והחוזקית לתכנית.

פרויקט:
בית ספר יסודי -24 כיתות
+ אולם ספורט
- מגרש 73 - בת ים

נושא:
תכנית קומה ג'
-טלב ב'

לעיון	לאישור	למכרז 30.09.2024	לביצוע

מזמין: עיריית בת ים	מס' גליון: PL-04	מהדורה: 01
אדריכל אחראי: סלסביל עומרי	מבצר: דנה מרמור	
קנה מידה: 1:50	מס' עבודה: 95/011	שבע: DA-95011-01

DATUM Eng Ltd
Engineering Services And Consulting
Tel: 04-6419957 | Fax: 04-6411646 | Kfar Kana 16930 | P.O.Box: 132
E.Mail: Datum@datum-eng.com