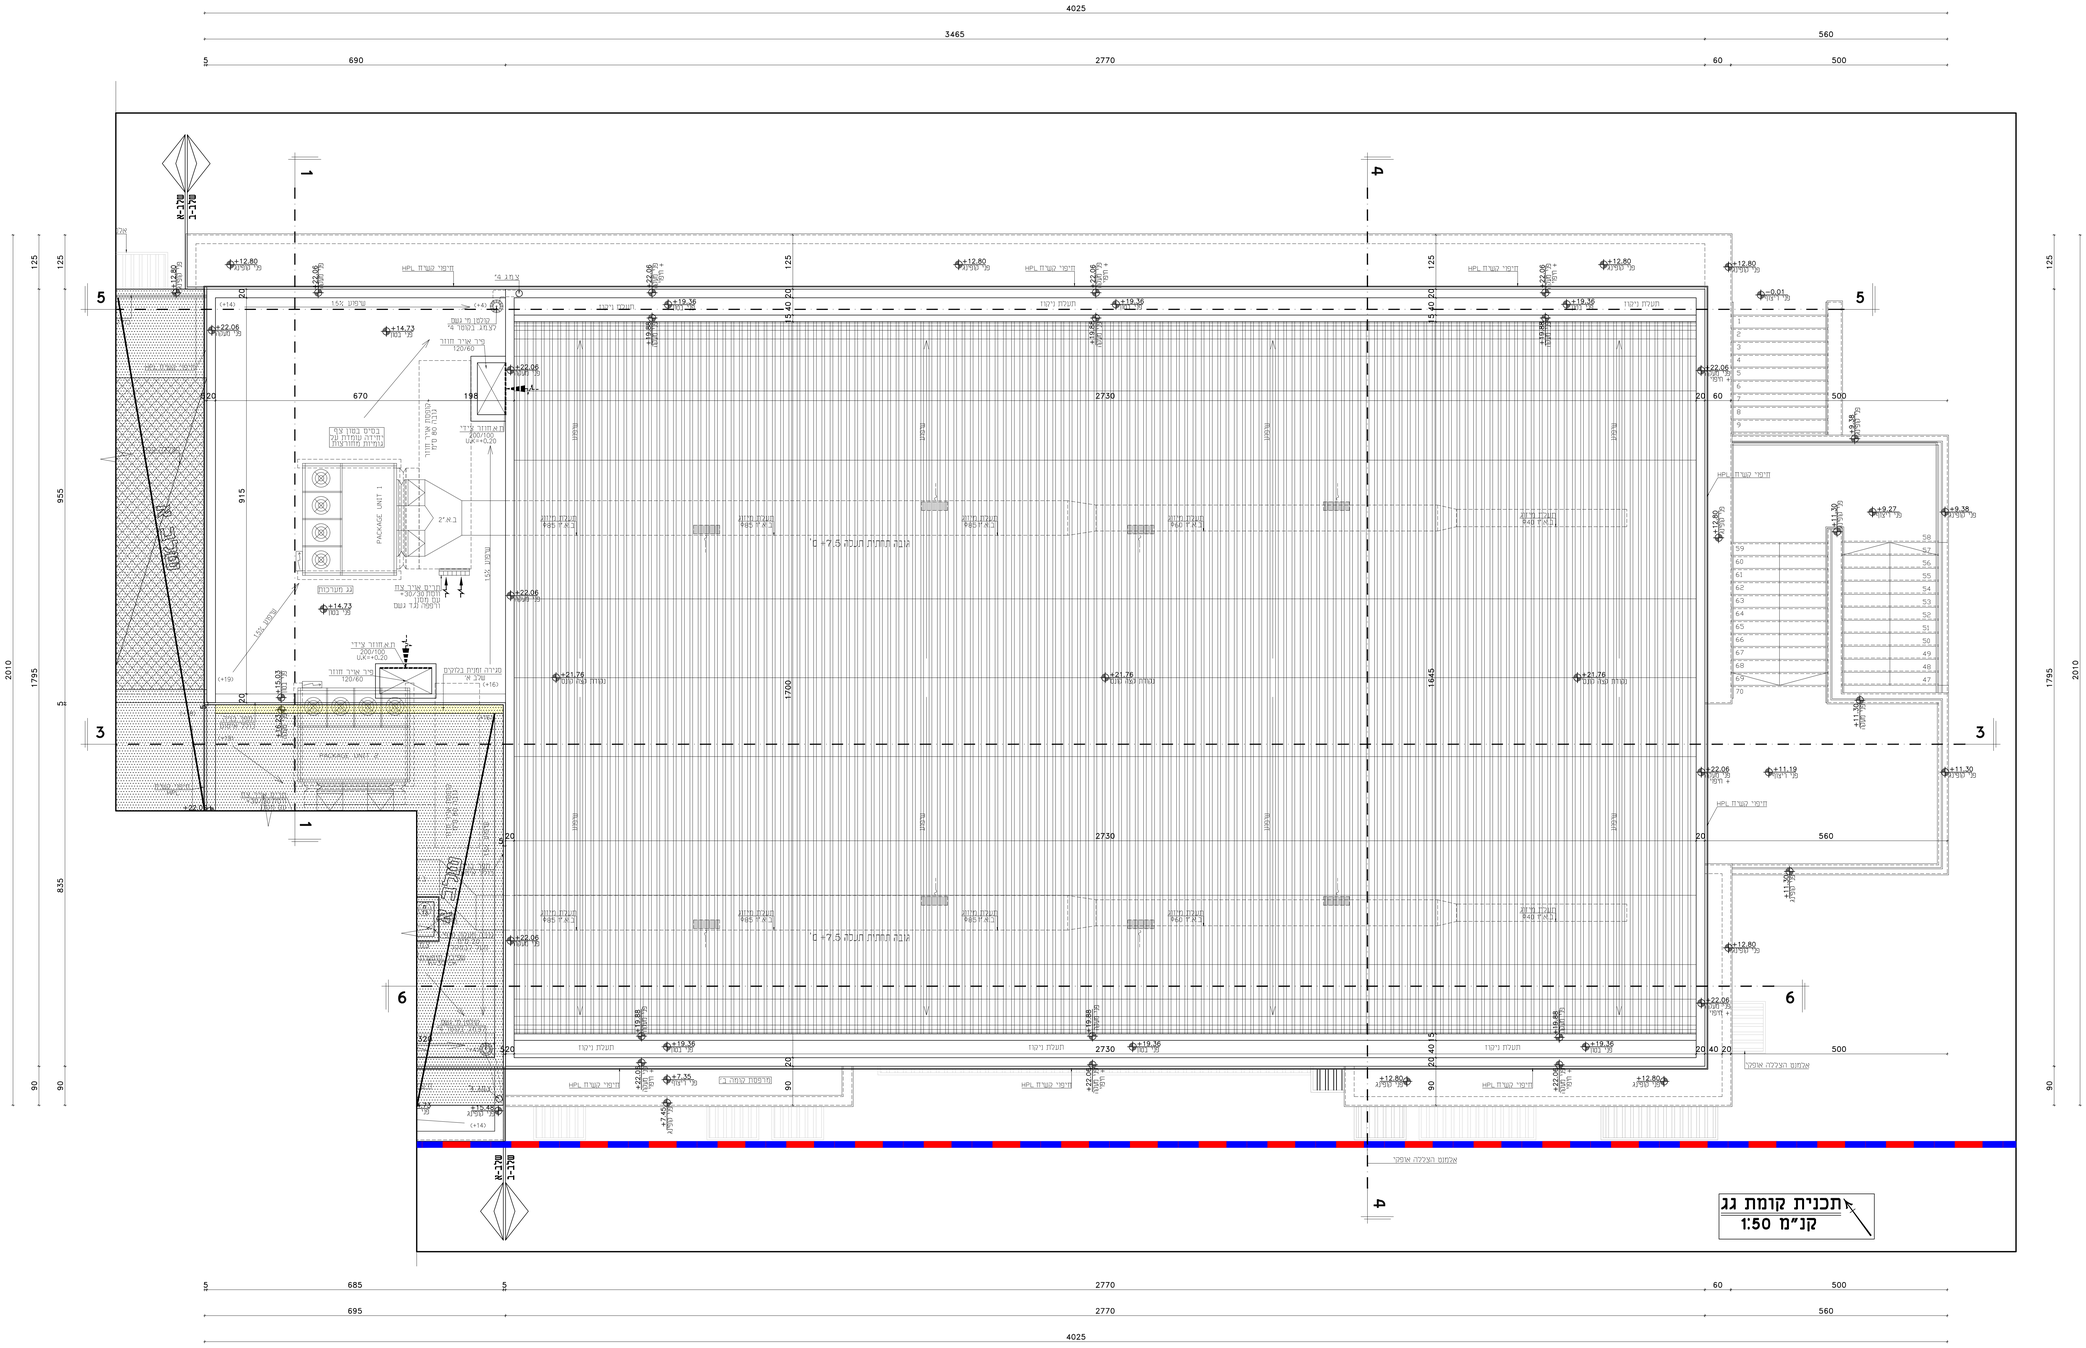

תאריך:	תמצה:	כמות:

תאריך:	שינוים:	מהדורה:

הערות כלליות:
- המבצע אחראי לבדיקת המידות והתאמתן במקום.
- בכל מקרה של ספק, טעות או אי התאמה יש לפנות למתכנן.
- אין לבצע מידות עפ"י מדידה מהשרטוט.
- חומרי גמר ואביזרי פרוזר יירכבו לאחר אישור המתכנן.
- אין לעשות כל שימוש בתכנית זו או ברעיונות הגלומים בה ללא אישור בכתב מהמתכנן.
- מהנדס רא"ו יונץ אשר שמו רשום מעל שם האדריכל בתכנית זו נושא לבדו באחריות המקצועית והחוקית לתכנית.

פרויקט:
בית ספר יסודי -24 כיתות
+ אולם ספורט
- מגרש 73 - בת ים

נושא:
תכנית קומת גג
-טלב ב'

לעיון	לאישור	למכרז 30.09.2024	לביצוע

מזמין: עיריית בת ים	מס' נ.ינון: PL-05	מהדורה: 01
אדריכל אחראי: טלסביל עומרי	מבצר: דנה מרמור	
קנה מידה: 1:50	מס' עבודה: 95/011	שבע: DA-95011-01

DATUM Eng Ltd
Engineering Services And Consulting
Tel: 04-6419957 | Fax: 04-6411646 | Kfar Kana 16930 | P.O.Box: 192
E.Mail: Datum@datum-eng.com