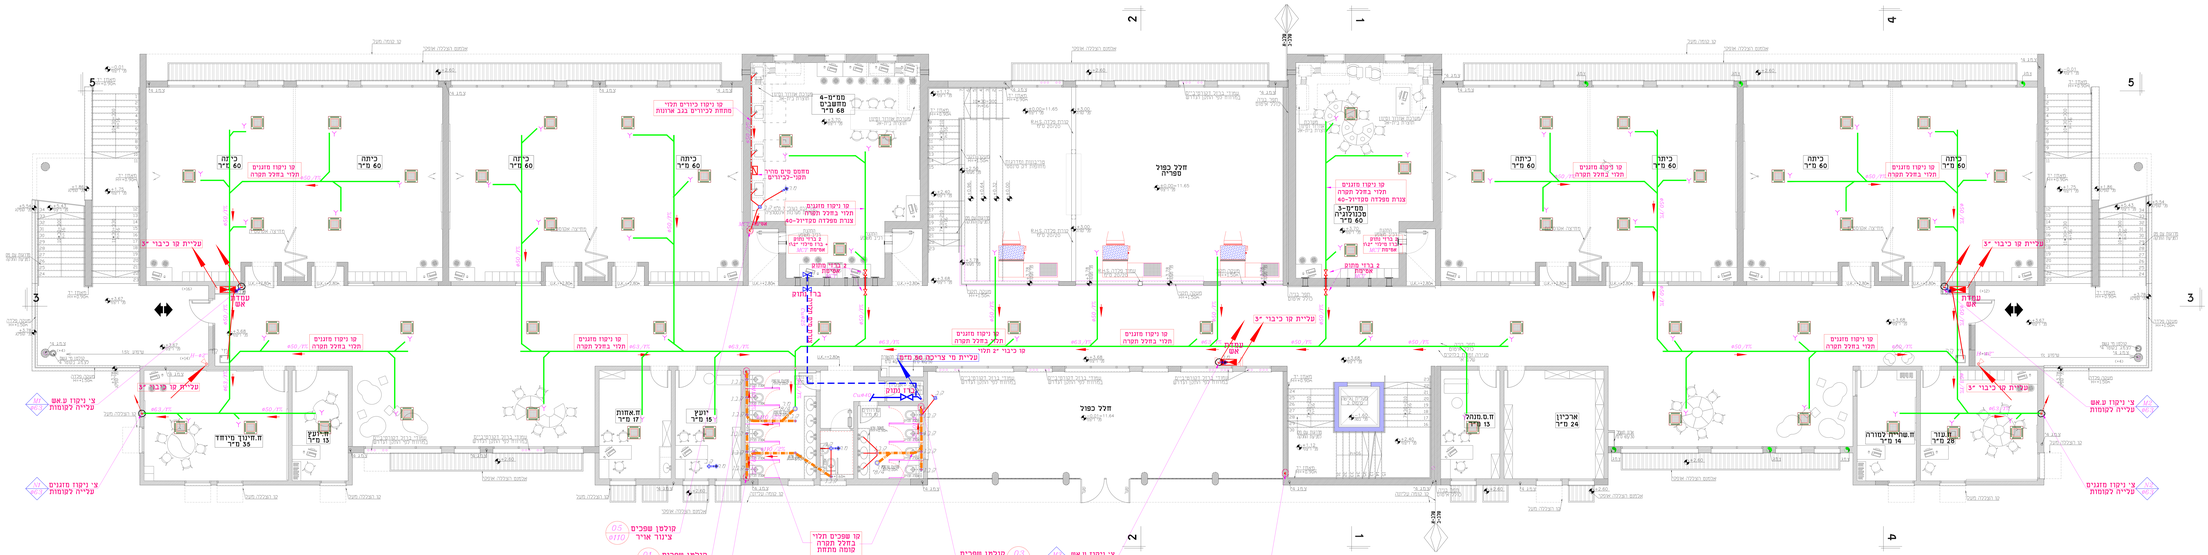
חדר מדרגות
חדר מדרגות
חדר מדרגות