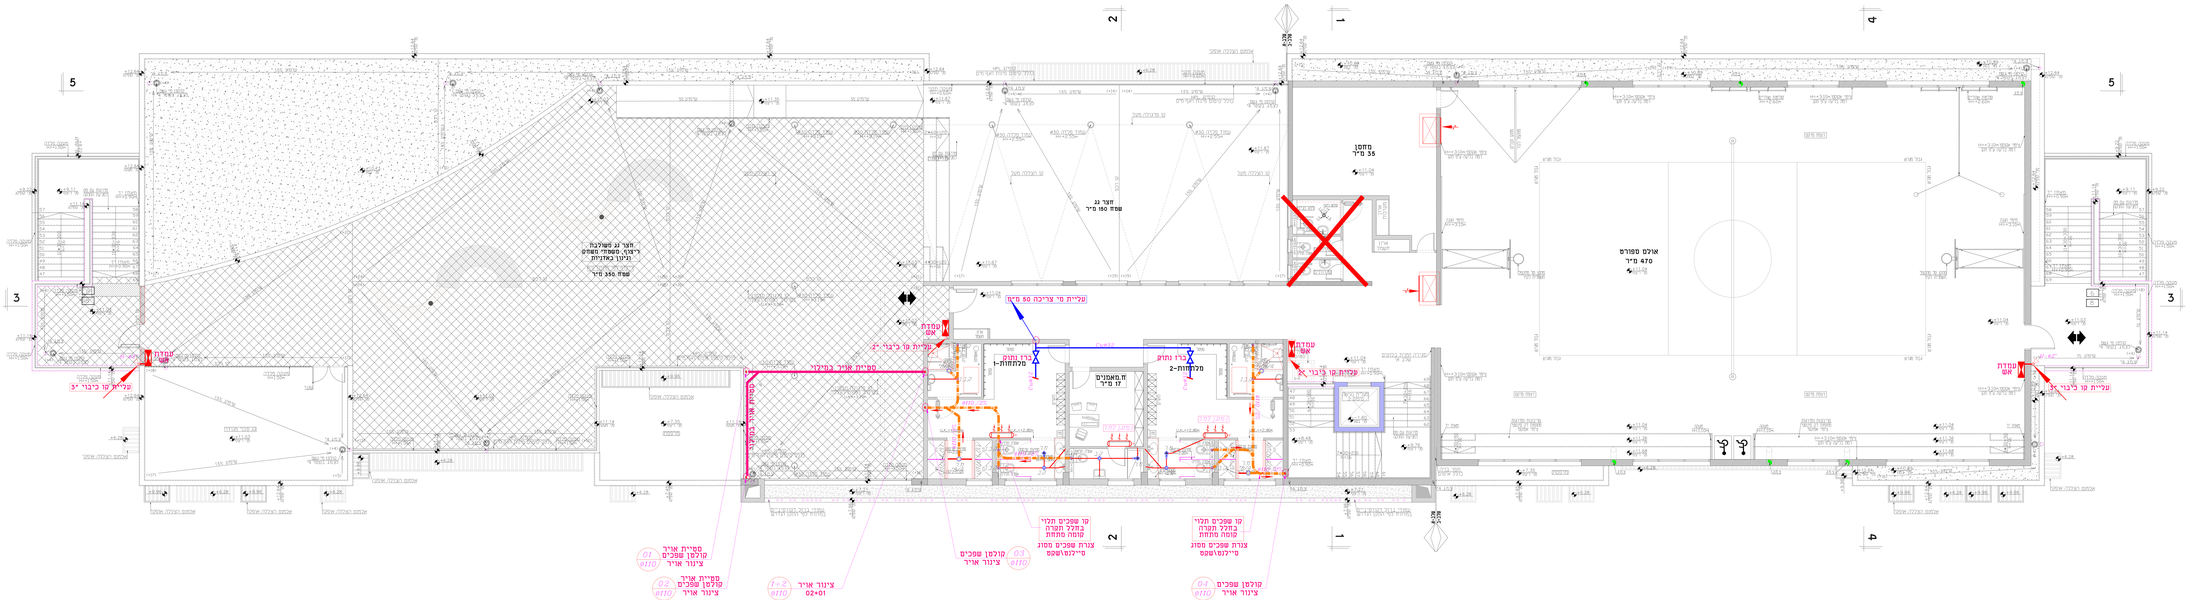
חדר גז משולבת רפואה, המאחז נמצים ונינון באוניות
משקל 350 מ"ר
חדר גז
משקל 150 מ"ר
מחסן
35 מ"ר
אולם ספורט
470 מ"ר
מ.מאמנים
10 מ"ר
מקלחות-1
מקלחות-2
עליית מי צריכה 50 מ"מ
עליית מי כיבוי "2
עליית מי כיבוי "3
עמדת אש
מסעדת אש
מסעדת אש
מסע