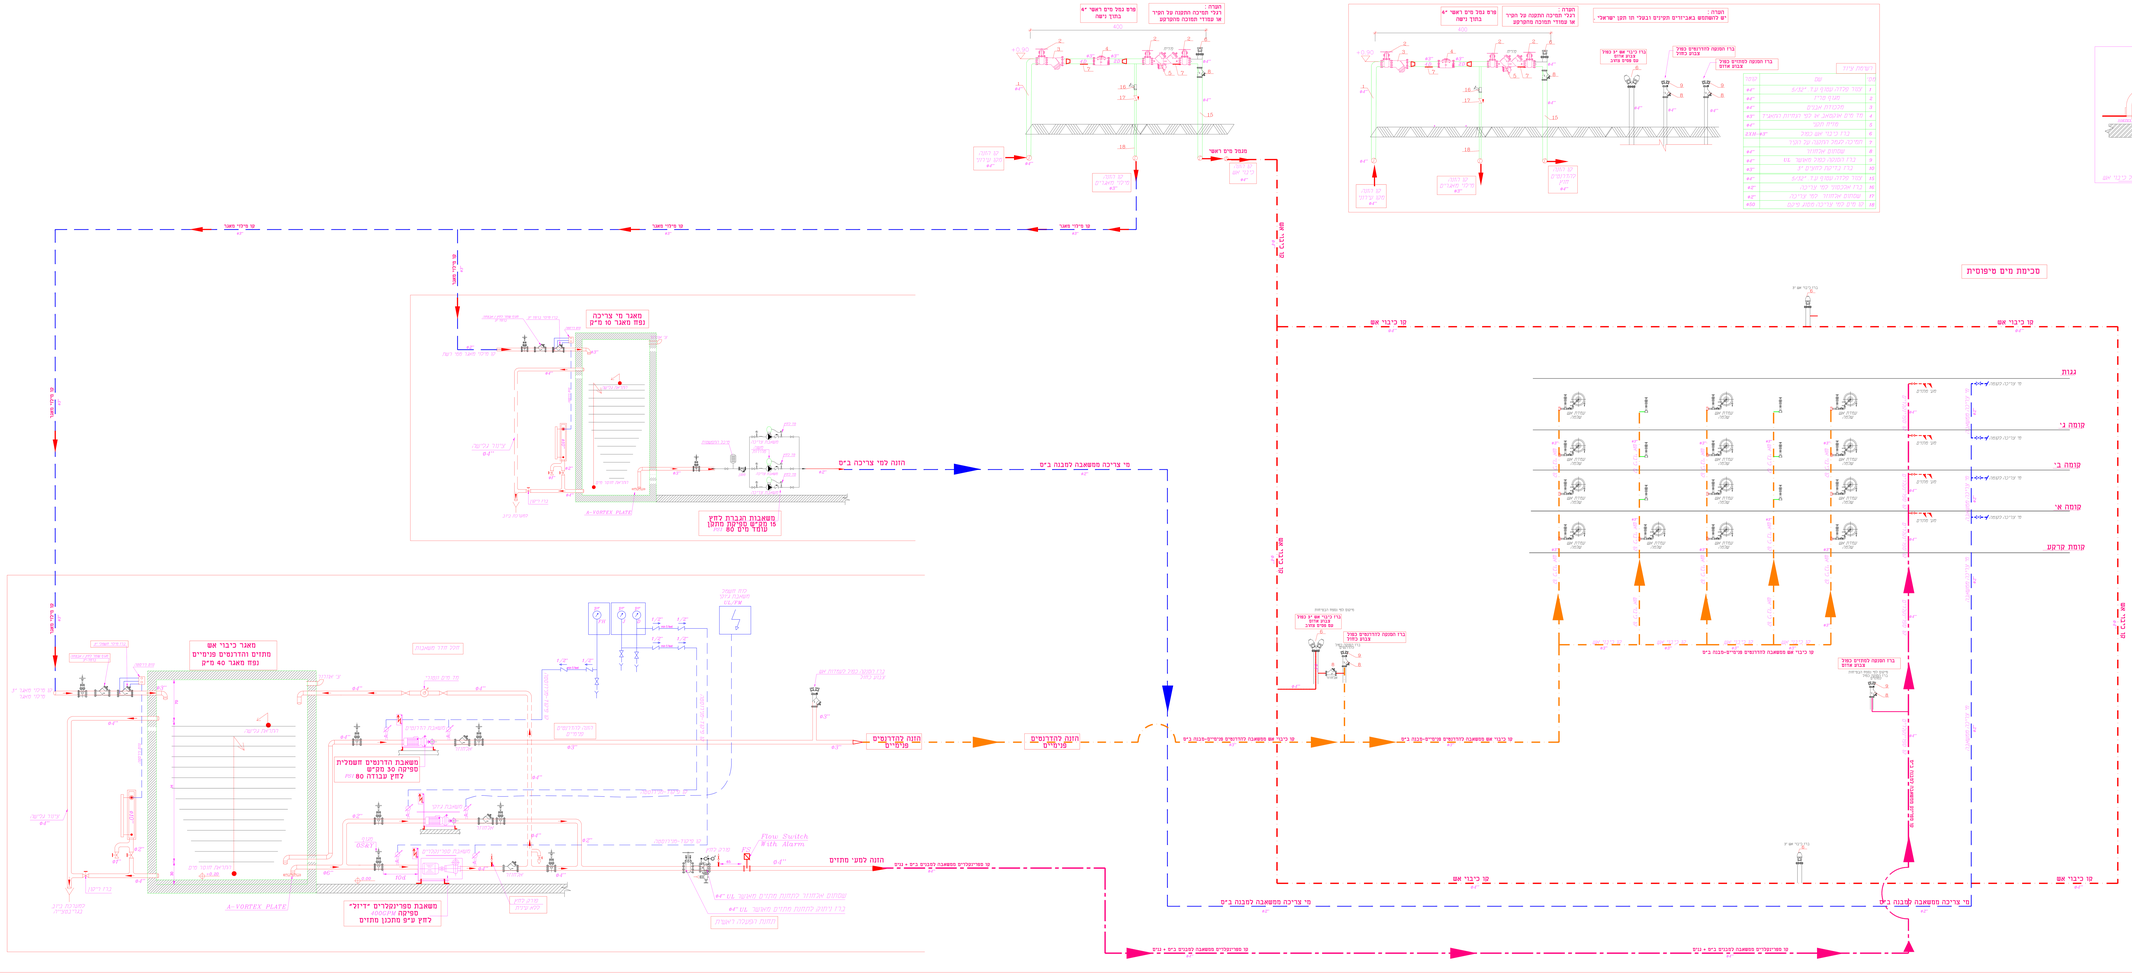
מאגר מי צריכה
נפח מאגר 50 מ"ק
חזרה לסי צריכה ב"מ
מי צריכה מסשאבה לתכנה ב"מ
משאבת הכבדת בחוץ
מי מים מקיקה מתכון
נחיר מים 80
מאגר ביבוי אש
מתוים והדרומים פנימיים
נפח מאגר 450 מ"ק
חזרה לתכנון מים
משאבת הדרומים משמכית
ספיקה 30 מ"ק
לחץ עבודה 80
חזרה לתכנון מים
Flow Switch
With Alarm
חזרה לסי מתחים
משאבת סרינקלרים "דיזל"
ספיקה
לחץ ע"פ מתכון מתחים
A-VORTEX PLATE
נגות
קומה ג'
קומה ב'
קומה א'
קומת קרקע
סכימת מים מיפוסית
מי ביבוי אש
מי ביבוי מאגר
מי מים ראשי
מקור מים ראשי
חזרה
רגלי תמיכה התקנה על הקיר
אי עמדי תמיכה מתעדכנ
מים נטל מים ראשי "4
בחוץ ראשי
חזרה
"יש לשמשם באביזרים תשיים ובעלי תו תקן ישראלי"
רגלי תמיכה התקנה על הקיר
אי עמדי תמיכה מתעדכנ
מים נטל מים ראשי "4
בחוץ ראשי
רשימת ציוד דורות
הכנות לחץ להידרנטים
מערכת מיכלי מאגר מים לצריכה
מערכת הכנות לחץ מאוגמחת לצריכה
גבן הנדסה יעוץ הנדסי
G R
שם הפרוייקט
ב"מ 24 כיתות
מגרש 73-בת ים
תוכן הגליון :
מעי אינסטלציה
סכימת מים
אדריכל: דאסמון מהנדסים
מזמין : דאסמון מהנדסים
Gaban Civil Eng
תכנון וניהול הנדסי
מערכות אינסטלציה סניטרית
מיזוג אויר ו הסקה ו כמיחות
054-6595776
gaban.eng.ltd@gmail.com