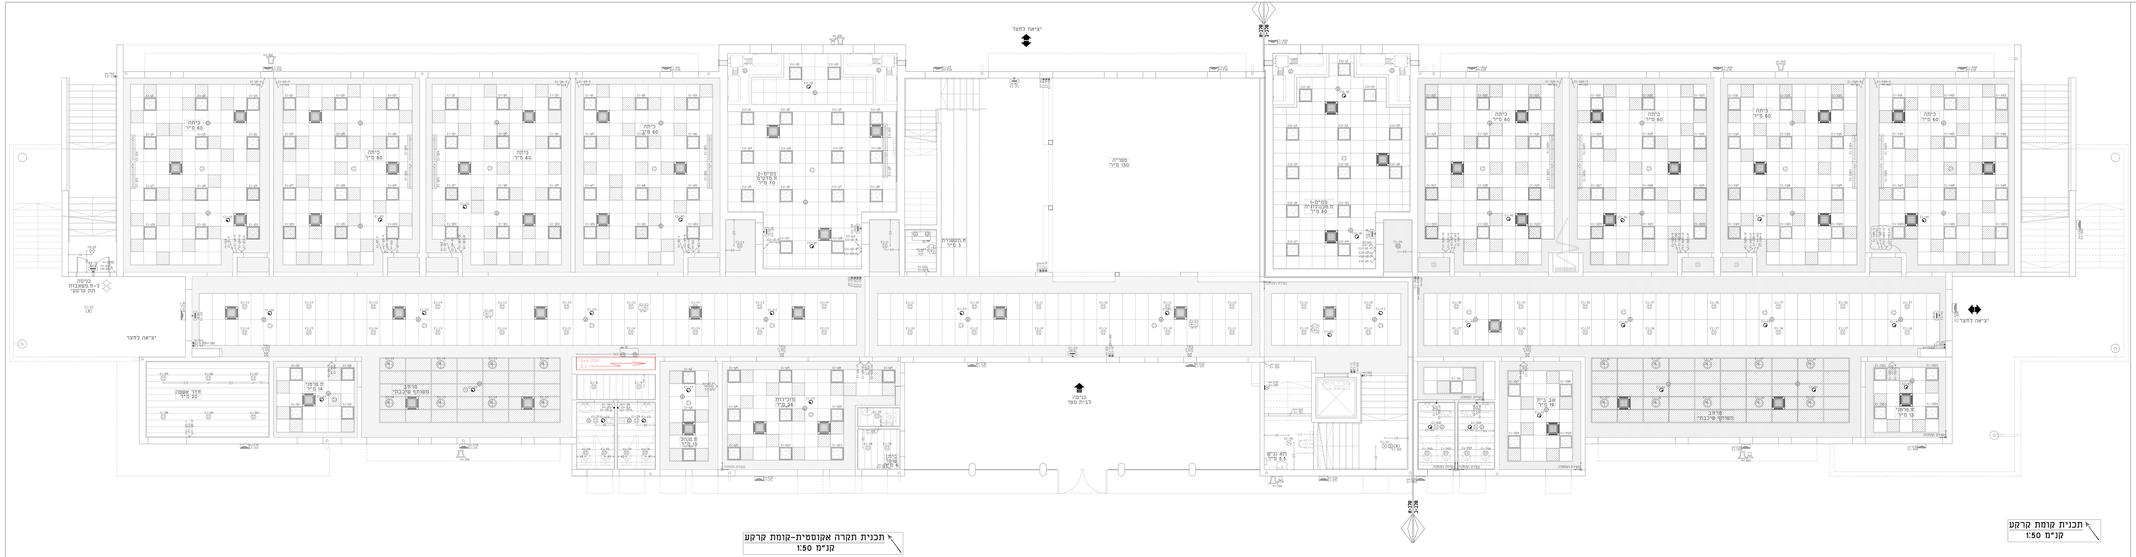
יציאה לחצר
יציאה לחצר
כניסה בית מגור
כניסה לבית המגורים
כניסה 60 מ"ר
מסדרון 350 מ"ר
מרפאה 3.5 מ"ר
מרפאה 3.5 מ"ר
מרפאה 3.5