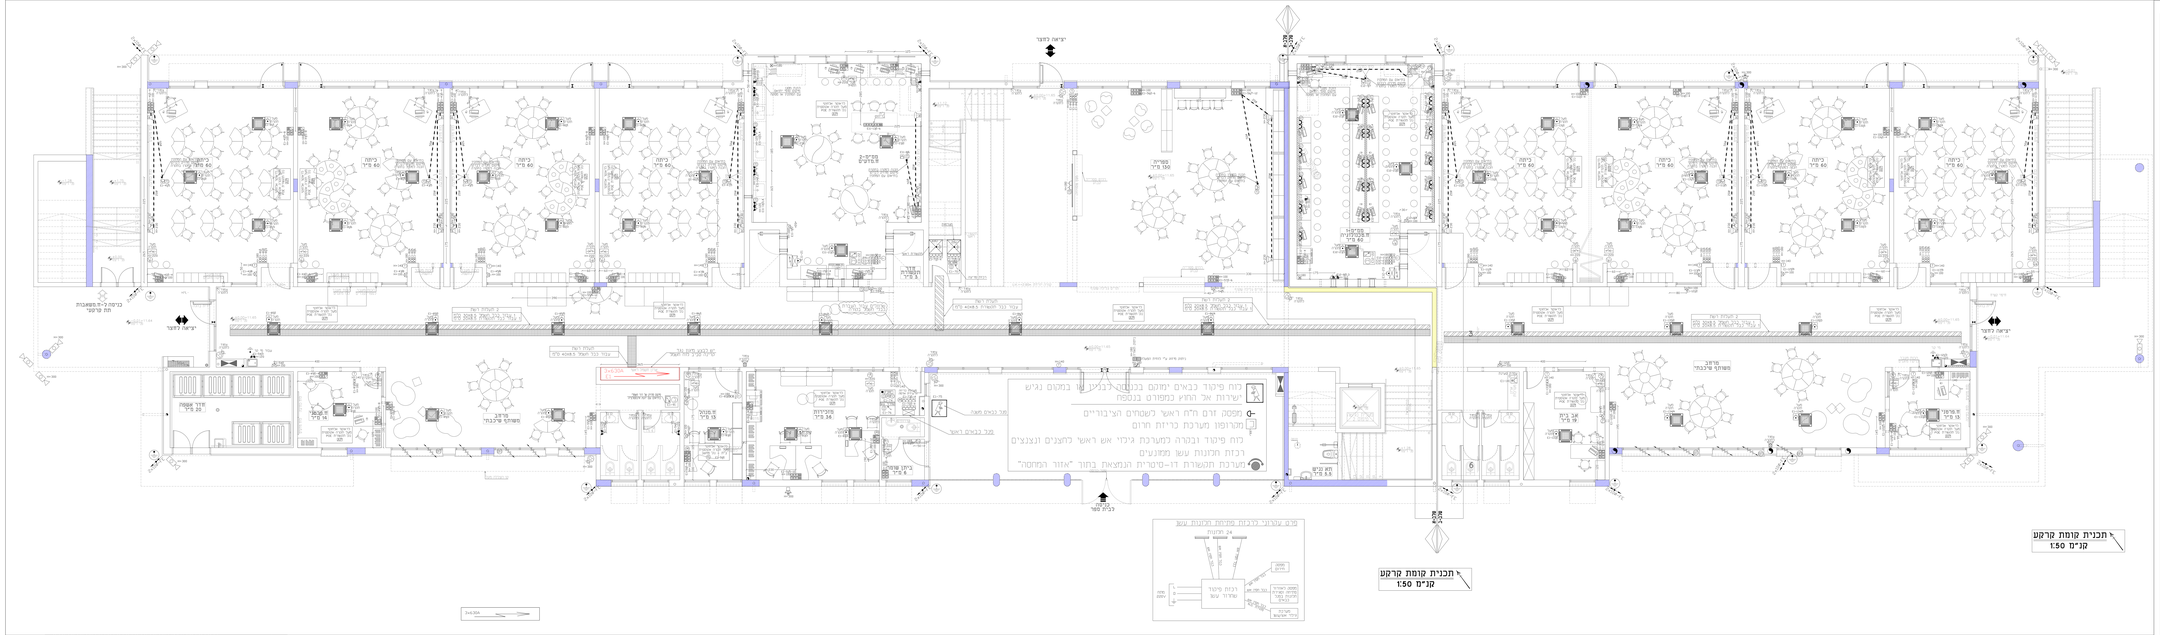
תכנית קומת קרקע
קנ"מ 1:50
תכנית קומת קרקע
קנ"מ 1:50
כניסה לבית מלאכות
יציאה לדרום
יציאה לדרום
יציאה לדרום
כניסה לבית מלאכות
מבנה מלאכות
מבנה מלאכות
מבנה