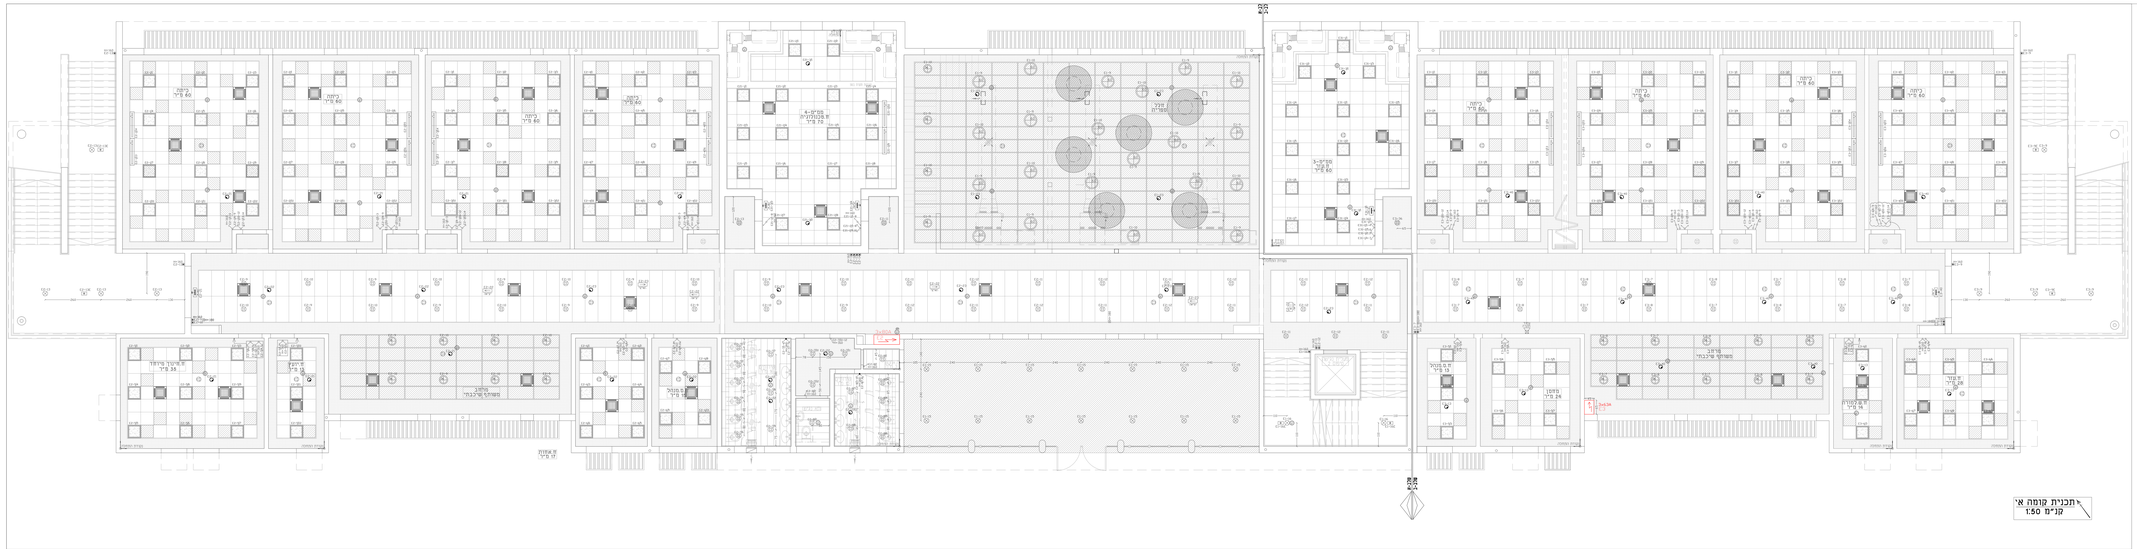

הערות לגבי האורה

לא נמסרה הוראה בנושא הזה. הוראה הכתובה בתוך הסכם אינה מספיקה לביצוע.

סמלים

- מנורת תקרה לד מלבנית בגודל 60 סמ' x 60 סמ' מדגם Philips CoreLine Prismatic Recessed 59W 4000K 4000lm 840 PSU
- מנורת תקרה לד מלבנית בגודל 60 סמ' x 60 סמ' מדגם Philips CoreLine Prismatic Recessed 59W 3000K 4000lm 830 PSU