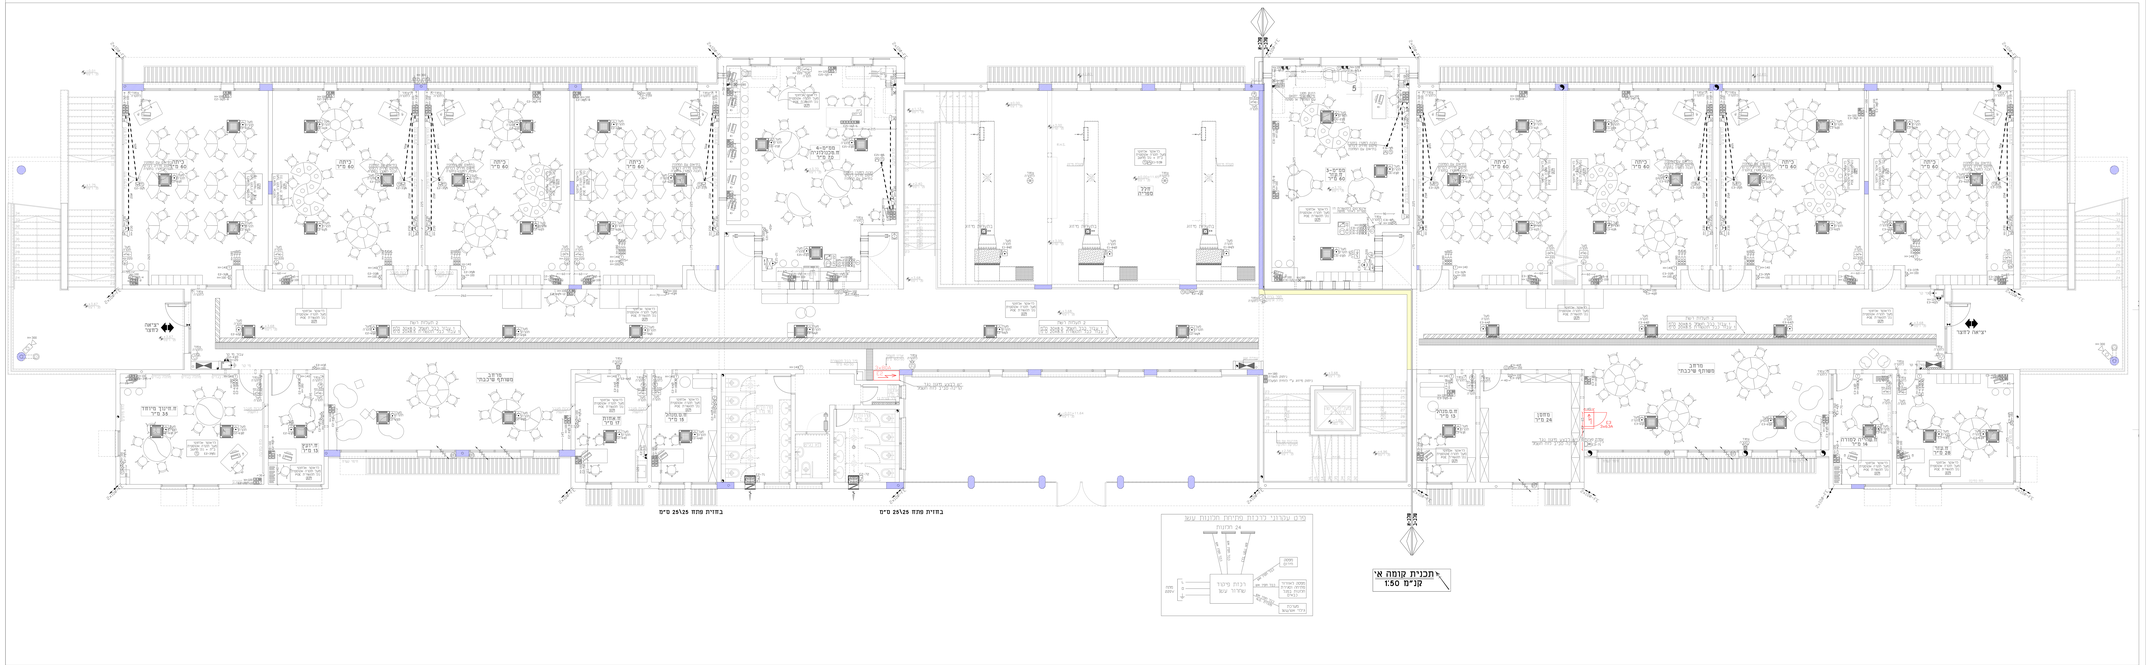
תכנית קומה א'
קנ"מ 1:50
בחזית מתח 25x25 מ"מ
בחזית מתח 25x25 מ"מ
מרפאת שיניים
מרפאת שיניים
מרפאת שיניים