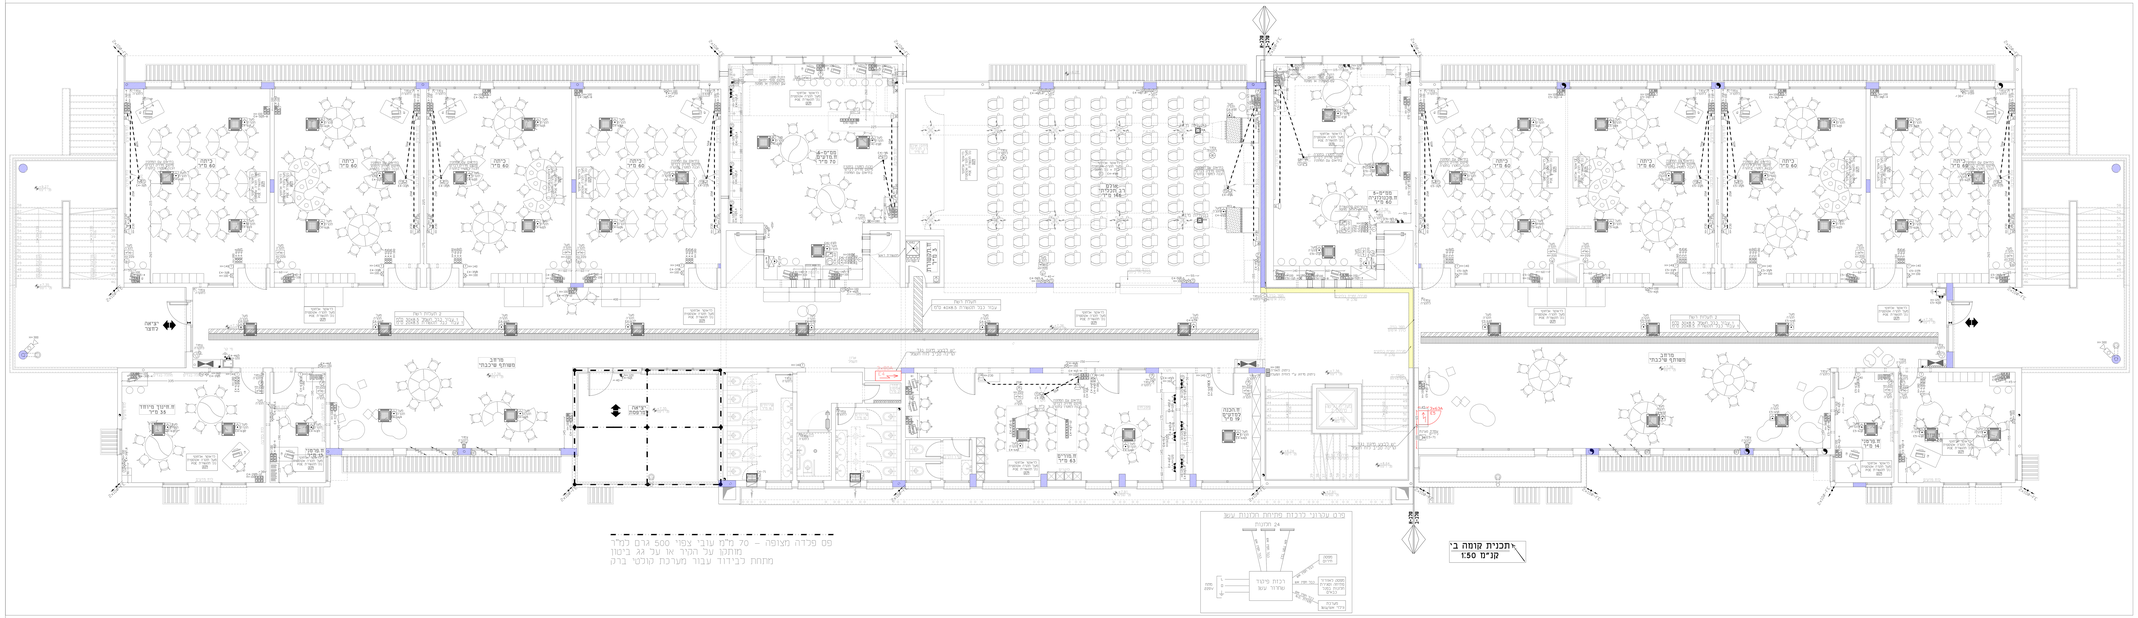
יחכנית קומה בי
קנ"מ 1:50
פס סרגל מצופה - 70 מ"מ עובי צפוי 500 גרם למ"ר
מחוטו על הסיר או על גג ביטון
מתחת כביביוד עבור מערכת קרטיב ברט
מרכז מלכבוד
מרכז מלכבוד
מרכז מלכבוד