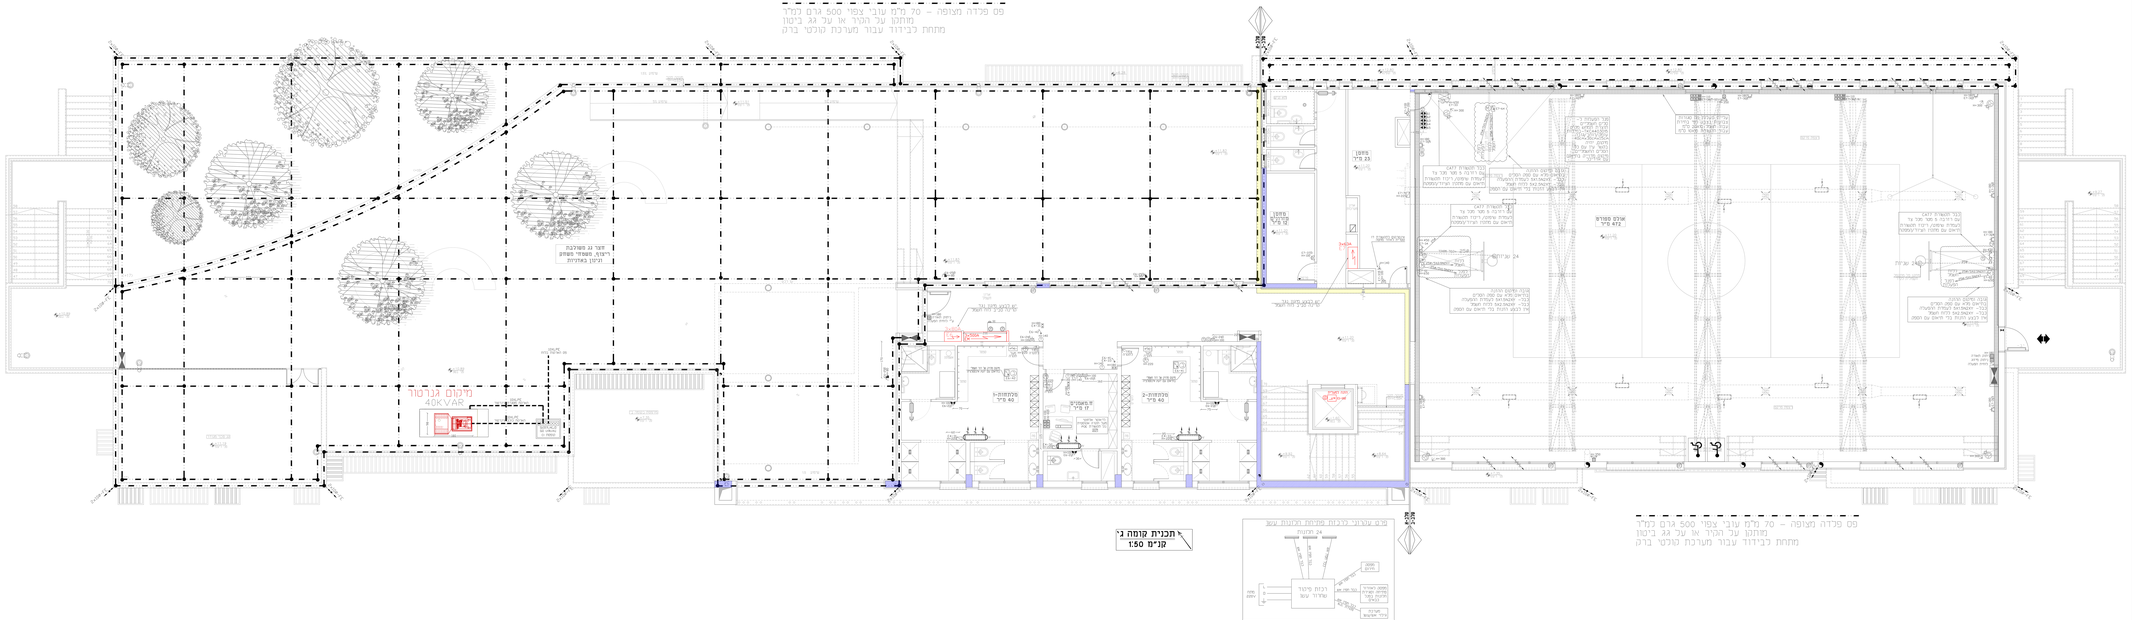
פס פלדה מצופה - 70 מ"מ עובי, עפר 500 גרם נמדד
מחוזק על הגג או על גג ביטון
מחבת בריחוד עבור מערכת טוכני ברג
אזור גן משרבת
ריצוף מפמלי מפוש
וגינון באדניות
מיקום קונסה
40KVAR
מטבחון-1
60 מ"ר
מטבחון-2
60 מ"ר
אזור משרדים
בלת מ"ר
מבנה עזר
מבנה עזר
מבנה עז