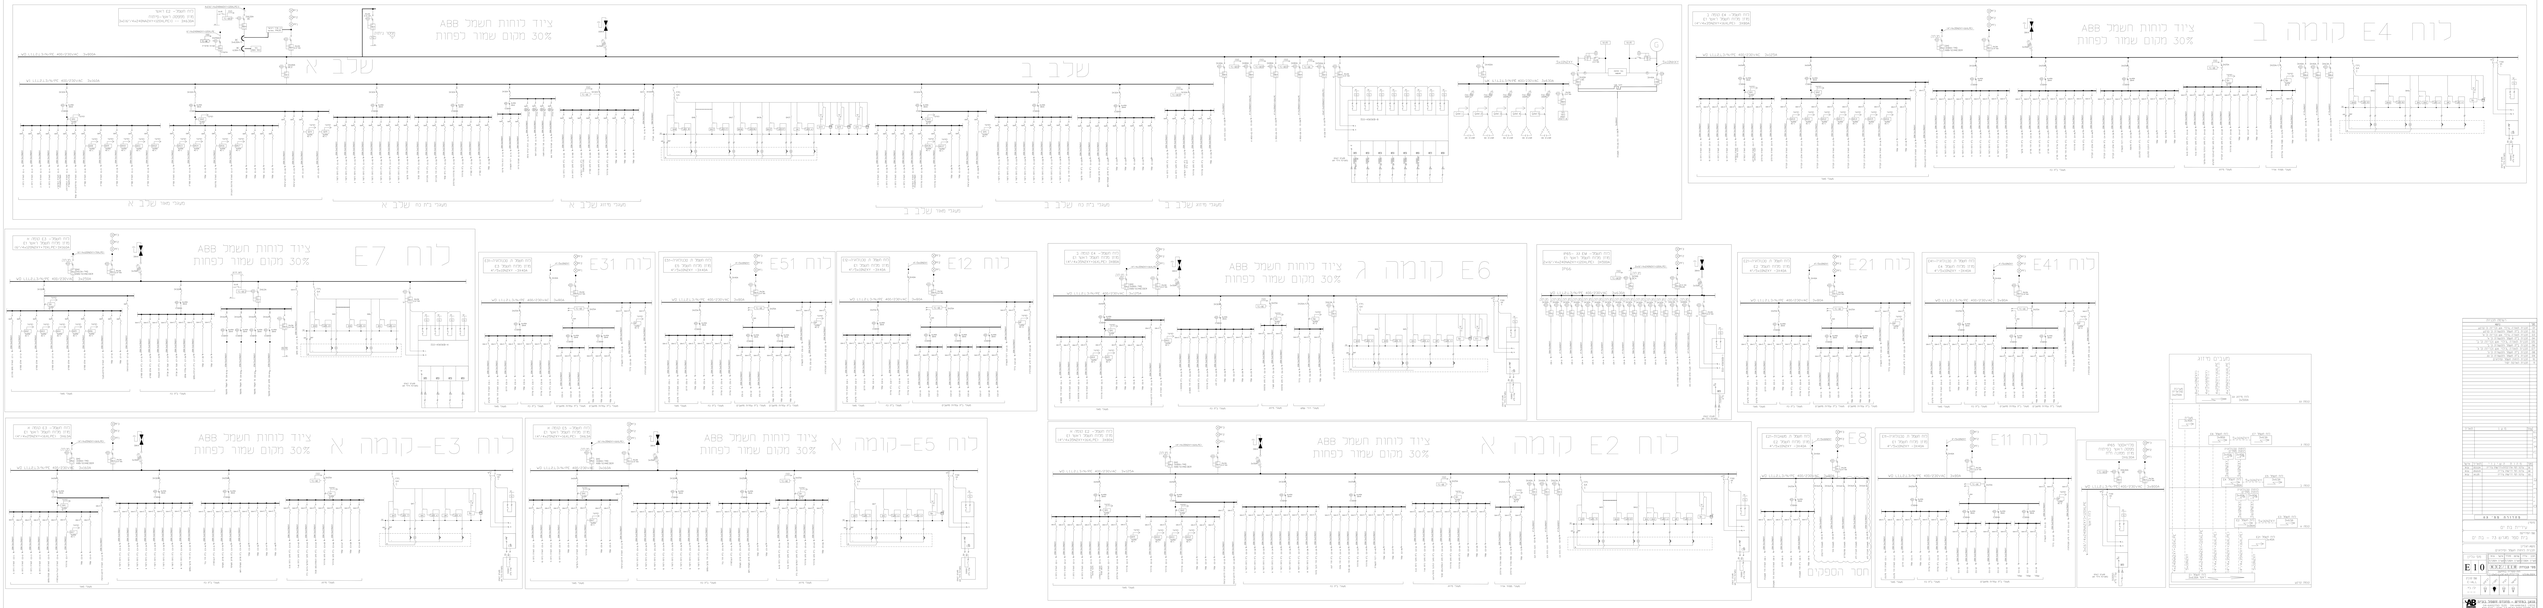
ציוד כוחות השמל ABB
30% מקום שמור לפחות
שלב א
שלב ב
לוח E4 קומה ב
לוח E7
לוח E31
לוח E51
לוח E12
לוח E6 קומה ג
לוח E21
לוח E41
לוח E3-קומה א
לוח E5-קומה א
לוח E2 קומה א
לוח E8
לוח E11
חדר הטפלים
E10