הערה:
*פרט זרוע+עמוד תאורה יתואם בין אגף חשמל עירייה לבין ספקי עמוד וגופי תאורה.
*ברגי יסוד עמוד תאורה יהיו דפיזיים נגד קוריזיה.
*הפנסים יוזמנו ע"י ספק עם צביעה מתאימה לאוירה ימית.
*חיבור כבל לפנס תהיה באחריות ספק ולא קבלן כדי לשמור על אטימות.
*הגופים יהיו עם אחריות 5 שנים לפחות.

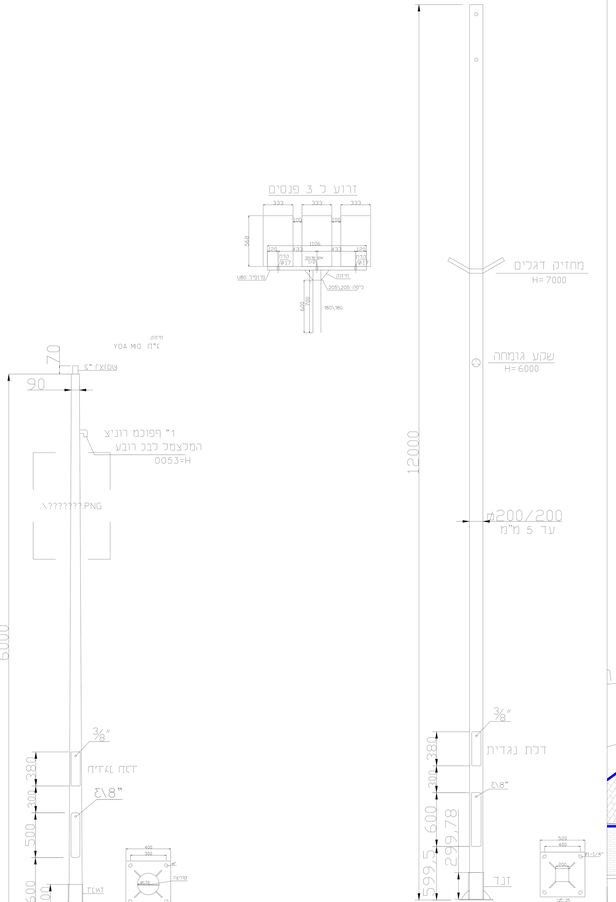

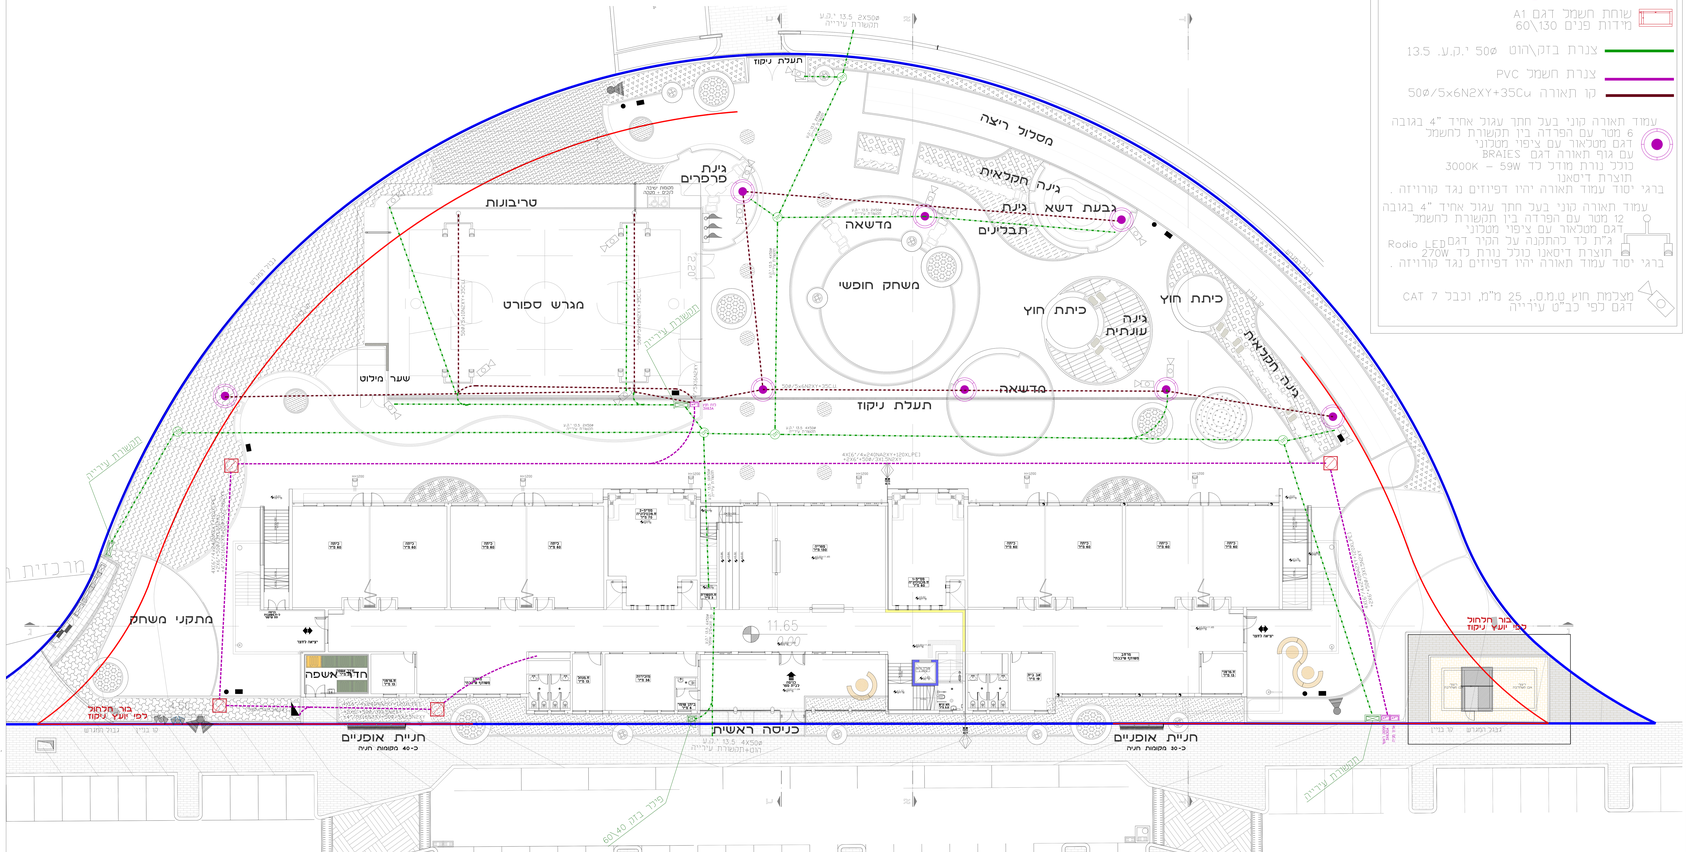

מקרא:

תקן	תא תקשורת
	תא חשמל
	שוחת חשמל דגם A1 מידות פנים 60\130
	צנרת בזק\הוט 50ø 13.5 מ.ק.ע.
	צנרת חשמל PVC
	קו תאורה 50ø/5x6N2XY+35Cu
	עמוד תאורה כוני בעל חתך עגול אחיד "4 בגובה 6 מטר עם הפרדה בין תקשורת לחשמל דגם מטלאור עם ציפוי מטלוני עם גוף תאורה דגם BRAIES כולל נורת מודל לד 59W 3000K – תוצרת דיסאנו ברגי יסוד עמוד תאורה יהיו דפיזיים נגד קוריזיה.
	עמוד תאורה כוני בעל חתך עגול אחיד "4 בגובה 12 מטר עם הפרדה בין תקשורת לחשמל דגם מטלאור עם ציפוי מטלוני ג"מ לד כהתקנה על הקיר דגם Rodio LED 27W תוצרת דיסאנו כולל נורת לד ברגי יסוד עמוד תאורה יהיו דפיזיים נגד קוריזיה.
	מצלמת חוץ ס.מ.מ., 25 מ"מ, וכבל CAT 7 דגם לפי כב"ט עירייה