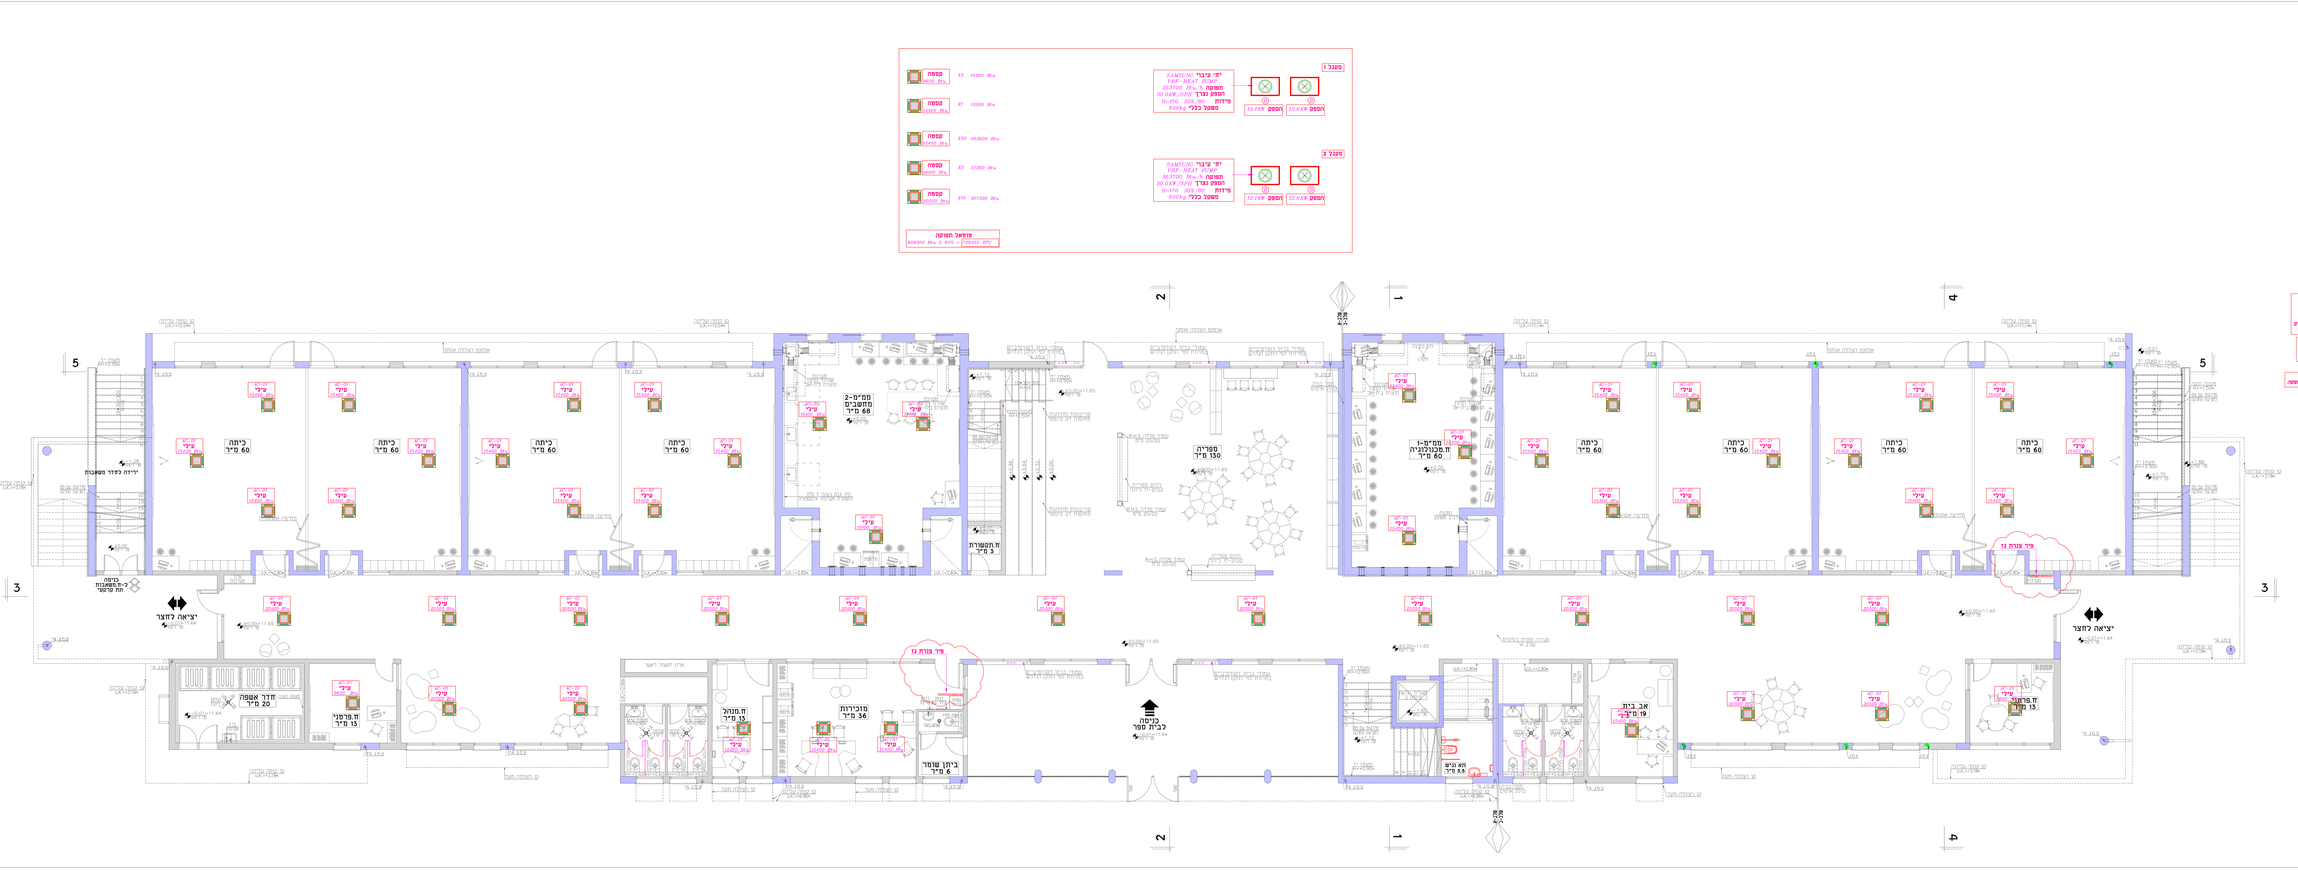

נבן הנדסה יעוץ הנדסי

GABAN CIVIL ENG

G R

שם הפרוייקט

ב"ס 24 כיתות
מגרש 73-בת ים

חוכן הגליון:

מפי מיזוג אוויר
קומת קרקע

אדריכל: דאסום מהנדסים

מזמין: דאסום מהנדסים

מספר: 73_24	שרטט: נ.נ.ל
תאריך: 24	קנה: 1:50

01

Gaban Civil Eng
מתכנן הנדסי הנדסי
מערכות אינסטלציה מכניות
מיזוג אויר • הסקה • בטיחות
054-6595776
gaban.eng316@gmail.com
כתובת: רח' קוטלר 66/7 בת ים 6970317