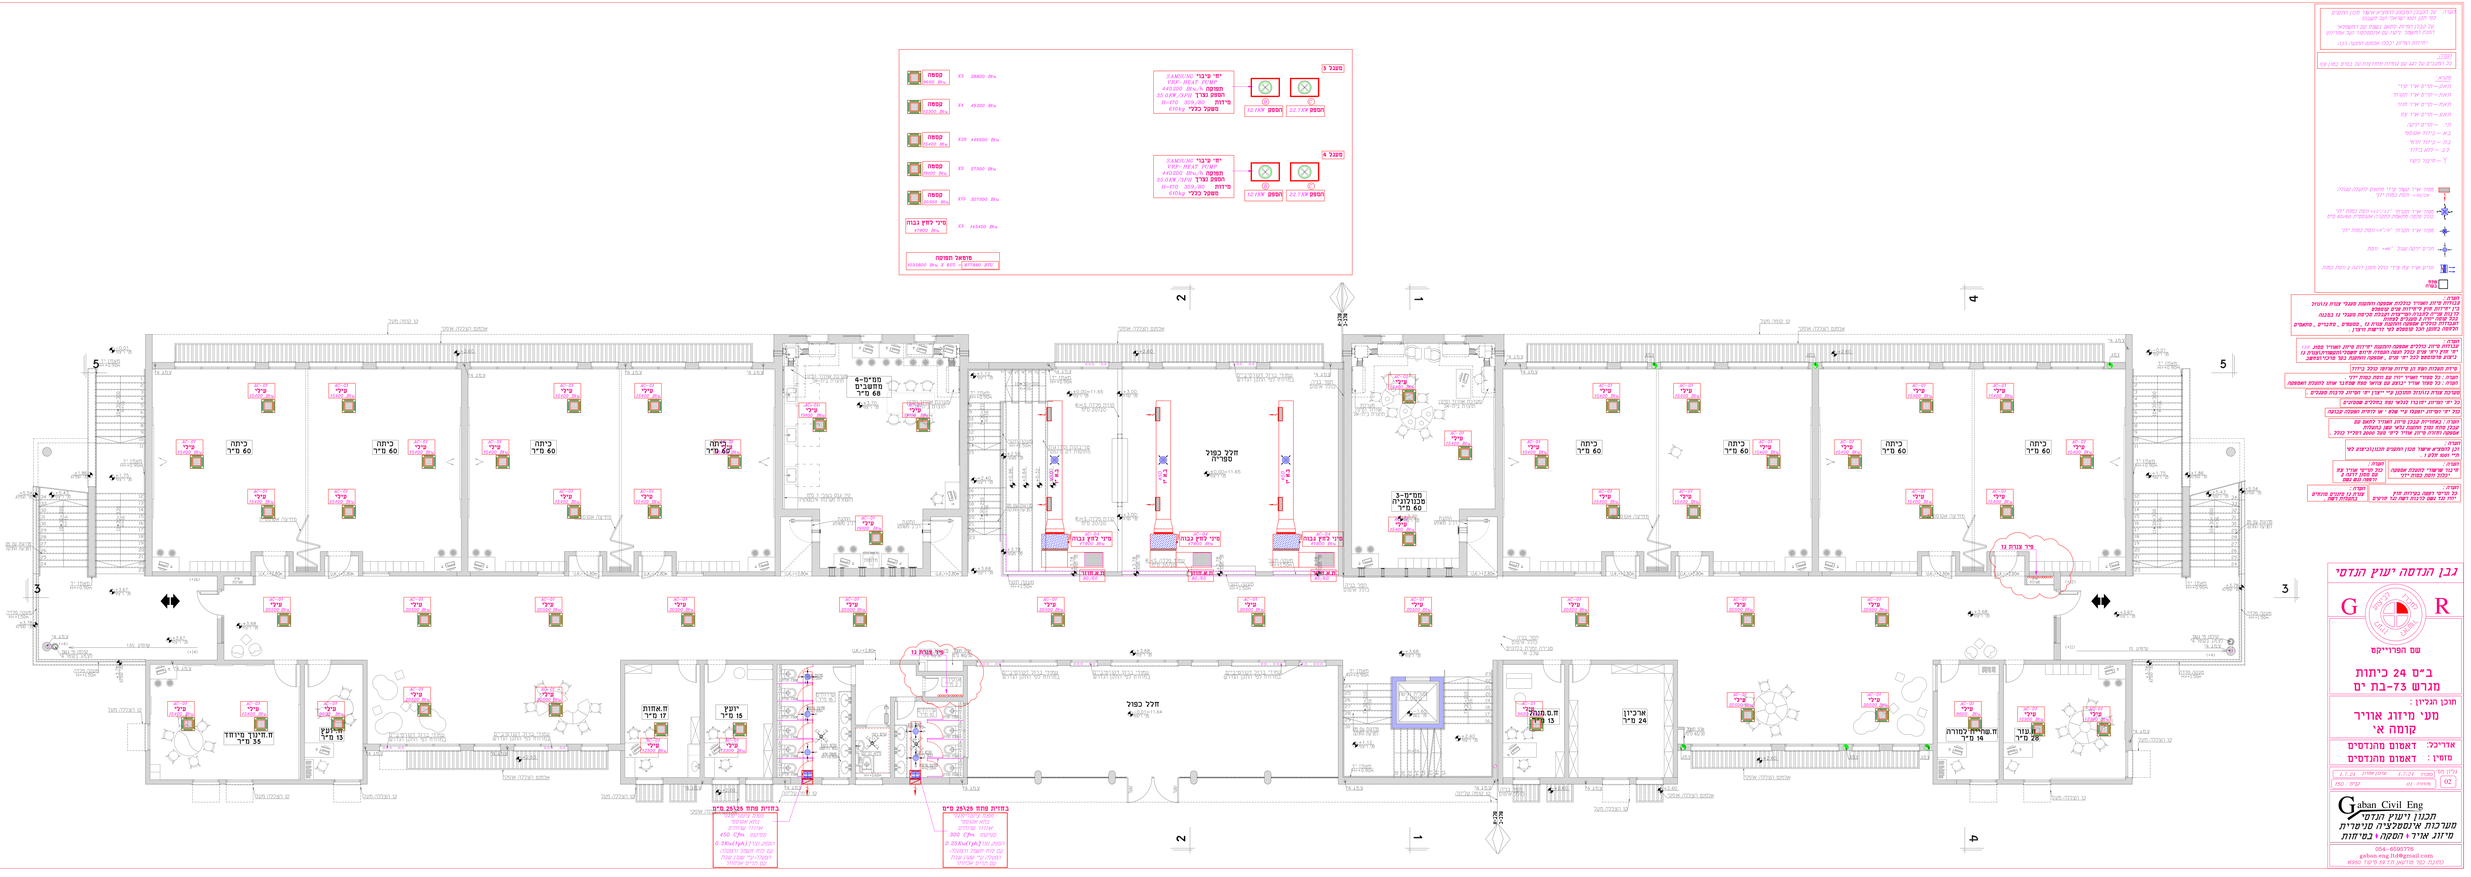

נבן הנדסה יעוץ הנדסי

GABAN CIVIL ENG. G R

שם הפרוייקט

ב"ס 24 כיתות
מגרש 73-בת ים

חוכן הגליון:

מפני מיזוג אוויר
קומה א'

אדריכל: דאסום מהנדסים

מזמין: דאסום מהנדסים

מס. גליון	02
מספר	17.24
עיכ"מאיר	נ.ב.ל
מאיר	יעא
קנ"מ	1:50

Gaban Civil Eng
תכנון יעוץ הנדסי
מערכות אינסטלציה מכנית
מיזוג אויר • הסקה • כיבוי אש

054-6559796
gaban.eng316@gmail.com
כתובת: רח' קדושי הלל 23 בת ים 6950