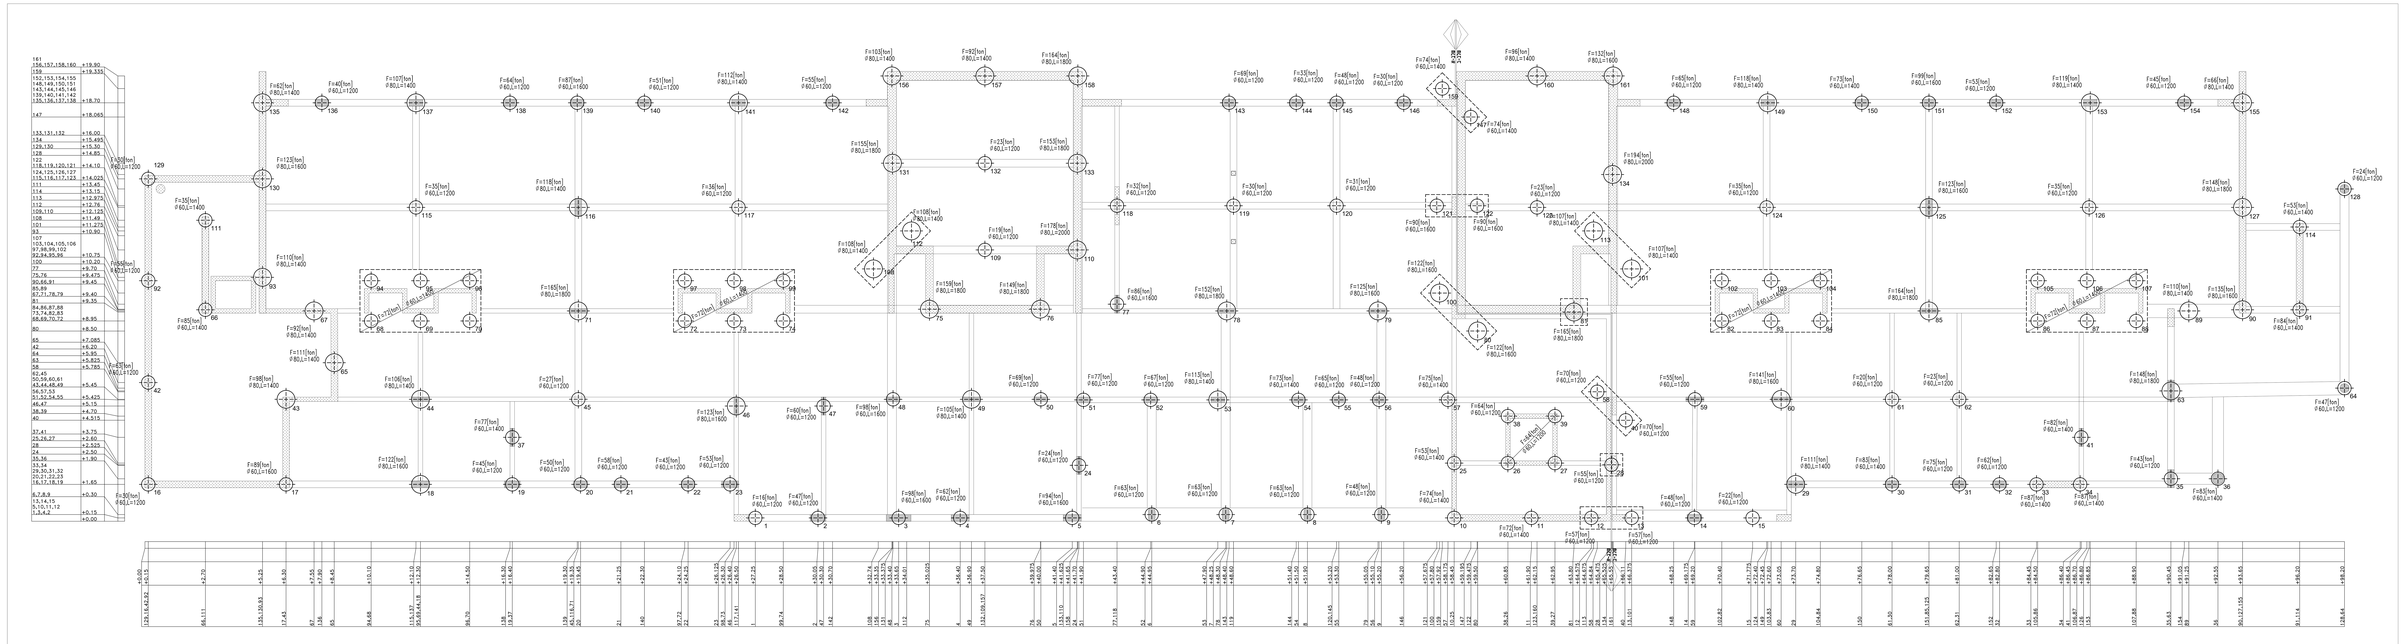

תכנית זז

לסמרז	לעיון	לבצוע

מקרא

- קיר בטון מפוסק
- קיר בטון מחוזק
- קיר בטון משענ
- עמוד מפשיל
- עמוד מפוסק
- עמוד מחוזק
- מחברים משענ על פיר/עמוד

הערות

הבנין אחוד לטיחות עכו כבנין.
כל הפרוזות הנדרש לסתכנן על כל
קנה מ"ר הוספה לא בבנין
שלא מוגשה מ"ר נוספת לאוכלוסת כלא
ערבי ומעבנו.
נסף, בחנסה הבריח יש בבנים את
הרעיה

הערות

הבנין אחוד לטיחות עכו כבנין.
כל הפרוזות הנדרש לסתכנן על כל
קנה מ"ר הוספה לא בבנין
שלא מוגשה מ"ר נוספת לאוכלוסת כלא
ערבי ומעבנו.
נסף, בחנסה הבריח יש בבנים את
הרעיה

בסון ב-30 כפי ת"ר 118
מומת פלדה מעוגנים
כפי ת"י 466 חבק 3
מומת מסוג 500W1 400W
רשת מסומסת פלדה
מעוגנים כפי ת"י 580

מסב"ב אב+ב

1-ב

1:50-ב"מ	שרטט: מרסה עבאנה
	בקר: נשאטה מופדי
תאריך	הערות
02.07.24	לסמרז 1

שם הפרויקט: בית ספר יסודי -24 כיתות + אלם ספורט

מקום עבור: עדיית בת ים

מבנים: בת ים / עדיית/ מגרש 2024/מגרש

נעאמנה מופדי
מהנדס בנין
מרחוב: ז'בוטינסקי 34 רמת-גן
טלפון: 04/8853222
פקס: 04/6745003
נייד: 0505560338
e-mail: Mufdi@mufdi-eng.com