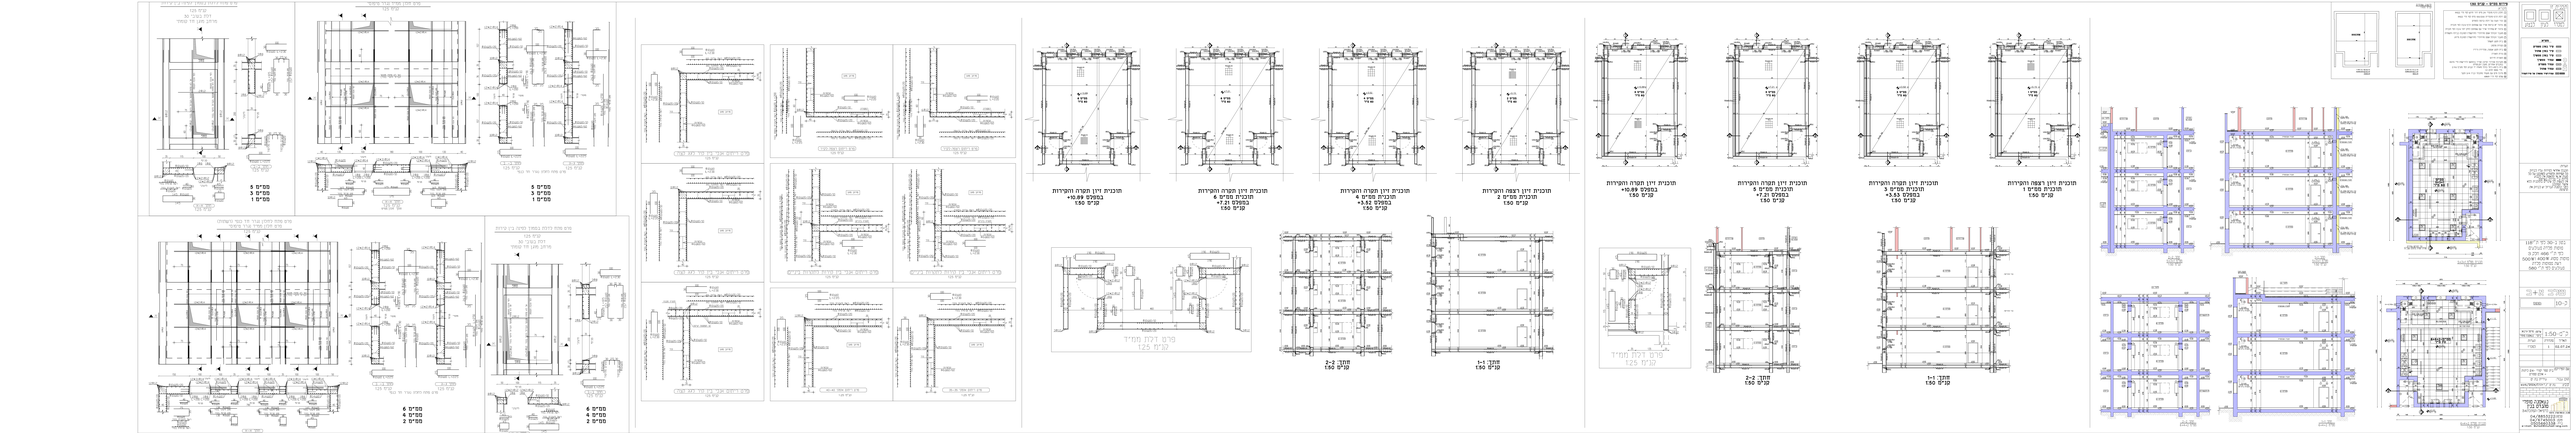
תוכנית דיון תקרה והסריות
מס"מ 5
מס"מ 3
מס"מ 1
תוכנית דיון תקרה והסריות
מס"מ 6
מס"מ 4
מס"מ 2
חתך 1-1
1:50
חתך 2-2
1:50
פרט דלת מחיר
מ"מ 125
מס"מ 5
מס"מ 3
מס"מ 1
מס"מ 6
מס"מ 4
מס"מ 2
מס"מ 5
מס"מ 3
מס"מ 1
מס"מ 6
מס"מ 4
מס"מ 2