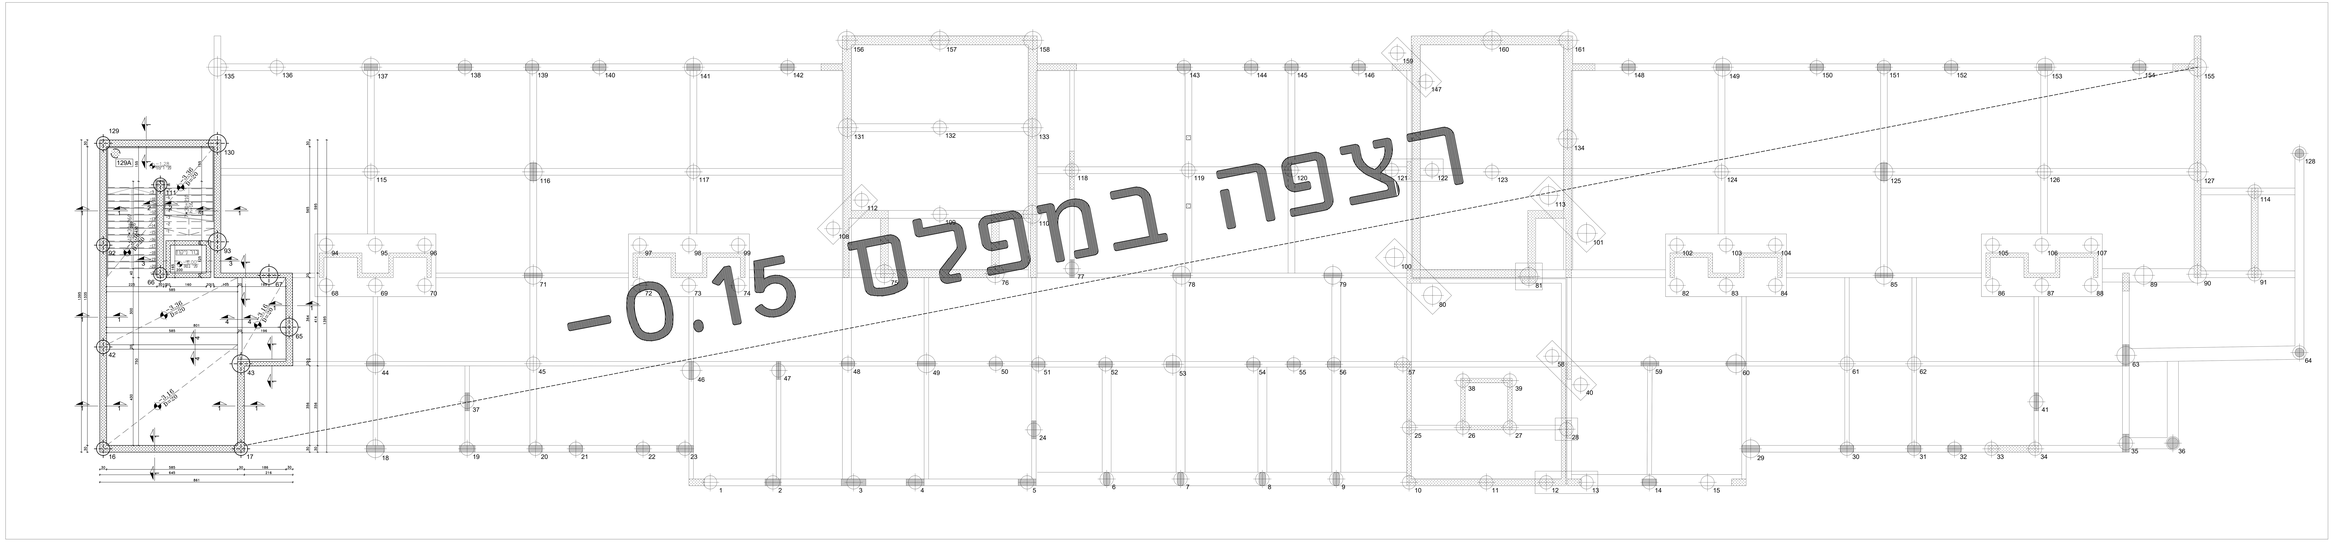

חתך: 1-1
1:20

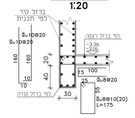

חתך: 2-2
1:20

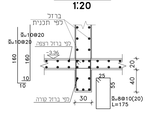

חתך: 4-4
1:20

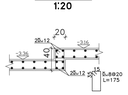

פרט עמוד שתול על תקרה
1:20

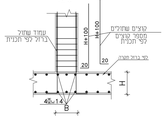

חתך: 3-3
1:20

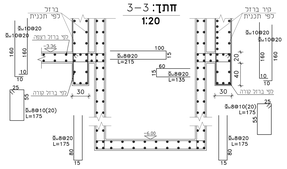

תכנית זו

כסדרה	לעיון	לביצוע
☒	☐	☐

מקרא

- קיר במון מפוסק
- קיר במון שתול
- קיר במון המשך
- עמוד- המשך
- עמוד מפוסק
- עמוד שתול
- שדרה/איר המשך של קיר/עמוד

הערה:
המבנה אחראי לגישות עלו לגבוהה.
כל הפרוזה המודגש למתבנן על כל שלוחה, אך אי הוספה אז לבנות אינה מה שנעשה שם.
אינה מהווה עדות בלתי מלא הקיר, הוספת הגריזל יש לבנות אז הרצפה.

בטון ב-30 לפי ת"י 118
מוטות פלדה מעולים
לפי ת"י 466 חלק 3
מוטות סטוג 400W1 500W
רשת מוטות פלדה
מעולים לפי ת"י 580

מפלס אב
מפלס מדרגה
-3.36 מדרגה
ק-2

ק"מ-1:50	שרטט: מרסל עבאנ
	בקר: נעאמנה מופדי

תאריך	מהדורה	הערות
02.07.24	1	לכסדרה

שם הפרויקט: בית ספר יסודי -24 כיתות + אולם מפוזם
הזמן עבור: עיריית בת ים
מבנה: בת ים /דיסקוטק
work/2024/

נעאמנה מופדי
מהנדס בנין
34המלאכה 8, בית שמאי-ג'ת
מס'ר:04/8853222
מס'ר:04/6745003
נייד:0505660338
e-mail: MufadiEngineer@gmail.com