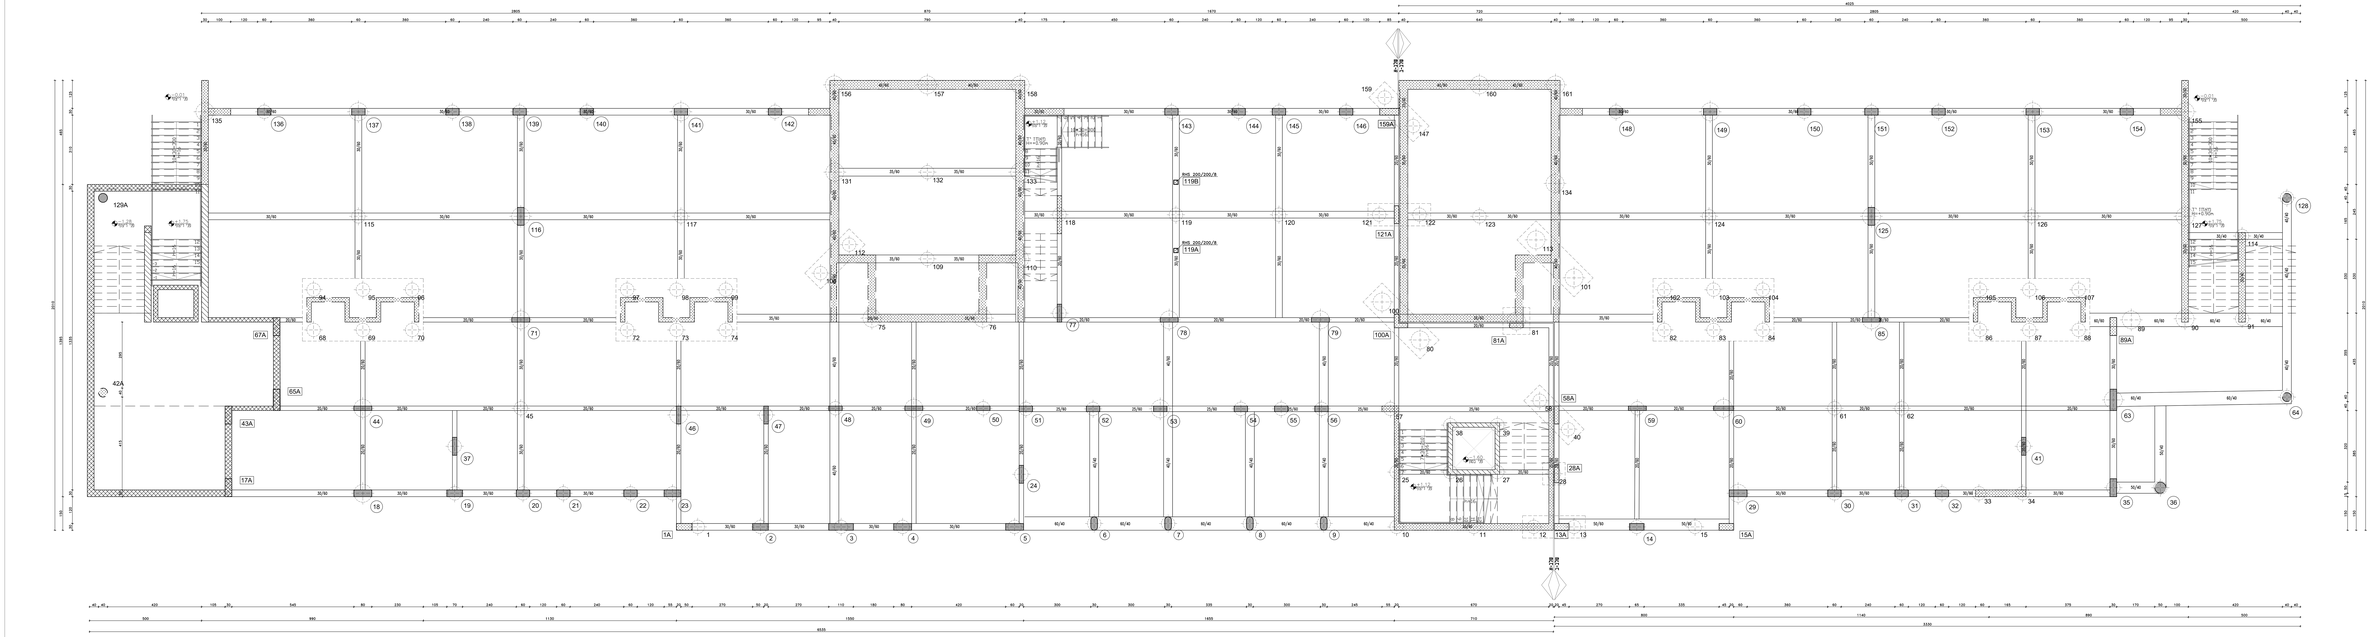

חתך טיפוסי בקורת רצפה
1:20

חתך: 1-1
1:20

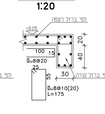

חתך: 2-2
1:20

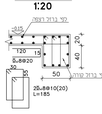

חתך: 3-3
1:20

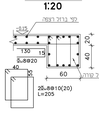

חתך: 4-4
1:20

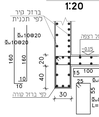

חתך: 5-5
1:20

חתך: 6-6
1:20

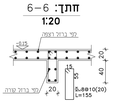

חתך: 7-7
1:20

חתך: 8-8
1:20

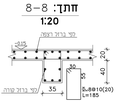

חתך: 9-9
1:20

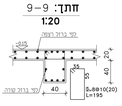

קורות פיתוח
1:20

תכנית זו

כמבוצע | נעוץ | כבצוע

מפתח

- קיר בטון מפסיק
- קיר בטון מחזיק
- קיר בטון משמש
- עמוד מפשיך
- עמוד מפסיק
- עמוד מחזיק
- עמודיעיר המשך על פירומוחד

הערות:
הבנין אדא לצידות עבו כבוזיב
כל הבדיות המדדים ומתנון על כל
מנת אי המאמה אי בבנה
אלקשאם מה עבאיב בתכנית כלא
מאבר המבנה
מנגי הנמנה הבריזו יש בבנוב את
הרשמה

בטון ב-30 לפי ת"118
מומות פכזה מעולנים
לפי ת"י 466 חכק 3
מומות מסוג 500W1400W
רשת מומומות פכזה
מעולנים לפי ת"י 580

עמליב אל+ב

מספר שרטוט	ק-3
מפלס אפס	-0.18 מ"מ

מ"ק-1:50	עורכ: טרסו בוגאן
	בינ: נעאמנה מוסדי

תאריך	מהדורה	הערות
02.07.24	1	כמבוצ

שם המדינה: בית ספר יסודי -24 כיתות + אולם ספורט

הוכן עבור:

קנ"מ: 1:50 עדיית בת ים

תאריך: 02/07/2024

נעאמנה מוסדי
מהנדס בנין
אדריכלות ופיתוח
34 הרצל ראש-העמק
טלפון: 04/8853222
פקס: 04/6745003
נייד: 0505860338
e-mail: ms@mustadi-eng.com