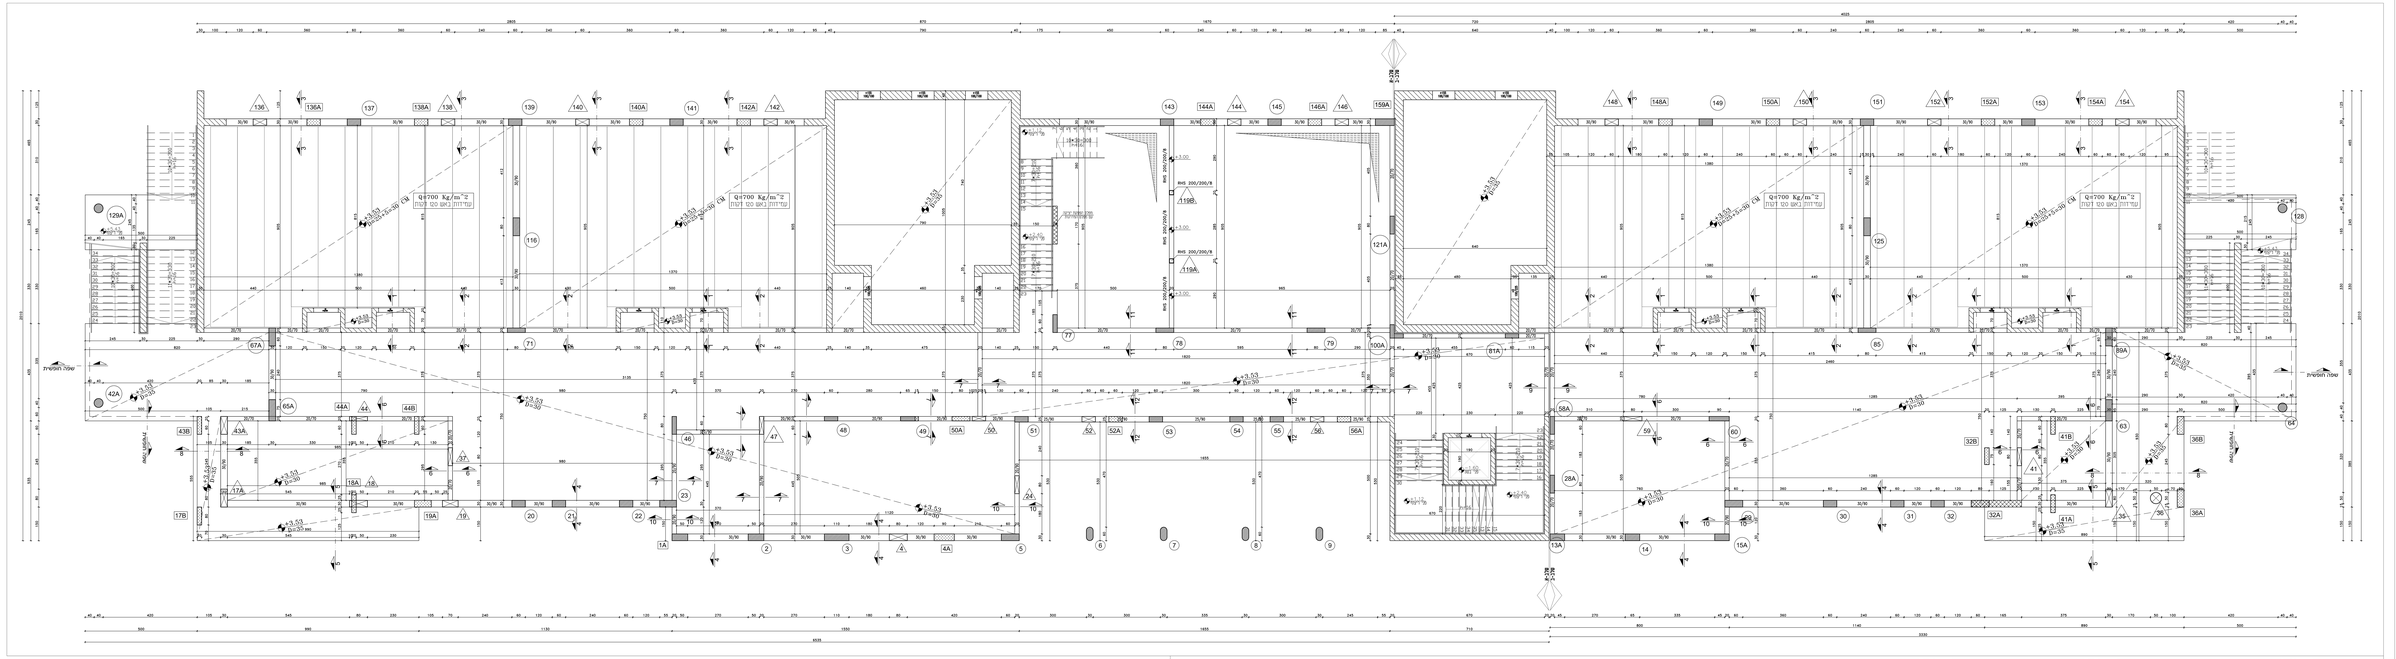
Q=700 kg/m^2
עדיפות (אם טרם רשום)
שטח הטיפולית
מבנה מגורים
מבנה מגורים
מבנה מגורים
מבנה מגורים
RHS 200/200/8
RHS 200/200/8
RHS 200/200/8
RHS 200/200/8
מבנה מגורים
מבנה מגורים
מבנה מגורים
מבנה מגורים