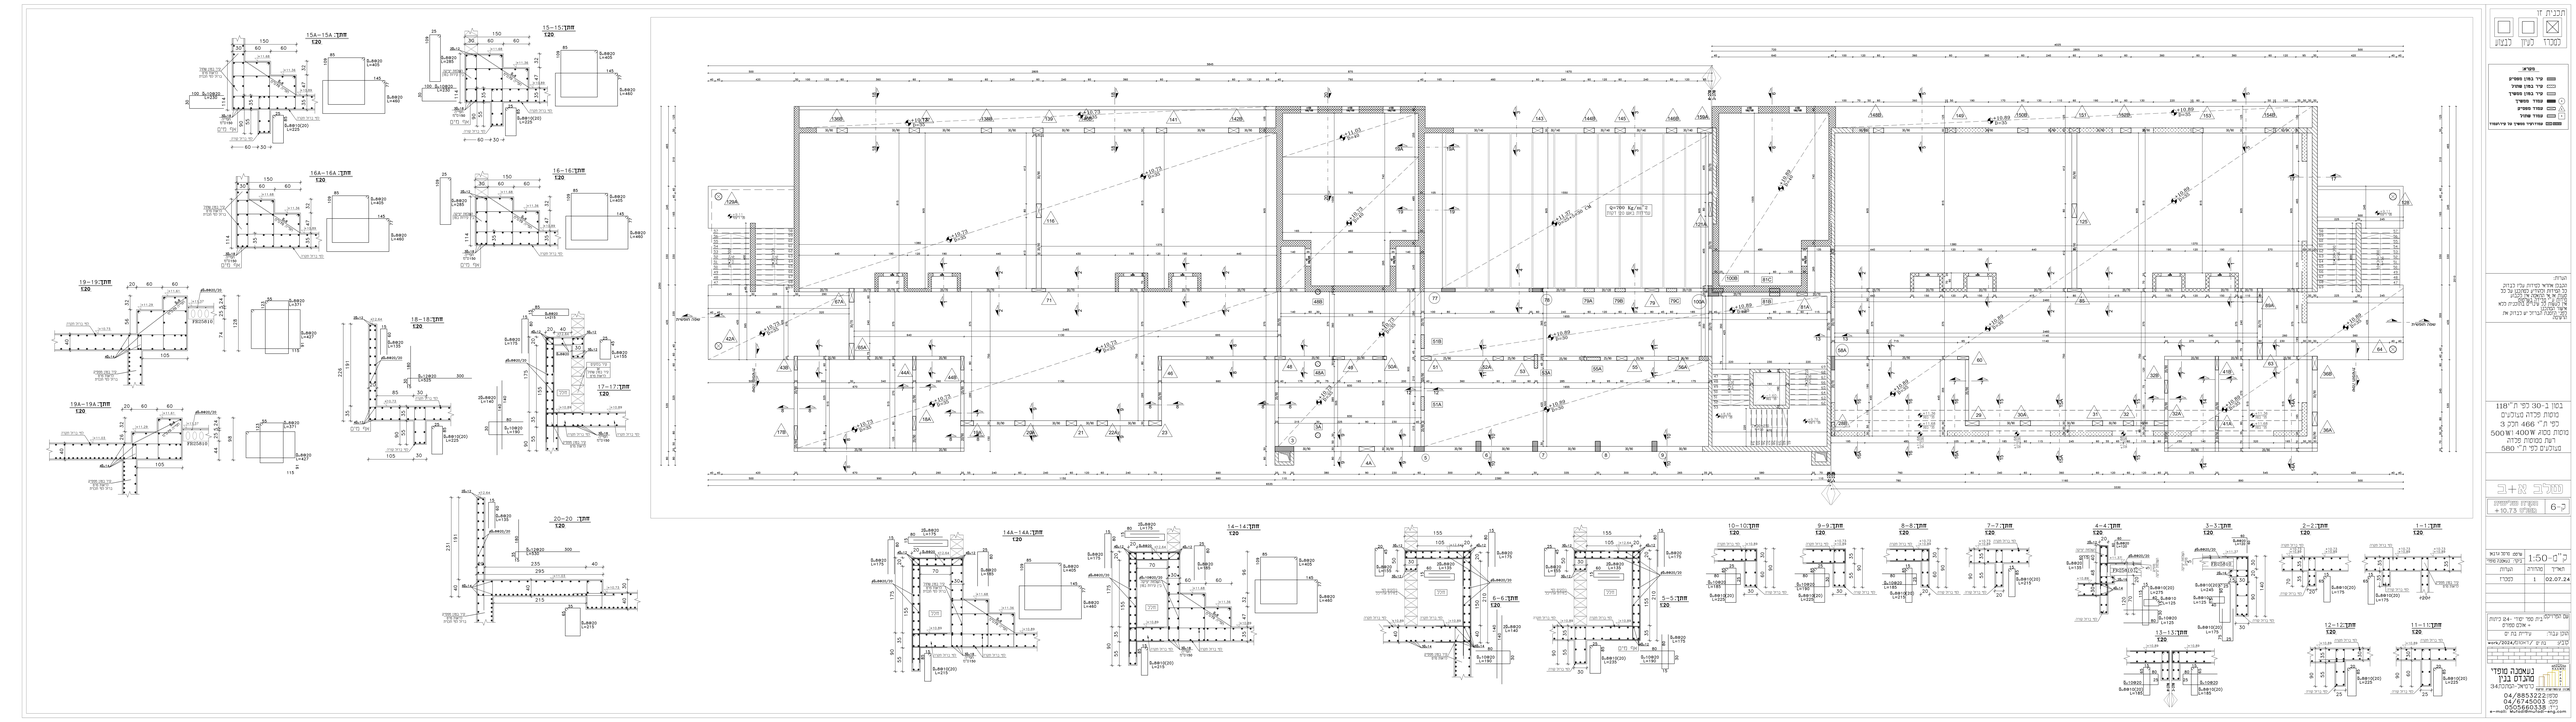
15A-15A :תחתון
15-15 :תחתון
16A-16A :תחתון
16-16 :תחתון
19-19 :תחתון
18-18 :תחתון
17-17 :תחתון
19A-19A :תחתון
20-20 :תחתון
14A-14A :תחתון
14-14 :תחתון
6-6 :תחתון
5-5 :תחתון
10-10 :תחתון
9-9 :תחתון
8-8 :תחתון
7-7 :תחתון
4-4 :תחתון
3-3 :תחתון
2-2 :תחתון
1-1 :תחתון
13-13 :תחתון
12-12 :תחתון
11-11 :תחתון
הבנין אחיד בחיבה עבין בבנין
מדרגות מגדלת סמוכים
מקום א' מסמה מדרגות
מקום ב' מסמה מדרגות
מקום ג' מסמה מדרגות בכא
מקום מדרגות ל' ג בבנין אל
מקום
בסמן 39-ג כפר ה"118
מוסת מכלה מעלעים
הפ"מ 466 ומכ 3
מוסת מכנ 400W|500
רשם מוסת מכלה
מעלעים פ' ה" 580
מבנה 6-ג
+10.73 מפלס
1:50-ק"מ
מאי 02.07.24
מהדורה I
מבנה בנין
בית ספר יסודי -24 כיתות
אבן שמואל
בית בגלה
בית ר' ל"ל
בשמכה מוסד
מגדל בנין
אדריכלים בע"מ רח' הרצל 34 בת ים
04/6853222 פקס
04/6745003 טל.
mail@bmb-arch.com