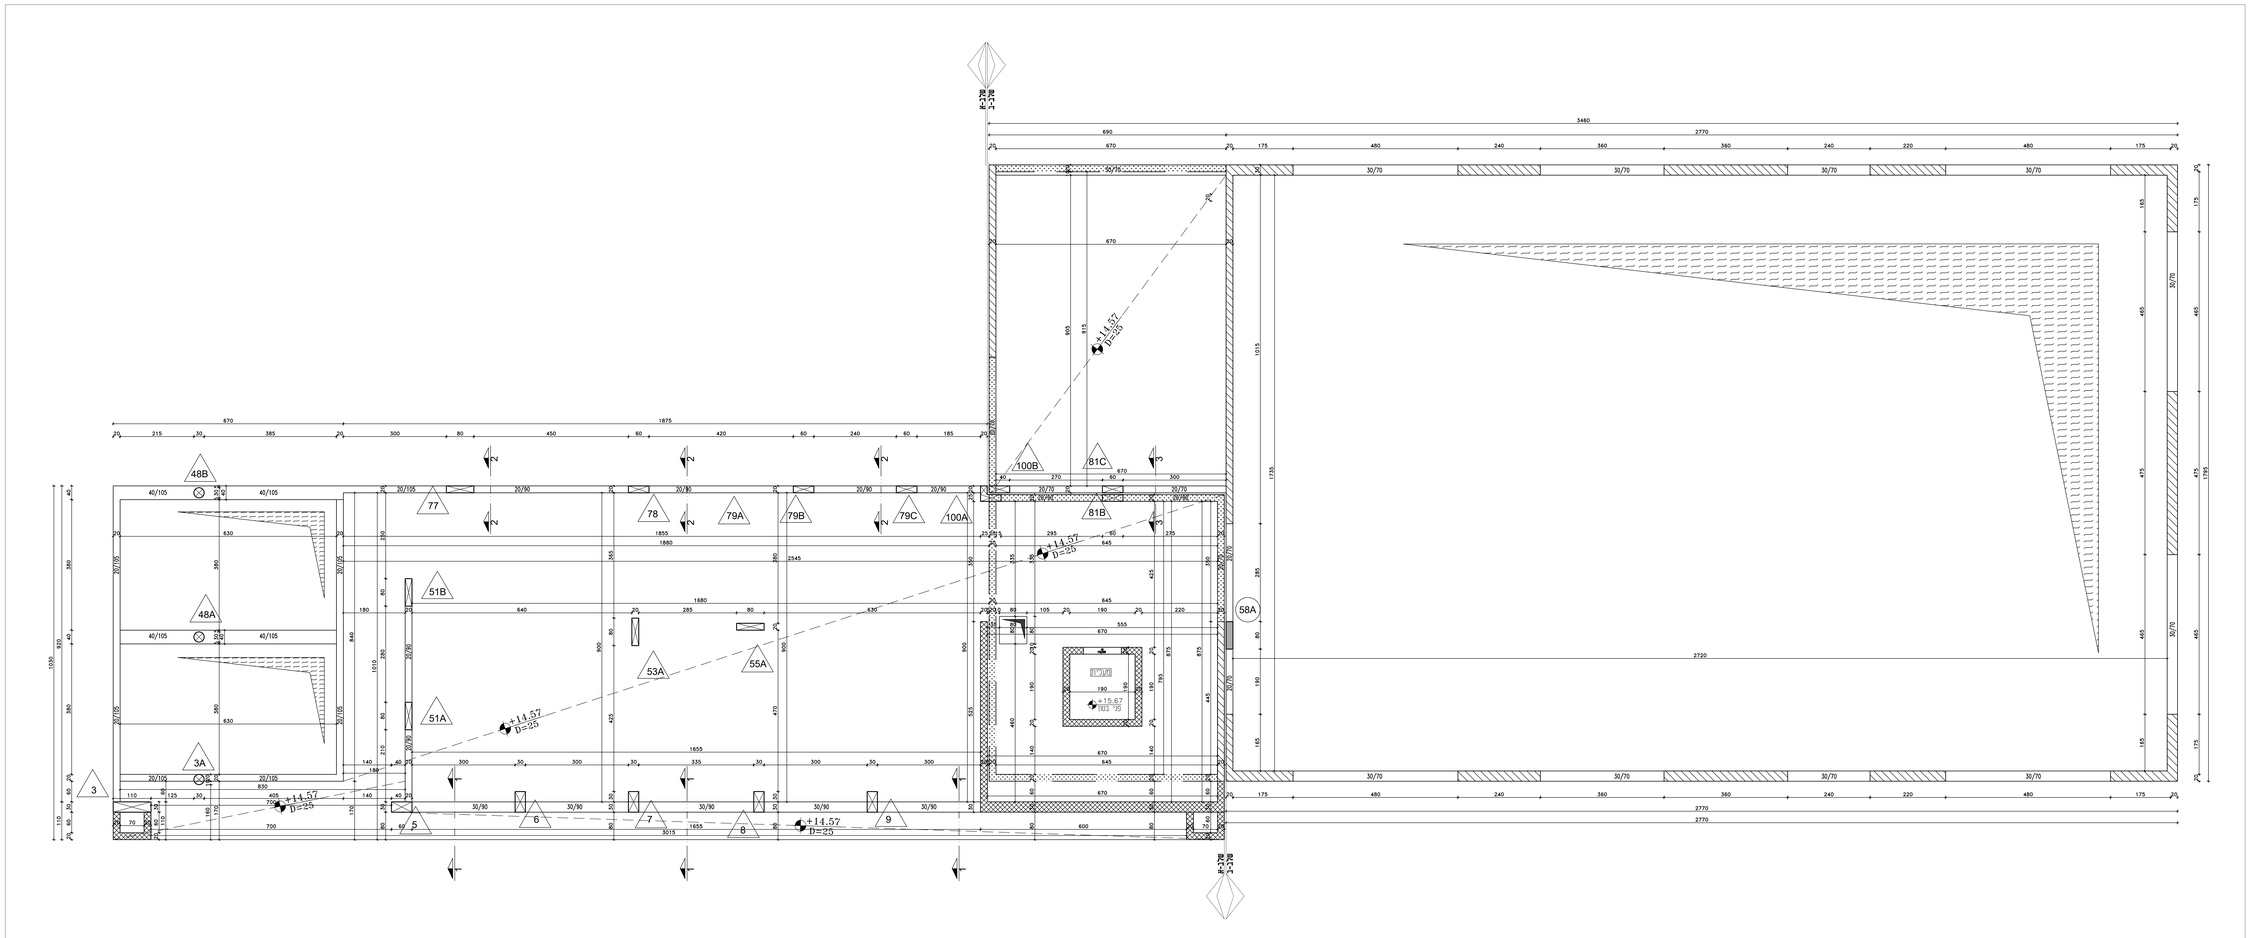

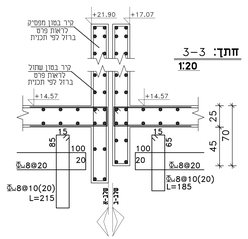

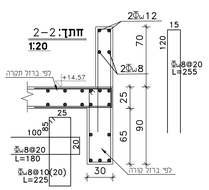

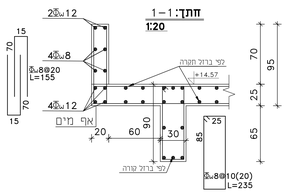

תכנית זו

כמכרז	לעיון	לבצוע
☒	☐	☐

מקרא:

- קיר בטון מפסיק
- קיר בטון שתול
- קיר בטון ממשיך
- עמוד ממשיך
- עמוד מפסיק
- עמוד שתול
- עמודופיר ממשיך על קירועמוד

הערות:
הבנכן אחראי לסידות עליו לבדוק
כל המידות והנהוגים למתקנן על כל
סעות אי אי התאמה אין לקבוע
מידות ע"י מדידה בשרטוט
אין לעשות כל שנויים בתוכנית ללא
אישור המתכנן
לפני הזמנת הברזל יש לבדוק את
הרשומה

בטון ב-30 לפי ת"118
מוטות פלדה מצולעים
לפי ת"י 466 חלק 3
מוטות מסוג 500W1400W
רשת ממוטות פלדה
מצולעים לפי ת"י 580

טקלב א+ב

ק-7	הקרה רביעית מפלס +14.57

ק"מ-1:50	שרטט: מרטל גדבאן
	ביקר: נעאמנה מופדי

תאריך	מהדורה	הערות
02.07.24	1	כמכרז

שם הפרויקט: בית ספר יסודי -24 כיתות + אולם ספורט

הוכן עבור: עיריית בת ים

קובץ: בת ים /דאטום/work/2024

נעאמנה מופדי
מהנדס בנין
כרמיאל-המתכת34
מכון עוסמנעמנה ופיגוח
טלפון: 04/8853222
פקס: 04/6745003
נייד: 0505660338
e-mail: Mufadi@mufadi-eng.com