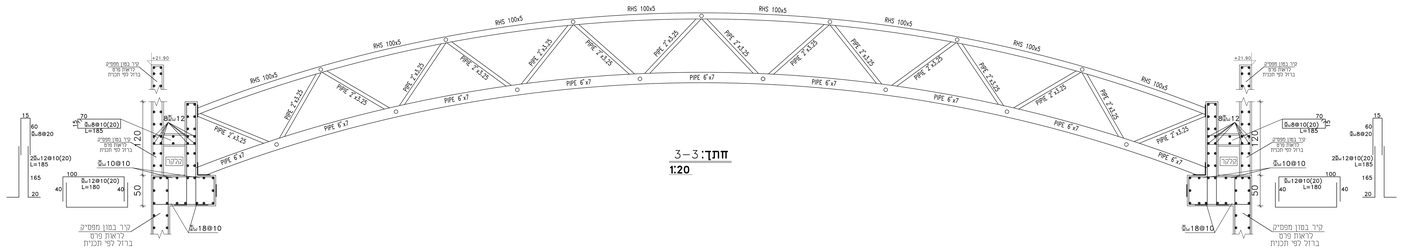

חתך: 3-3
1:20

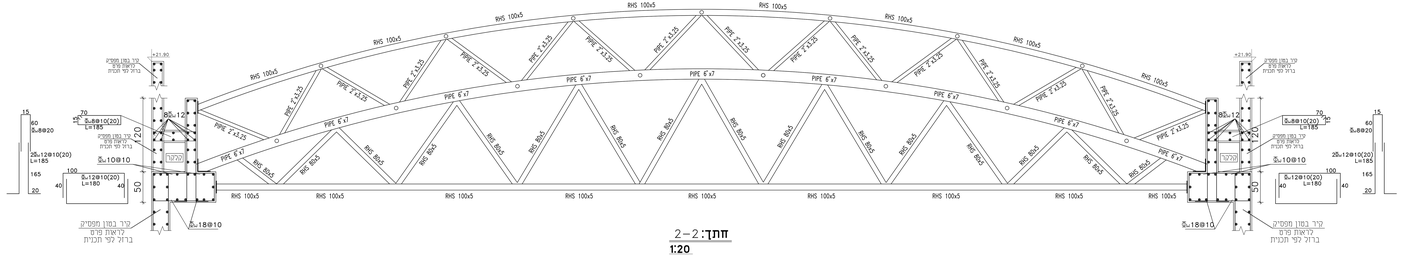

חתך: 2-2
1:20

חתך: 1-1
1:20

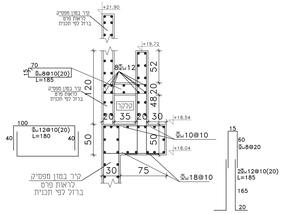

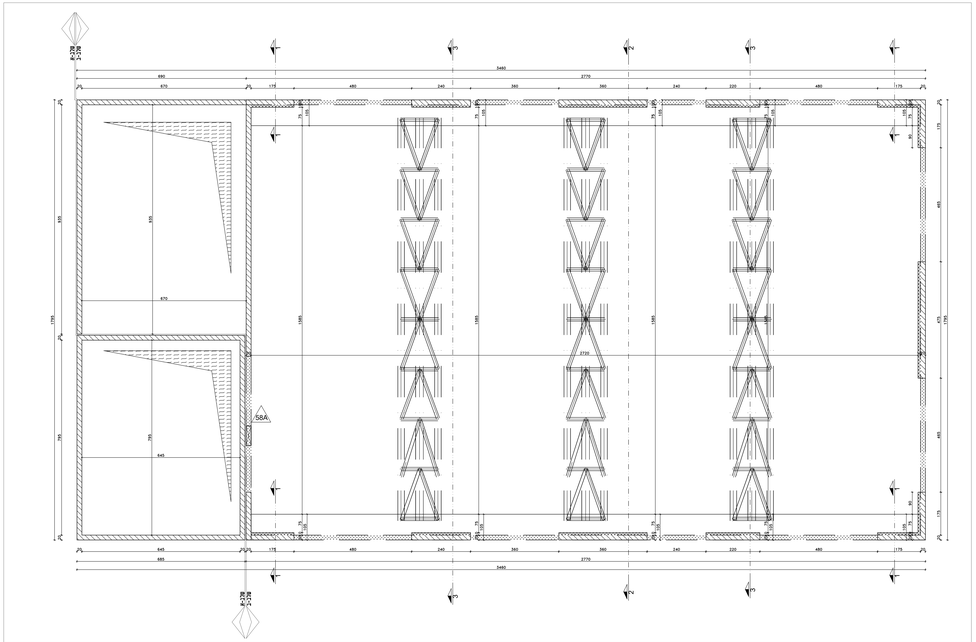

תכנית זו

לסכרד	לעיון	לביצוע
☒	☐	☐

מפרא:

- קיר בטון מפסיק
- קיר בטון שחול
- קיר בטון משקע
- עמוד משקע
- עמוד מפסיק
- עמוד שחול
- עמודיקר משקע על ריצוף/אדמה

הערות:
הבנין אדאר לטירות עניו לבניה.
כל הפרוט והמידע המסומן על כל מפות אי אי המאמה אין לבצוע מדידה. כל מידה בפועל.
אין בעשות כל עניים בתוכנית כלא תיקון המכנו.
תיקון המסמה הבריזה יש לבנוס את מרעיה.

בטון ב-30 לפי ת"י 118
מוטות פלדה מעוגלים
לפי ת"י 466 חלק 3
מוטות מסוג 400W ו500W
רשת מסוגות פלדה
מעוגלים לפי ת"י 580

מקרא א+ב

מפלס 22 מפלס +18.54 מ"מ	ק-8

שרטט: מרטל גוגא	ק"מ-1:50
בקיר: נעאמנה מופדי	
תאריך	מהדורה	הערות
02.07.24	1	למכרז

שם הפרויקט: בית ספר יסודי -24 כיתות + אלם ספורט
הכן עבור: עיריית בת ים
מבנין: work/2024/אחוזת/בת ים

נעאמנה מופדי
מהנדס בנין
רח' עוזיאל 34 כרמיאל-המחנה
טלפון: 04/8853222
פקס: 04/6745003
נייד: 0505660338
e-mail: Mufadi@multi-eng.com